

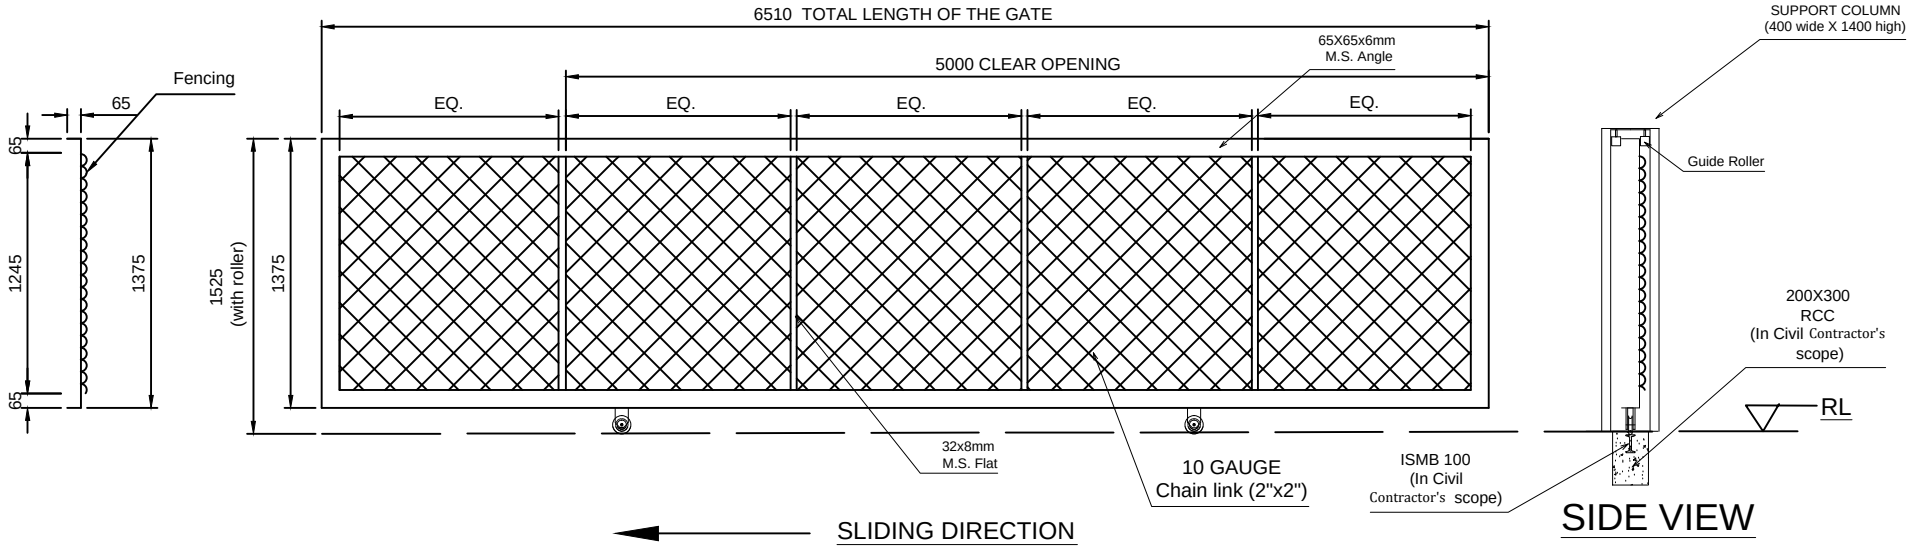


SIDE VIEW
(with SUPPORT COLUMN)

Clear Opening size - 5000X1525mm
Total length of gate - 6510X1525mm
No. Of Column - 4 nos.
Factory paint finish - Red oxide primer coat with Enamel paint Finish
NOTE :- *ALL REQ. CIVIL WORK WILL BE IN YOUR CONTRACTOR'S SCOPE.
NOTE:- As per calculation only 2 wheels are required for Sliding Gate.

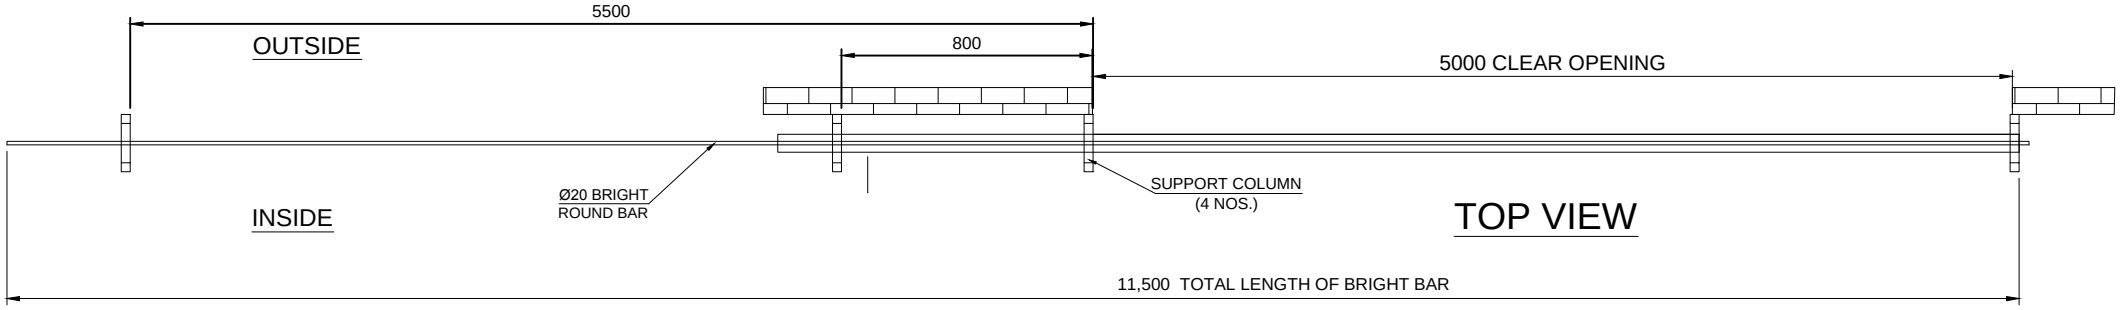

TOP VIEW

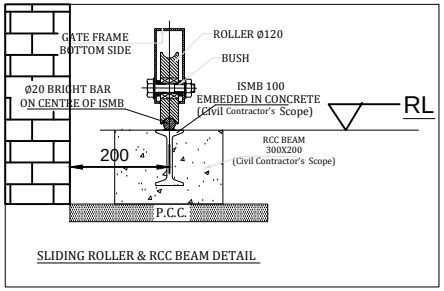

SLIDING ROLLER & RCC BEAM DETAIL

This drawing & designing is the property of NIHVA TECHNOLOGIES. Not be sold or copy to any other concern.

TITLE	FENCED SLIDING GATE		NIHVA TECHNOLOGY PVT. LTD. PUNE
	SIGN	DATE	NIHVA TECHNOLOGIES PVT. LTD.
DRAWN	OMKAR	13/01/16	CLIENT - REWARD CONSTRUCTION
CHECK	ANIL	13/01/16	PROJECT - GIVAUDAN
REV.	00		SITE - RANJANGAON MIDC
APPROVAL	R.Kulkarni	13/01/16	

Tel : 020 66304033
Email:- info@nihva.com
Website:- www.nihva.com

If any queries contact : projects@nihva.com	SCALE: --	WT:	SHEET: 01 OF 01
ALL DIMENSION ARE IN mm			