

Abbrevation's:
WOW-Wall Opening Width
WOH-Wall Opening Height
UC-Under Cut
FFL-Finished Floor Level

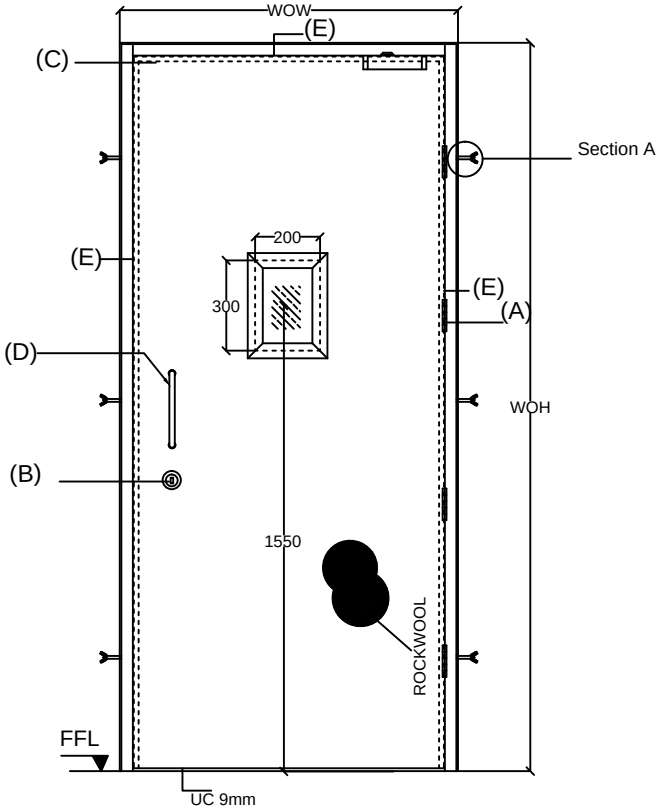

ELEVATION



TOP VIEW

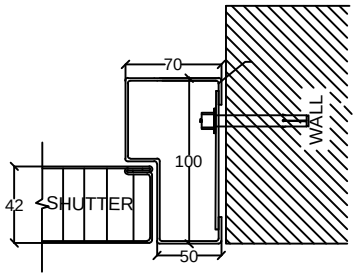

Section A

ASSESORIES DETALES

(A) HINGES: DORMA MAKE

(B) LOCK : DORMA MAKE.

(C) DOOR CLOSER: DORMA MAKE.

(D) HANDLE : 'D' HANDLE (BOTH SIDE) dia 200mmX22mm
DORMA MAKE.

(E) DOOR OPENING : LHS INSIDE OPENING.

Shutter thickness : 42 mm
Frame Sheet thick : 1.5mm
Shutter sheet thick : 1.2mm
Fixing : On Solid Brick plastered wall with Anchors

NOTE:- *All Dimensions are in mm.
*Tolerance:-All Linear Dimensions ±3mm,Others ±0.5mm.
*The Drawing Is For Location of Hardware only. Drawing Does Not Represent The Hardware For More Clarity, Please Go Through Hardware Broucher.

COLOR
1.(RAL 9010)

Steel door size		
WOW	WOH	QUANTITY
1000mm	2200mm	02 NOS

NOTE - 1. POLYCARBONET SHEET VISION PANEL REQ.

REV NO	DRAWN	DATE	REMARK
R01	P.V.A	18.07.19	1. DOOR OPENING CHANGED

This drawing & designing is the property of NIHVA TECHNOLOGIES. Not be sold or copy to any other concern.

TITLE: STEEL DOOR (SINGLE LEAF)

NIHVA TECHNOLOGIES PVT. LTD.

NIHVA TECHNOLOGY PVT. LTD. PUNE
Tel : 020 66304033
Email:- info@nihva.com
Website:-www.nihva.com

	NAME	SIGN.	DATE
DRAWN	P.V.A		17.07.19
CHECK	V.M.T		17.07.19
APPRD.			

If any queries contact: design@nihva.com

ALL DIMENSION ARE IN mm

CLIENT - FERRERO INDIA PVT LTD
PROJECT -
SITE LOCATION - BARAMATI
DWG. NO. - NIHVA/19-20/0050/R01 REV.:-R01
SCALE: NTS WT: SHEET: 01 OF 01