

FOR TENDER

GROUND FLOOR PLAN

SERVICES CUTOUT LEGEND	
S1	HVAC & Plumbing Shaft (255mm x 1355mm)
S2	Plumbing Shaft (650mm x 200mm)
S2a	Plumbing Shaft (900mm x 300mm)
S2c	Plumbing Shaft (870mm x 300mm)
S3	Electrical Shaft (900mm x 300mm)
S4	Eliminated
S5	Storm water Shaft (125mm x 175mm)
S6	Electrical junction box Cutout (450mm x 450mm)
S7	Electrical junction box Cutout (600mm x 600mm)

MATERIAL LEGEND	
	Light Weight Partition
	230mm thk Brick wall
	115mm thk Brick wall
	200mm thk Light weight AAC wall
	100mm thk Light weight AAC wall
	RCC columns
	115mm thk. brick ledge wall
	230mm thk. concrete patli
	100mm x 100mm non- structural concrete for window jambs

ARCHITECT:

SJK ARCHITECTS

302-303,VEENA KILLEDAR INDL.EST.
,10/14,PAIS STREET, BYCULLA-WEST,
MUMBAI-400 011
TEL.NO.: 022- 2300 8766, 022-23008761
FAX.NO. : 022-2309 0983
email: design @sjkarchitect.com

This "drawing" is the copyright of **SJK Architects** and shall not be used for any purpose other than that for which it has been loaned.

STRUCTURAL:

MANJUNATH & CO.
CONSULTING ENGINEERS
#236 5th CROSS,
K.G. NAGAR,
BANGALORE - 560019
TEL.NO.: 080- 26616610
email:
manjaxe2010@gmail.com

MEP:

MEPTEK CONSULTANTS
Science Of Total Comfort

-2;665, Millennium, Veer Savarkar Marg,
Dadar (W),
Mumbai-400028.
nimish.shah@meptekconsultants.com

PMC:

GENERAL NOTES:

1. All Dimensions Are In MILLIMETERS Unless Otherwise Specified.
2. All Dimensions Specified Are UnFinished Dimensions, Unless Otherwise specified.
3. All structural dimensions shall be referred as per Consultants' drawings.
4. DO NOT SCALE Drawing
5. Any Discrepancies In the Drawings Shall Be Brought To The Notice Of The Architect,Prior to Execution.

SPECIFIC NOTES / LEGEND:

1. All Boxed Dimensions are finished dimensions (i.e. after plaster, dado etc). Remaining are unfinished dimensions
2. All External surfaces of walls shall have 20mm thk External Sandfaced Plaster.
3. All Internal surfaces of walls shall have 12mm thk Backing Coat of Plaster + POP Punning. (Except toilet walls, which will receive waterproofing and dado finish).
4. Refer to Site Plan for Otla all around the Building.

NORTH

REVISION NOTES:

PROJECT:

NAGPUR HOUSE

CLIENT:

JAIN FAMILY

REV NO: R0
DATE OF REVISION:

DRAWING NO: NH-ID-PLN-001-R0

DRAWING TITLE:

GROUND FLOOR PLAN

DATE OF ISSUE: 11-02-2021

SCALE: 1:75 **SHEET SIZE:** A2

PURPOSE : FOR REFERENCE ONLY



FOR TENDER

FIRST FLOOR PLAN

SERVICES CUTOUT LEGEND	
S1	HVAC & Plumbing Shaft (255mm x 1355mm)
S2	Plumbing Shaft (650mm x 200mm)
S2a	Plumbing Shaft (900mm x 300mm)
S2b	Plumbing Shaft (1150mm x 300mm)
S3	Electrical Shaft (900mm x 300mm)
S4	Eliminated
S5	Storm water Shaft (125mm x 175mm)

MATERIAL LEGEND	
	Light Weight Partition
	230mm thk Brick wall
	115mm thk Brick wall
	200mm thk Light weight AAC wall
	100mm thk Light weight AAC wall
	RCC columns
	115mm thk. brick ledge wall
	230mm thk. concrete patli
	100mm x 100mm non- structural concrete for window jambs

ARCHITECT:

SJK ARCHITECTS

302-303,VEENA KILLEDAR INDL.EST. ,10/14,PAIS STREET, BYCULLA-WEST, MUMBAI-400 011
TEL.NO.: 022- 2300 8766, 022-23008761
FAX.NO. : 022-2309 0983
email: design @sjkarchitect.com

This "drawing" is the copyright of **SJK Architects** and shall not be used for any purpose other than that for which it has been loaned.

STRUCTURAL:

MANJUNATH & CO. CONSULTING ENGINEERS #236 5th CROSS, K.G. NAGAR, BANGALORE - 560019
TEL.NO.: 080- 26616610
email: manjaxe2010@gmail.com

MEP:

MEPTEK CONSULTANTS
Engineering Smart Solutions

-2;665, Millennium, Veer Savarkar Marg, Dadar (W), Mumbai-400028.
nimish.shah@meptekconsultants.com

PMC:

GENERAL NOTES:

1. All Dimensions Are In MILLIMETERS Unless Otherwise Specified.
2. All Dimensions Specified Are UnFinished Dimensions, Unless Otherwise specified.
3. All structural dimensions shall be referred as per Consultants' drawings.
4. DO NOT SCALE Drawing
5. Any Discrepancies In the Drawings Shall Be Brought To The Notice Of The Architect,Prior to Execution.

SPECIFIC NOTES / LEGEND:

1. All Boxed Dimensions are finished dimensions (i.e. after plaster, dado etc). Remaining are unfinished dimensions.
2. All External surfaces of walls shall have 20mm thk External Sandfaced Plaster.
3. All Internal surfaces of walls shall have 12mm thk Backing Coat of Plaster + POP Punning. (Except toilet walls, which will receive waterproofing and dado finish).

NORTH

REVISION NOTES:

PROJECT:

NAGPUR HOUSE

CLIENT:

JAIN FAMILY

REV NO: R0
DATE OF REVISION:

DRAWING NO: NH-ID-PLN-002-R0

DRAWING TITLE:

FIRST FLOOR PLAN

DATE OF ISSUE: 11-02-2021

SCALE: 1:75 **SHEET SIZE:** A2

PURPOSE : FOR REFERENCE ONLY



FOR TENDER

SECOND FLOOR PLAN

SERVICES CUTOUT LEGEND	
S1	HVAC & Plumbing Shaft (255mm x 1355mm)
S2	Plumbing Shaft (650mm x 200mm)
S2a	Plumbing Shaft (900mm x 300mm)
S2b	Plumbing Shaft (1150mm x 300mm)
S3	Electrical Shaft (900mm x 300mm)
S4	Eliminated
S5	Storm water Shaft (125mm x 175mm)

MATERIAL LEGEND	
	Light Weight Partition
	230mm thk Brick wall
	115mm thk Brick wall
	200mm thk Light weight AAC wall
	100mm thk Light weight AAC wall
	RCC columns
	115mm thk. brick ledge wall
	230mm thk. concrete patli
	100mm x 100mm non- structural concrete for window jambs

ARCHITECT:

SJK ARCHITECTS

302-303,VEENA KILLEDAR INDL.EST, ,10/14,PAIS STREET, BYCULLA-WEST, MUMBAI-400 011
TEL.NO.: 022- 2300 8766, 022-23008761
FAX.NO. : 022-2309 0983
email: design @sjkarchitect.com

This "drawing" is the copyright of **SJK Architects** and shall not be used for any purpose other than that for which it has been loaned.

STRUCTURAL:

MANJUNATH & CO. CONSULTING ENGINEERS #236 5th CROSS, K.G. NAGAR, BANGALORE - 560019
TEL.NO.: 080- 26616610
email: manjaxe2010@gmail.com

MEP:

MEPTEK CONSULTANTS
Complete MEP Design Solutions

-2:665, Millennium, Veer Savarkar Marg, Dadar (W), Mumbai-400028.
nimish.shah@meptekconsultants.com

PMC:

GENERAL NOTES:

1. All Dimensions Are In MILLIMETERS Unless Otherwise Specified.
2. All Dimensions Specified Are UnFinished Dimensions, Unless Otherwise specified.
3. All structural dimensions shall be referred as per Consultants' drawings.
4. DO NOT SCALE Drawing
5. Any Discrepancies In the Drawings Shall Be Brought To The Notice Of The Architect,Prior to Execution.

SPECIFIC NOTES / LEGEND:

1. All Boxed Dimensions are finished dimensions (i.e. after plaster, dado etc). Remaining are unfinished dimensions.
2. All External surfaces of walls shall have 20mm thk External Sandfaced Plaster.
3. All Internal surfaces of walls shall have 12mm thk Backing Coat of Plaster + POP Punning. (Except toilet walls, which will receive waterproofing and dado finish).

NORTH

REVISION NOTES:

PROJECT:

NAGPUR HOUSE

CLIENT:

JAIN FAMILY

REV NO: R0
DATE OF REVISION:

DRAWING NO: NH-ID-PLN-003-R0

DRAWING TITLE:

SECOND FLOOR PLAN

DATE OF ISSUE: 11-02-2021

SCALE: 1:75 **SHEET SIZE:** A2

PURPOSE : FOR REFERENCE ONLY



FOR TENDER

THIRD FLOOR PLAN

SERVICES CUTOUT LEGEND	
S1	HVAC & Plumbing Shaft (255mm x 1355mm)
S2	Plumbing Shaft (650mm x 200mm)
S2a	Plumbing Shaft (900mm x 300mm)
S2b	Plumbing Shaft (1150mm x 300mm)
S3	Electrical Shaft (900mm x 300mm)
S4	Eliminated
S5	Storm water Shaft (125mm x 175mm)

MATERIAL LEGEND	
	Light Weight Partition
	230mm thk Brick wall
	115mm thk Brick wall
	200mm thk Light weight AAC wall
	100mm thk Light weight AAC wall
	RCC columns
	115mm thk. brick ledge wall
	230mm thk. concrete patli
	100mm x 100mm non- structural concrete for window jambs

ARCHITECT:

SJK ARCHITECTS

302-303,VEENA KILLEDAR INDL.EST.
,10/14,PAIS STREET, BYCULLA-WEST,
MUMBAI-400 011
TEL.NO.: 022- 2300 8766, 022-23008761
FAX.NO.: 022-2309 0983
email: design @sjkarchitect.com

This "drawing" is the copyright of **SJK Architects** and shall not be used for any purpose other than that for which it has been loaned.

STRUCTURAL:

MANJUNATH & CO.
CONSULTING ENGINEERS
#236,5th CROSS,
K.G. NAGAR,
BANGALORE - 560019
TEL.NO.: 080- 26616610
email:
manjaxe2010@gmail.com

MEP:

MEPTEK CONSULTANTS

-2;665, Millennium, Veer Savarkar Marg,
Dadar (W),
Mumbai-400028.
nimish.shah@meptekconsultants.com

PMC:

GENERAL NOTES:

1. All Dimensions Are In MILLIMETERS Unless Otherwise Specified.
2. All Dimensions Specified Are UnFinished Dimensions, Unless Otherwise specified.
3. All structural dimensions shall be referred as per Consultants' drawings.
4. DO NOT SCALE Drawing
5. Any Discrepancies In the Drawings Shall Be Brought To The Notice Of The Architect,Prior to Execution.

SPECIFIC NOTES / LEGEND:

1. All Boxed Dimensions are finished dimensions (i.e. after plaster, dado etc). Remaining are unfinished dimensions.
2. All External surfaces of walls shall have 20mm thk External Sandfaced Plaster.
3. All Internal surfaces of walls shall have 12mm thk Backing Coat of Plaster + POP Punning. (Except toilet walls, which will receive waterproofing and dado finish).

NORTH

REVISION NOTES:

PROJECT:

NAGPUR HOUSE

CLIENT:

JAIN FAMILY

REV NO: R0
DATE OF REVISION:

DRAWING NO: NH-ID-PLN-005-R0


DRAWING TITLE:

THIRD FLOOR PLAN

DATE OF ISSUE: 11-02-2021

SCALE: 1:75 **SHEET SIZE:** A2

PURPOSE : FOR REFERENCE ONLY

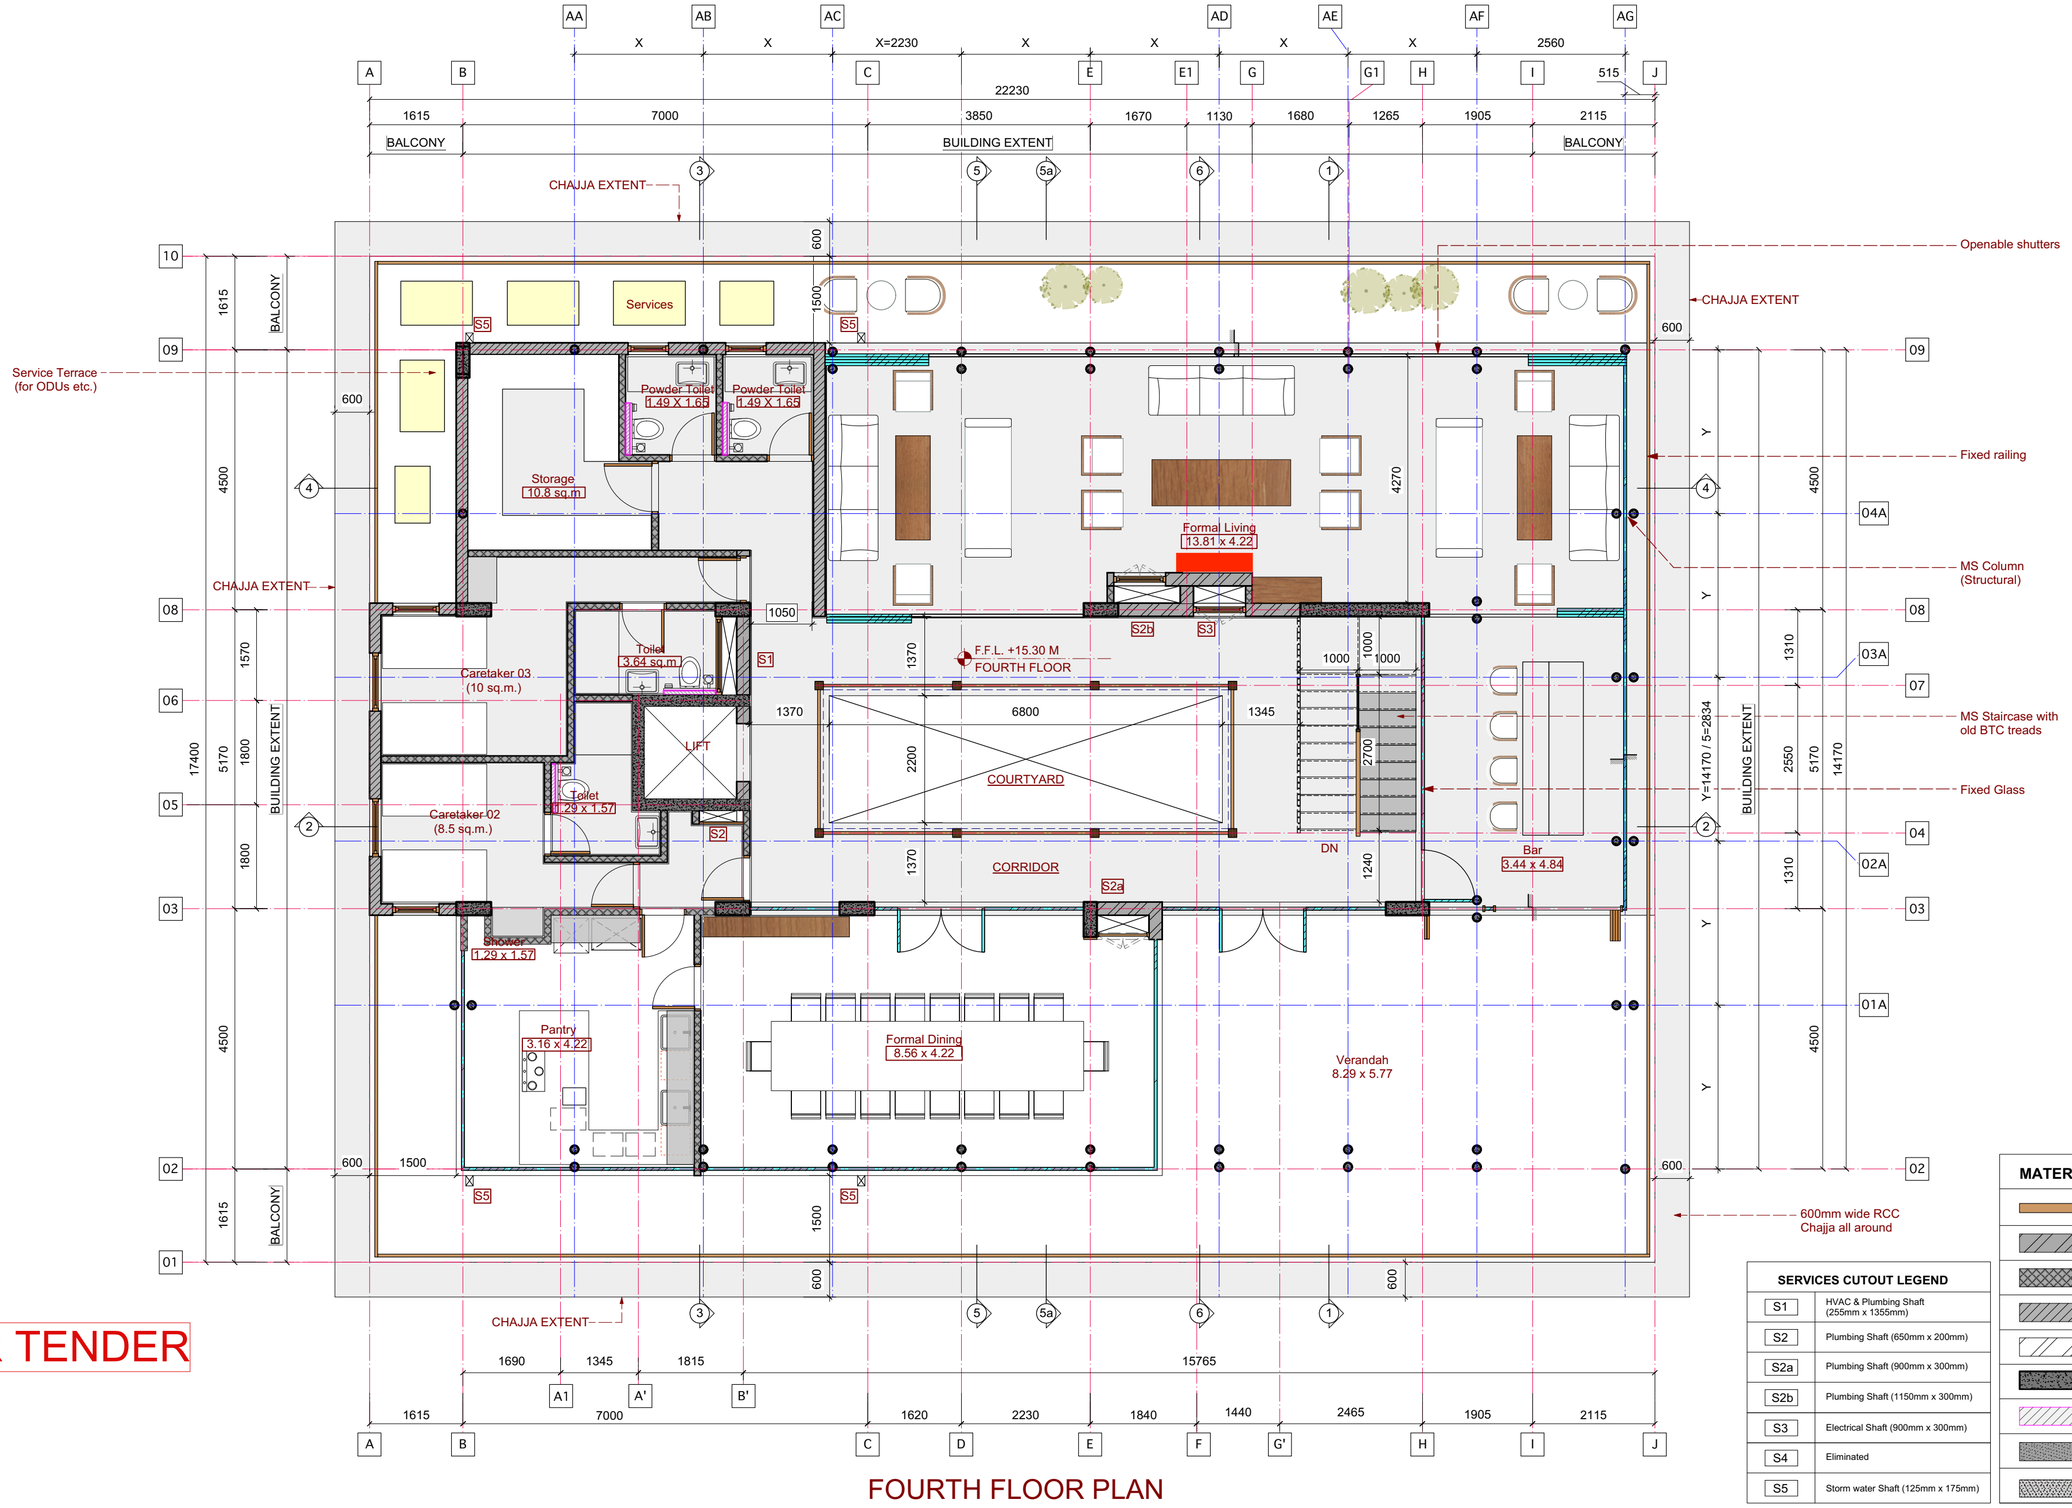

FOR TENDER

FOURTH FLOOR PLAN

MATERIAL LEGEND

	Light Weight Partition
	230mm thk Brick wall
	115mm thk Brick wall
	200mm thk Light weight AAC wall
	100mm thk Light weight AAC wall
	RCC columns
	115mm thk. brick ledge wall
	230mm thk. concrete patli
	100mm x 100mm non- structural concrete for window jambs

SERVICES CUTOUT LEGEND

S1	HVAC & Plumbing Shaft (255mm x 1355mm)
S2	Plumbing Shaft (650mm x 200mm)
S2a	Plumbing Shaft (900mm x 300mm)
S2b	Plumbing Shaft (1150mm x 300mm)
S3	Electrical Shaft (900mm x 300mm)
S4	Eliminated
S5	Storm water Shaft (125mm x 175mm)

ARCHITECT:

SJK ARCHITECTS

302-303,VEENA KILLEDAR INDL.EST. ,10/14,PAIS STREET, BYCULLA-WEST, MUMBAI-400 011
TEL.NO.: 022- 2300 8766, 022-23008761
FAX.NO. : 022-2309 0983
email: design @sjkarchitect.com

This "drawing" is the copyright of **SJK Architects** and shall not be used for any purpose other than that for which it has been loaned.

STRUCTURAL:

MANJUNATH & CO. CONSULTING ENGINEERS #236 5th CROSS, K.G. NAGAR, BANGALORE - 560019
TEL.NO.: 080- 26616610
email: manjaxe2010@gmail.com

MEP:

MEPTEK CONSULTANTS

-2;665, Millennium, Veer Savarkar Marg, Dadar (W), Mumbai-400028.
nimish.shah@meptekconsultants.com

PMC:

GENERAL NOTES:

1. All Dimensions Are In MILLIMETERS Unless Otherwise Specified.
2. All Dimensions Specified Are UnFinished Dimensions, Unless Otherwise specified.
3. All structural dimensions shall be referred as per Consultants' drawings.
4. DO NOT SCALE Drawing
5. Any Discrepancies In the Drawings Shall Be Brought To The Notice Of The Architect,Prior to Execution.

SPECIFIC NOTES / LEGEND:

1. All Boxed Dimensions are finished dimensions (i.e. after plaster, dado etc). Remaining are unfinished dimensions.
2. All External surfaces of walls shall have 20mm thk External Sandfaced Plaster.
3. All Internal surfaces of walls shall have 12mm thk Backing Coat of Plaster + POP Punning. (Except toilet walls, which will receive waterproofing and dado finish).

NORTH

REVISION NOTES:

PROJECT:

NAGPUR HOUSE

CLIENT:

JAIN FAMILY

REV NO: R0
DATE OF REVISION:

DRAWING NO: NH-ID-PLN-005-R0


DRAWING TITLE:

FOURTH FLOOR PLAN

DATE OF ISSUE: 11-02-2021

SCALE: 1:75 **SHEET SIZE:** A2

PURPOSE : FOR REFERENCE ONLY

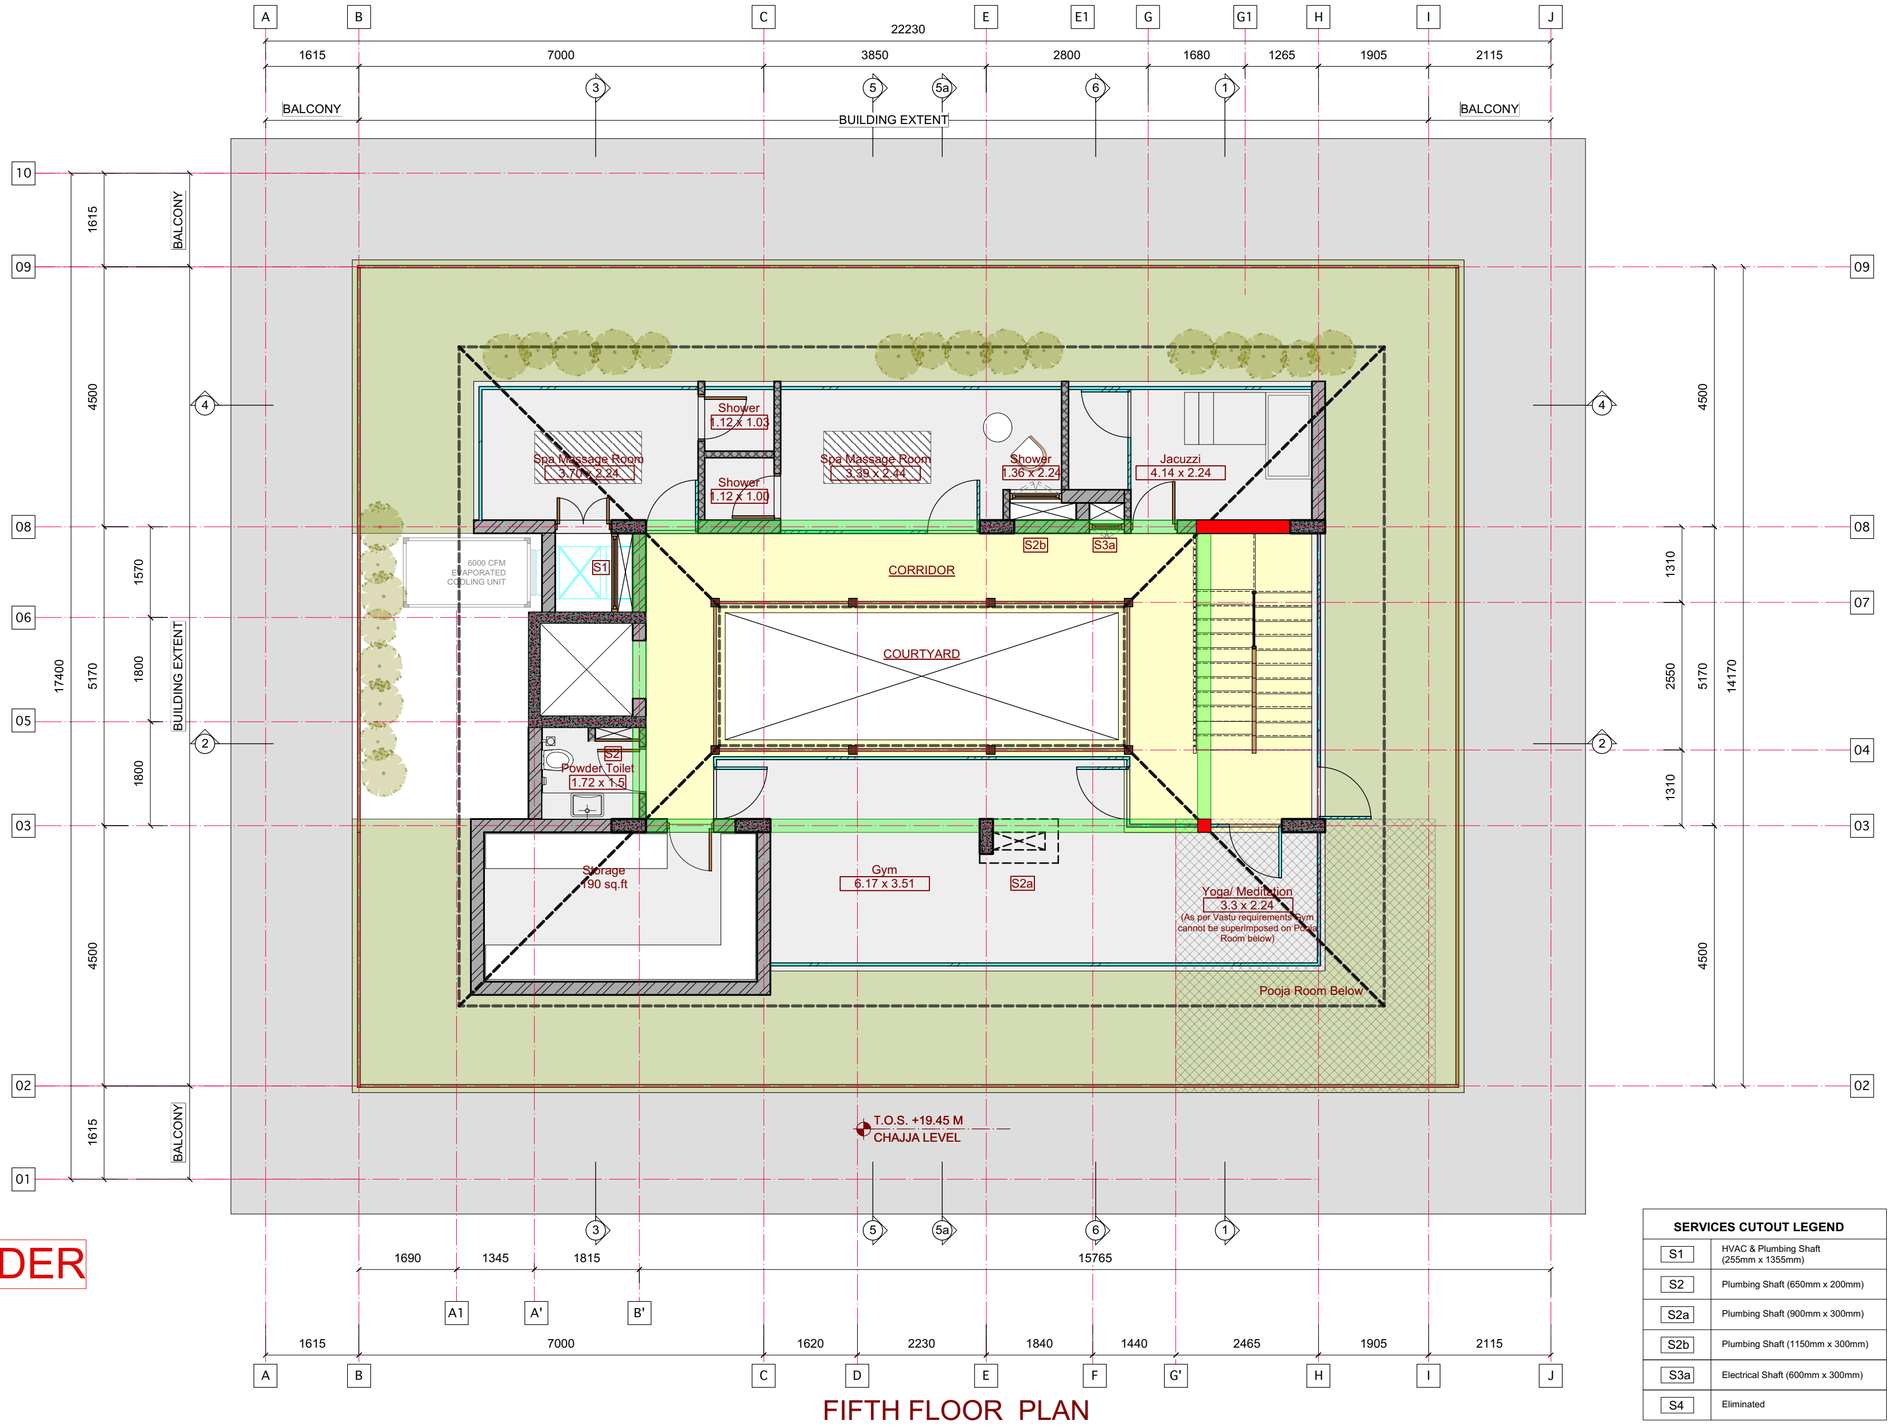

FOR TENDER

FIFTH FLOOR PLAN

SERVICES CUTOUT LEGEND	
S1	HVAC & Plumbing Shaft (255mm x 1355mm)
S2	Plumbing Shaft (650mm x 200mm)
S2a	Plumbing Shaft (900mm x 300mm)
S2b	Plumbing Shaft (1150mm x 300mm)
S3a	Electrical Shaft (600mm x 300mm)
S4	Eliminated

MATERIAL LEGEND	
	Light Weigth Partition
	230mm thk Brick wall
	115mm thk Brick wall
	200mm thk Light weight AAC wall
	100mm thk Light weight AAC wall
	RCC columns
	115mm thk. brick ledge wall
	230mm thk. concrete patli
	100mm x 100mm non- structural concrete for window jambs

ARCHITECT:

SJK ARCHITECTS

302-303,VEENA KILLEDAR INDL.EST.
,10/14,PAIS STREET, BYCULLA-WEST,
MUMBAI-400 011
TEL.NO.: 022- 2300 8766, 022-23008761
FAX.NO. : 022-2309 0983
email: design @sjkarchitect.com

This "drawing" is the copyright of **SJK Architects** and shall not be used for any purpose other than that for which it has been loaned.

STRUCTURAL:

MANJUNATH & CO.
CONSULTING ENGINEERS
#236 5th CROSS,
K.G. NAGAR,
BANGALORE - 560019
TEL.NO.: 080- 26616610
email:
manjaxe2010@gmail.com

MEP:

MEPTEK CONSULTANTS

-2/665, Millennium, Veer Savarkar Marg,
Dadar (W),
Mumbai-400028.
nimish.shah@meptekconsultants.com

PMC:

GENERAL NOTES:

1. All Dimensions Are In MILLIMETERS Unless Otherwise Specified.
2. All Dimensions Specified Are UnFinished Dimensions, Unless Otherwise specified.
3. All structural dimensions shall be referred as per Consultants' drawings.
4. DO NOT SCALE Drawing
5. Any Discrepancies In the Drawings Shall Be Brought To The Notice Of The Architect,Prior to Execution.

SPECIFIC NOTES / LEGEND:

1. All Boxed Dimensions are finished dimensions (i.e. after plaster, dado etc). Remaining are unfinished dimensions.
2. All External surfaces of walls shall have 20mm thk External Sandfaced Plaster.
3. All Internal surfaces of walls shall have 12mm thk Backing Coat of Plaster + POP Punning. (Except toilet walls, which will receive waterproofing and dado finish).

NORTH

REVISION NOTES:

PROJECT:

NAGPUR HOUSE

CLIENT:

JAIN FAMILY

REV NO: R0
DATE OF REVISION:

DRAWING NO: NH-DD-PLN-006-R0

DRAWING TITLE:

FIFTH FLOOR PLAN

DATE OF ISSUE: 11-02-2021

SCALE: 1:75 **SHEET SIZE:** A2

PURPOSE : FOR REFERENCE ONLY