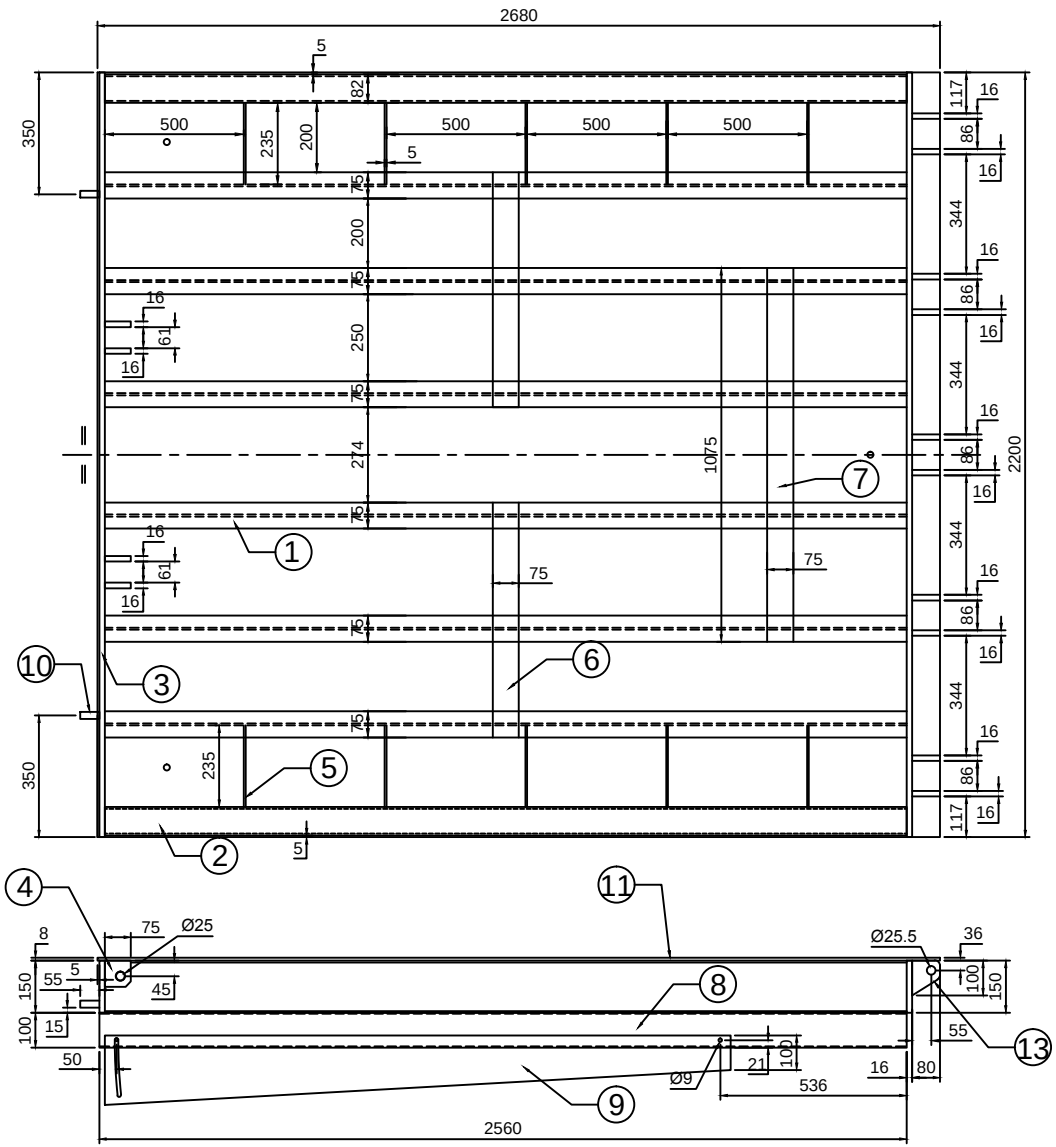


NOTE:~ MTL : MS

PART NO.	PART NAME	DESCRIPTION	QTY
1.	ISMB	150 X 75 X 2560L	6 NOS
2.	R.TUBE	145 X 82 X 5.4THK X 2560L	2 NOS
3.	FLAT	150 X 16 X 2200L	2 NOS
4.	FLAT	75 X 16 X 75L	4 NOS
5.	FLAT	150 X 6 X 235L	10 NOS
6.	FLAT	75 X 6 X 660L	2 NOS
7.	FLAT	75 X 6 X 1060L	1 NO
8.	BEND	100 X 3THK X 2570L	2 NOS
9.	SIDE COVER	200 X 3THK X 1800L	2 NOS
10.	LIP STOPER	Ø20 X 55L	4 NOS
11.	CHEQ.SHEET	2200 X 5 THK X 2680L	1 NO
12.	EYE BOLT	M16 X STD WITH NUT	3 NOS
13.	FLAT	100 X 16 X 80L	10 NOS

This drawing & design is the property of NIHVA TECHNOLOGIES. Not to be sold or copied to any other concern.

TITLE

DECK ASSLY

	NAME	SIGN	DATE
DRAWN	PRADEEP		02.05.2018
CHECK	PRADEEP		02.05.2018
APPRD.	PRADEEP		02.05.2018

If any queries contact : design@nihva.com

ALL DIMENSION ARE IN mm

NIHVA TECHNOLOGIES PVT. LTD.

NIHVA TECHNOLOGIES PVT. LTD. PUNE
Tel : 020 66304033
Email:- info@nihva.com
Website:- www.nihva.com

CLIENT -

PROJECT - NDL 385 & 386

SITE LOCATION -

DWG. NO. : NIHVA/18-19/MFG/NDL385&386/001

SCALE: NTS | WT: | REV- 00