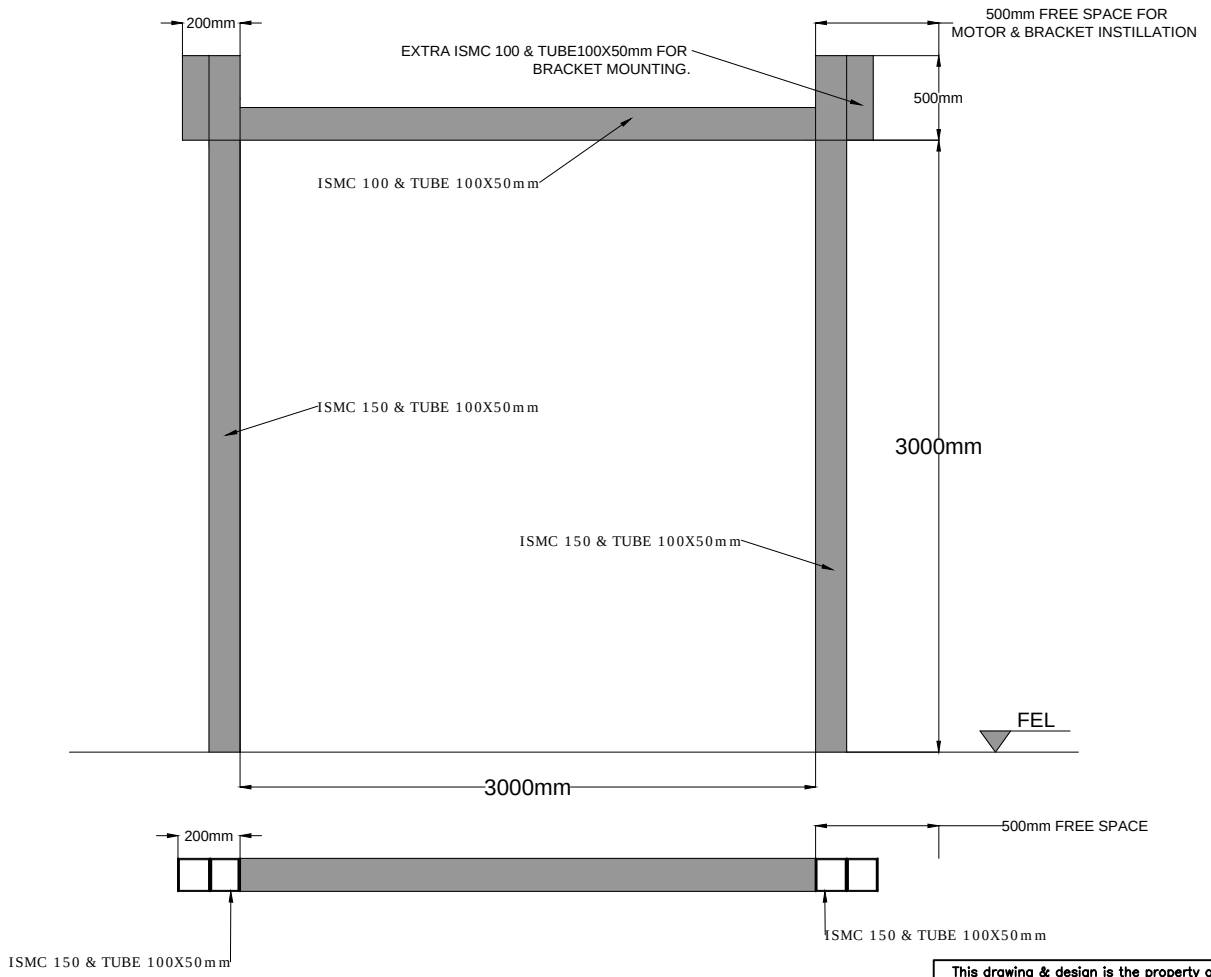


TOLERANCE - ±10mm

CLEAR WIDTH	CLEAR HEIGHT	QTY.
3000mm	3000mm	01NOS

(NOTE: REQUIRED STRUCTURE FOR DOOR SHOULD BE IN CLIENT SCOPE.)

This drawing & design is the property of NIHVA TECHNOLOGIES. Not to be sold or copied to any other concern.

TITLE: STRUCTURE FOR MOTORISED ROLLING SHUTTER

NIHVA TECHNOLOGIES PVT. LTD.
NIHVA TECHNOLOGIES PVT. LTD. PUNE
Tel : 020 66304033
Email:- info@nihva.com
Website:- www.nihva.com

	NAME	SIGN	DATE
DRAWN	SURAJ		21-05-2018
CHECK	PRADEEP		21-05-2018
APPRD.	PRADEEP		21-05-2018

If any queries contact : design@nihva.com

ALL DIMENSION ARE IN mm

CLIENT - GBRN

PROJECT - CNH

SITE LOCATION - CHAKAN

DWG. NO. : NIHVA/18-19/0040 | REV- 0

SCALE: NTS | WT: | SHEET: 01 OF 01