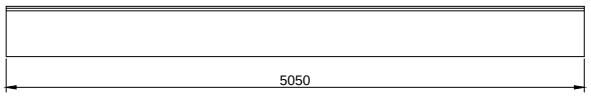

Slat profile- FLAT type.
Material- GI
Thickness - 1mm
Length of slats - 5050mm
Total no of slat - 80

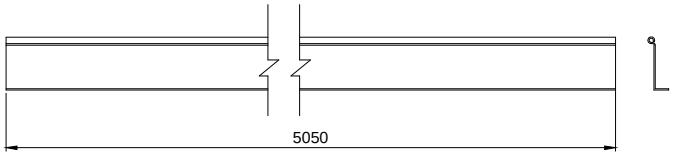

Material- MS
Thickness - 2.5mm
Length of bottom profile - 5050mm
Quantity- 1 Nos.

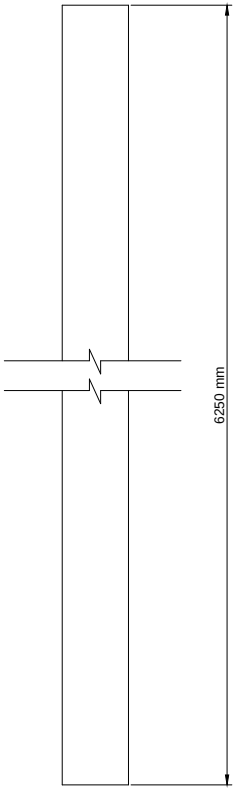

Material- MS
Thickness - 3mm
Length of guide - 6250mm
Quantity- 2 Nos.

This drawing & design is the property of NIHVA TECHNOLOGIES. Not to be sold or copied to any other concern.

TITLE
SLAT GUIDE & BOTTOM

NIHVA TECHNOLOGIES PVT. LTD.
NIHVA TECHNOLOGIES PVT. LTD. PUNE
Tel : 020 66304033
Email:- info@nihva.com
Website:- www.nihva.com

	SIGN	DATE
DRAWN	OMKAR	06/04/17
CHECK	SAGAR P.	06/04/17
REV.		
APPROVAL		

CLIENT -
PROJECT -
SITE -
DWG. NO. : NIHVA/17-18/VDR/001/R01
If any queries contact : projects@nihva.com
SCALE: NTS | WT: | SHEET: 01 OF 01
ALL DIMENSION ARE IN mm