


DETAIL VIEW OF 'B'

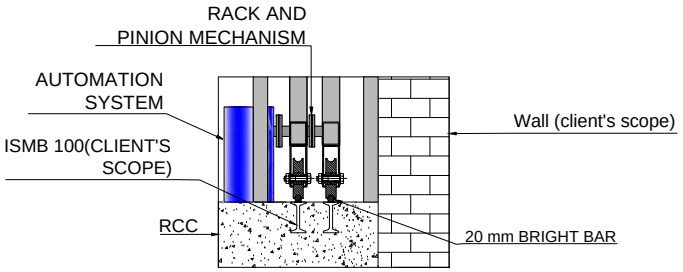

DETAIL VIEW OF 'A'

NOTE:-
1. ALL REQUIRED CIVIL WORK BE IN CLIENTS SCOPE.
2. ONE COAT OF RED OXIDE & TWO COAT OF APPROVED RAL SHADE WILL BE GIVEN TO THE GATE.
3. IF NECESSARY GATE LEAF WILL BE IN TWO PARTS FOR TRANSPORTATION & WILL BE WELD TOGETHER ON SITE.

CLEAR WIDTH	CLEAR HEIGHT	QUANTITY.
35000mm	1800mm	01 NOS

This drawing & designing is the property of NIHVA TECHNOLOGIES. Not to be sold or copied to any other concern.

TITLE: AUTOMATIC DOUBLE LEAF TELESCOPIC GATE

NIHVA TECHNOLOGIES PVT. LTD. PUNE
Tel : 020 66304033
Email:- info@nihva.com
Website:- www.nihva.com

		SIGN	DATE
DRAWN	SURAJ		06-10-18
CHECK	PRADEEP		06-10-18
APPROVAL	R.D		06-10-18

CLIENT -INDAMAR
PROJECT -
SITE -NAGPUR
If any queries contact :design@nihva.com
DWG. NO. : NIHVA/18-19/0140 REV.- 0
ALL DIMENSION ARE IN mm
SCALE: NTS WT: SHEET: 01 OF 01