


ELEVATION - 01

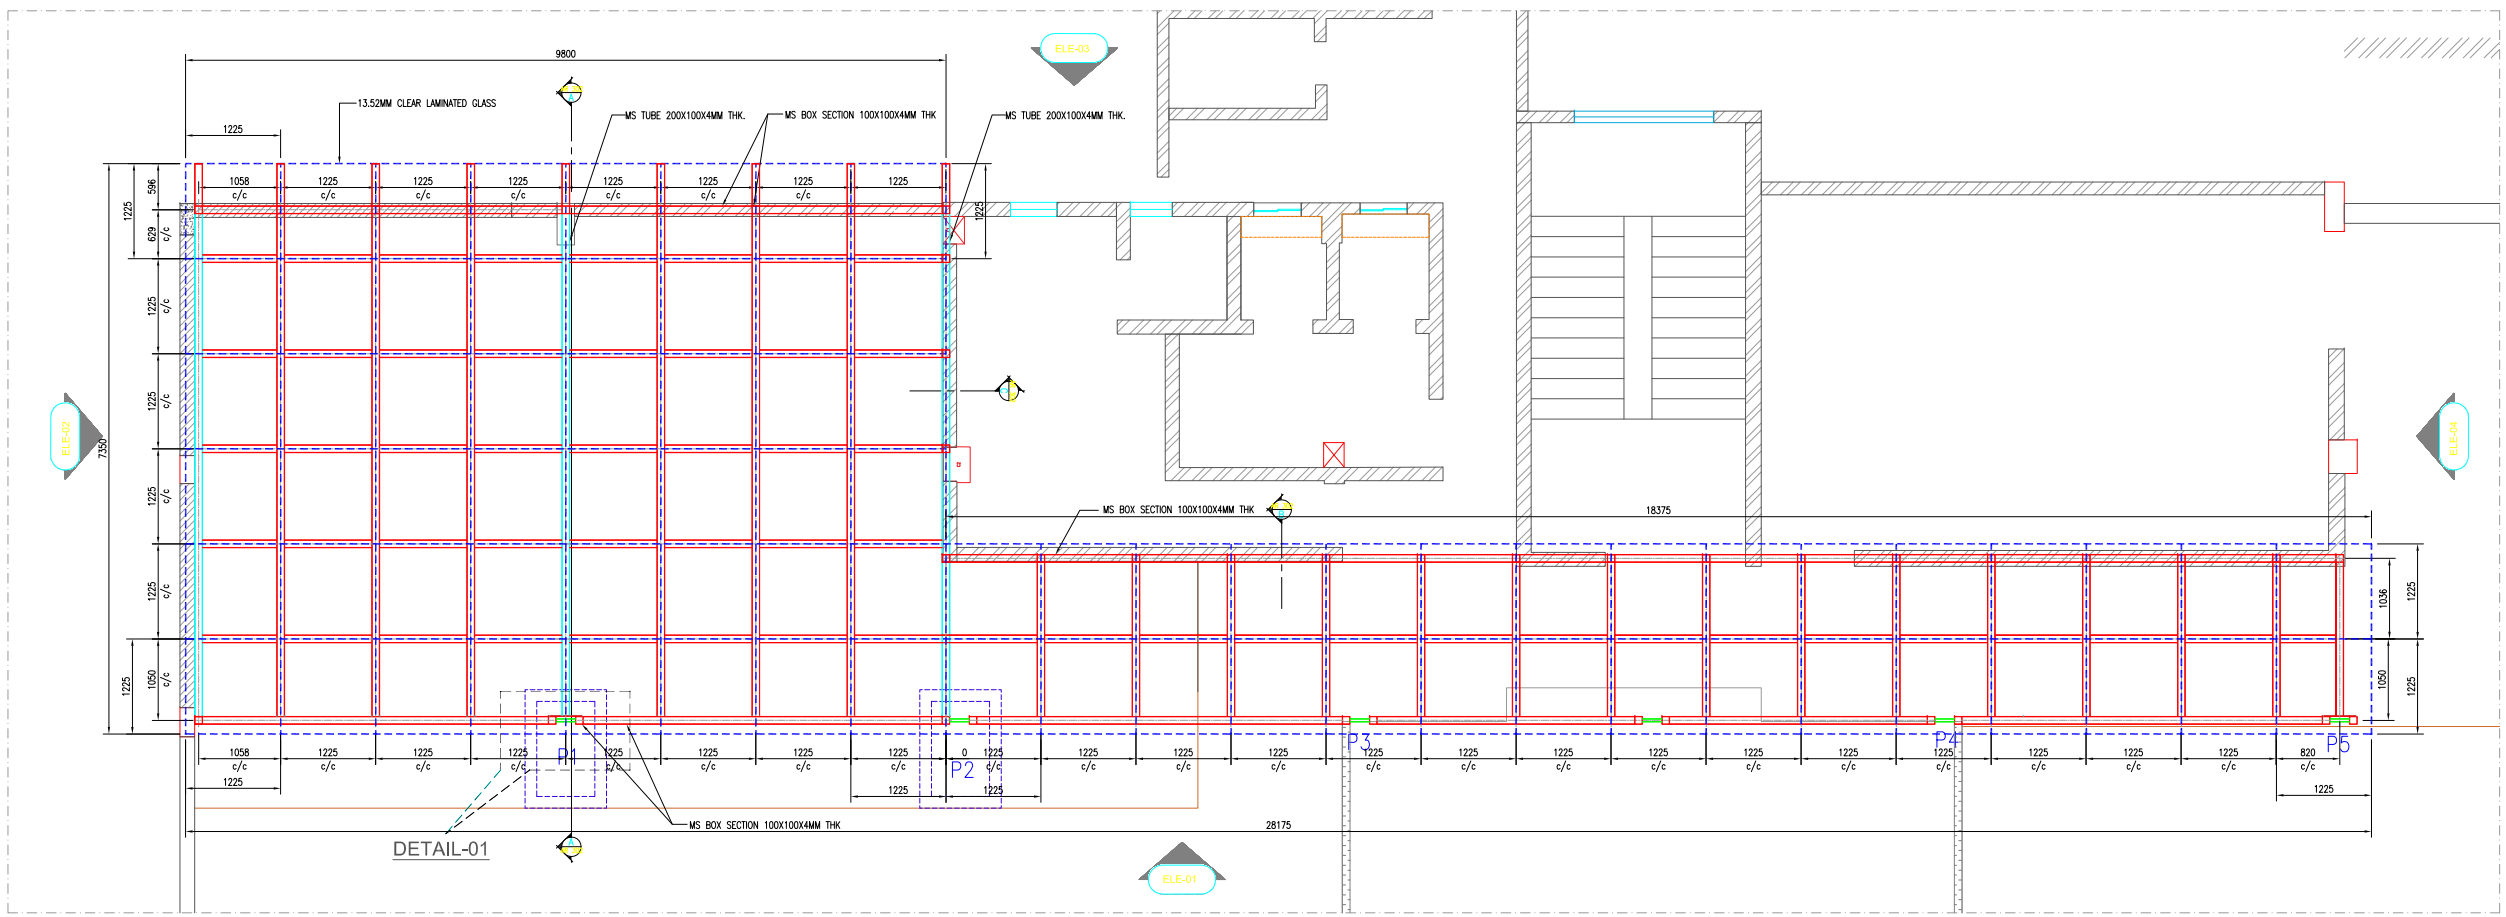

TOP GLASS CANOPY PLAN

GENERAL NOTES :
1. ALL DIMENSIONS ARE IN MM.
2. DO NOT SCALE FROM THIS DRAWING.
3. ALL DIMENSIONS TO BE VERIFIED ON SITE.
4. THIS DRAWING IS TO BE READ IN CONJUNCTION WITH RELEVANT ARCHITECTURAL DETAILS, M & E DRAWINGS AND SPECIFICATIONS. CONTRACTOR SHALL CO-ORDINATE THESE DRAWINGS AND REPORT ANY DISCREPANCY FOR CLARIFICATION BEFORE PROCEEDING WITH WORKS.
5. ALL MATERIALS TO BE APPROVED BY ARCHITECT/ENGINEER.
6. CONTRACTOR SHOULD SUBMIT SHOP DRAWING FOR APPROVAL.
7. CONTRACTOR WILL BE RESPONSIBLE FOR THE CHECKING AND VERIFICATION OF ALL DIMENSIONS, SIZES AND TOLERANCES NEEDED FOR THE INSTALLATIONS OF ALL EQUIPMENT AND FITTINGS THOSE THAT ARE WITHIN THE SCOPE OF THE WORK OF THE CONTRACT AS WELL AS THOSE TO BE SUPPLIED BY OTHERS THEREFORE ALL DIMENSIONS SHOWN ON DRAWINGS RELEVANT TO THESE INSTALLATION ARE FOR
8. BASIC REFERENCE CODE: IS:456-2000
9. CONCRETE MIX IS M20 UNLESS STATED OTHERWISE.
10.CLEAR COVER TO MAIN REINFORCEMENT :- FOOTING:-50mm, COLUMNS:-40mm, SLABS:-20mm, BEAMS:-25mm
11.ALL REINFORCEMENT SHOWN T TO BE T.M.T. BARS OF GRADE Fe.500, @ INDICATES MILD STEEL.
12.LAPS FOR MAIN REINFORCEMENT :- COLUMNS - BAR, BEAMS & SLABS BAR
13.BEARING CAPACITY TO BE ASCERTAINED BEFORE CONCRETING BY THE CONTRACTOR.
14.THE RESPONSIBILITY OF THE DESIGNER SEIZES IF THE DISTRIBUTION OF THE REINFORCEMENT IS NOT GOT CHECKED PRIOR TO CONCRETING.
15.THE DESIGNER'S RESPONSIBILITY LIMITED TO THE DRG. & DESIGN ONLY & NOT FOR EXECUTION.
16.STABILITY OF CONCRETING WORK IS NOT DESIGNER'S RESPONSIBILITY.
17. ALL STRUCTURE MEMBER USED AS PER ISI STANDARD
18. TWO COAT ENAMEL PAINT OF BURGER OR EQUIVALENT OR MARKET AVAILABLY.
19. STANDARD MAKE OF GYPSUM FALSE CEILING
20. AT THE TIME OF EXECUTION SOME CHANGES WILL HAPPEN AS PER DESIGN
21. WE WILL MAKE FINAL DRAWING BEFORE EXECUTION.

DATE	NO.	DESCRIPTION	DRN BY	CHK BY	APP BY

REVISIONS:

CLIENT:

PROJECT:

ROOF TOP RESTAURANT

TITLE:


GLASS ROOF DETAILS
SOLAR PANEL SHED

DRAWING NO.: AHE-HE-21-22-01


SCALE:	AS SHOWS	DATE:	12.09.2022
DRN BY:	SACHIN	CHK BY:	PRAKASH
APP BY:	S. BHUTKAR	ORIGIN:	PUNE
ACAD REF:	--		

ISSUED-FOR-APPROVAL

HERAMB ENTERPRISES
STRUCTURAL CONSULTANT
REGISTERED OFFICE:
KATRAJ KONDHAWA ROAD,
KATRAJ PUNE- 411046
MAHARASHTRA, INDIA
Email : prakashvw@in.com

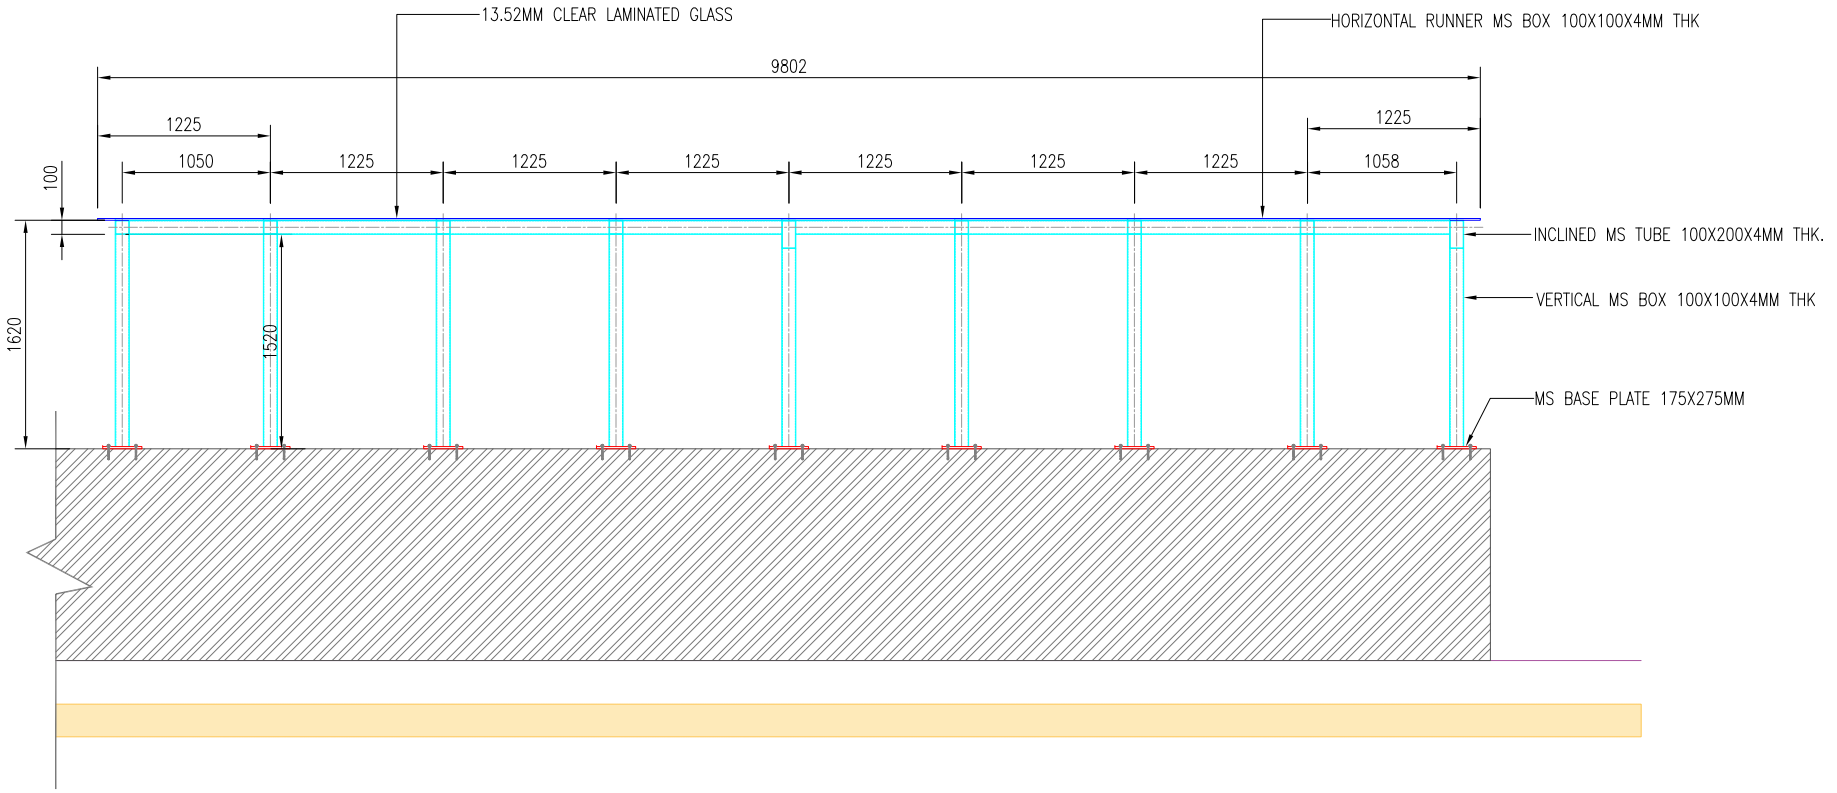


ELEVATION - 03

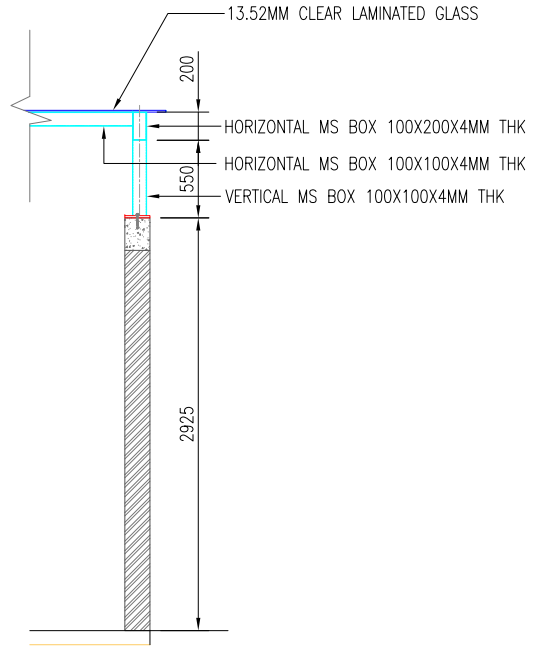


SECTION C-C

DETAIL-02

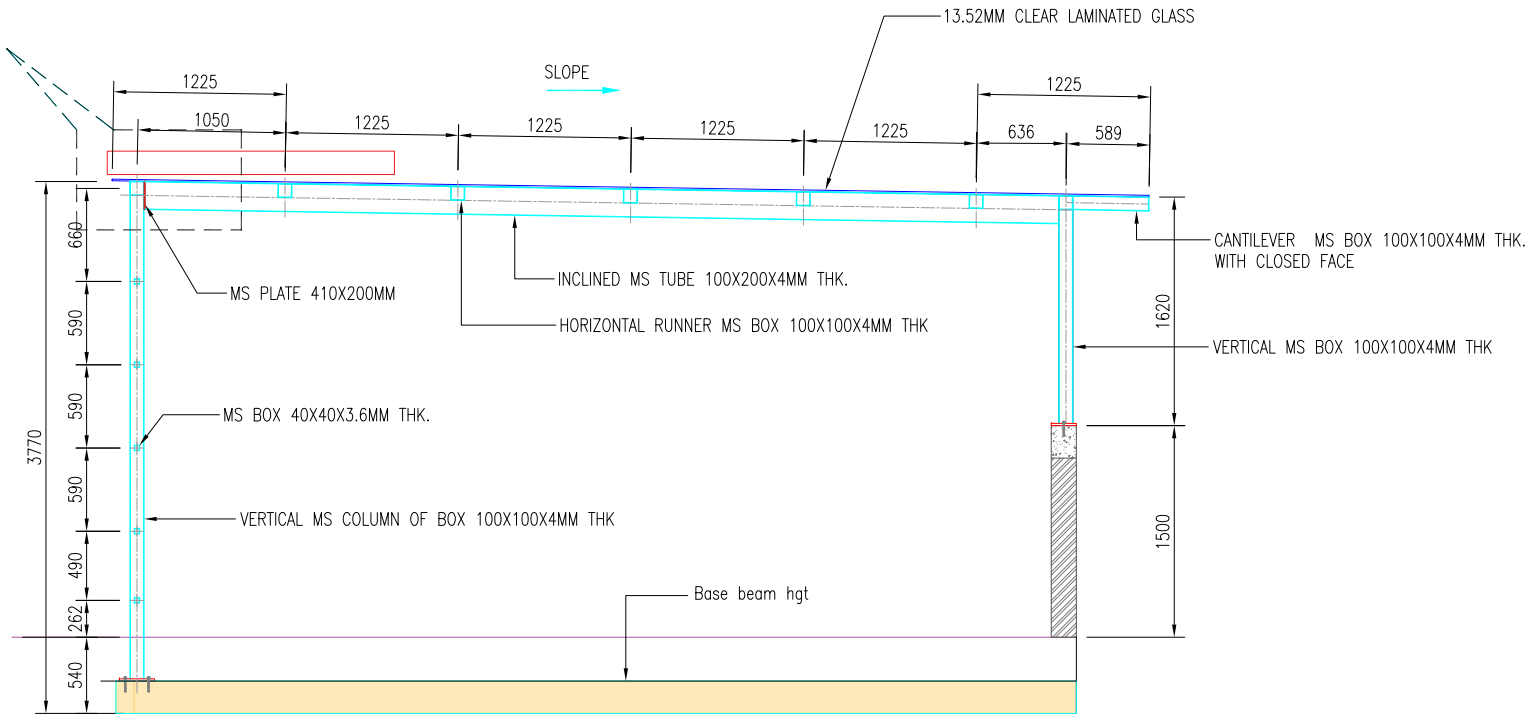

SECTION A-A

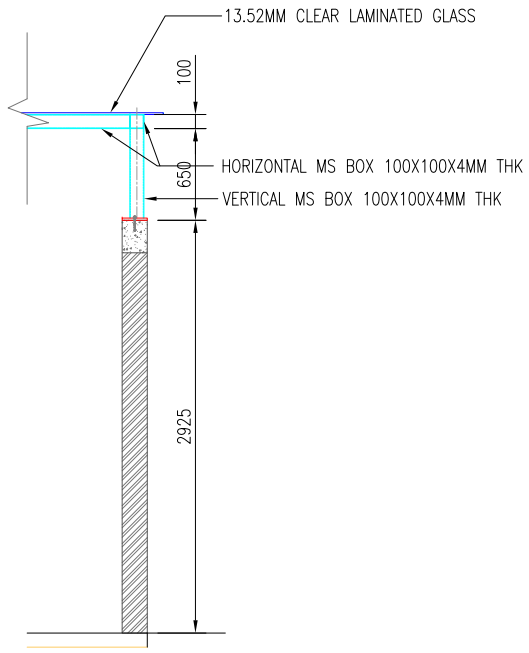

SECTION B-B

GENERAL NOTES :

1. ALL DIMENSIONS ARE IN MM.
2. DO NOT SCALE FROM THIS DRAWING.
3. ALL DIMENSIONS TO BE VERIFIED ON SITE.
4. THIS DRAWING IS TO BE READ IN CONJUNCTION WITH RELEVANT ARCHITECTURAL DETAILS, M & E DRAWINGS AND SPECIFICATIONS. CONTRACTOR SHALL CO-ORDINATE THESE DRAWINGS AND REPORT ANY DISCREPANCY FOR CLARIFICATION BEFORE PROCEEDING WITH WORKS.
5. ALL MATERIALS TO BE APPROVED BY ARCHITECT/ENGINEER.
6. CONTRACTOR SHOULD SUBMIT SHOP DRAWING FOR APPROVAL.
7. CONTRACTOR WILL BE RESPONSIBLE FOR THE CHECKING AND VERIFICATION OF ALL DIMENSIONS, SIZES AND TOLERANCES NEEDED FOR THE INSTALLATIONS OF ALL EQUIPMENT AND FITTINGS THOSE THAT ARE WITHIN THE SCOPE OF THE WORK OF THE CONTRACT AS WELL AS THOSE TO BE SUPPLIED BY OTHERS THEREFORE ALL DIMENSIONS SHOWN ON DRAWINGS RELEVANT TO THESE INSTALLATION ARE FOR
8. BASIC REFERENCE CODE: IS:456-2000
9. CONCRETE MIX IS M20 UNLESS STATED OTHERWISE.
10. CLEAR COVER TO MAIN REINFORCEMENT :- FOOTING:-50mm, COLUMNS:-40mm, SLABS:-20mm, BEAMS:-25mm
11. ALL REINFORCEMENT SHOWN T TO BE T.M.T. BARS OF GRADE Fe.500, @ INDICATES MILD STEEL.
12. LAPS FOR MAIN REINFORCEMENT :- COLUMNS - BAR, BEAMS & SLABS BAR
13. BEARING CAPACITY TO BE ASCERTAINED BEFORE CONCRETING BY THE CONTRACTOR.
14. THE RESPONSIBILITY OF THE DESIGNER SEIZES IF THE DISTRIBUTION OF THE REINFORCEMENT IS NOT GOT CHECKED PRIOR TO CONCRETING.
15. THE DESIGNER'S RESPONSIBILITY LIMITED TO THE DRG. & DESIGN ONLY & NOT FOR EXECUTION.
16. STABILITY OF CONCRETING WORK IS NOT DESIGNER'S RESPONSIBILITY.
17. ALL STRUCTURE MEMBER USED AS PER ISI STANDARD
18. TWO COAT ENAMEL PAINT OF BURGER OR EQUIVALENT OR MARKET AVAILABLY.
19. STANDARD MAKE OF GYPSUM FALSE CEILING
20. AT THE TIME OF EXECUTION SOME CHANGES WILL HAPPEN AS PER DESIGN
21. WE WILL MAKE FINAL DRAWING BEFORE EXECUTION.

DATE	NO.	DESCRIPTION	DRN BY	CHK BY	APP BY
REVISIONS:					

CLIENT:

PROJECT:

ROOF TOP RESTAURANT

TITLE:


GLASS ROOF DETAILS
SOLAR PANEL SHED

DRAWING NO.: AHE-HE-21-22-01


SCALE:	AS SHOWS	DATE:	12.09.2022
DRN BY:	SACHIN	CHK BY:	PRAKASH
APP BY:	S. BHUTKAR	ORIGIN:	PUNE
ACAD REF:	--		

ISSUED-FOR-APPROVAL


HERAMB ENTERPRISES
STRUCTURAL CONSULTANT
REGISTERED OFFICE:
KATRAJ KONDHAWA ROAD,
KATRAJ PUNE- 411046
MAHARASHTRA, INDIA
Email : prakashvw@in.com

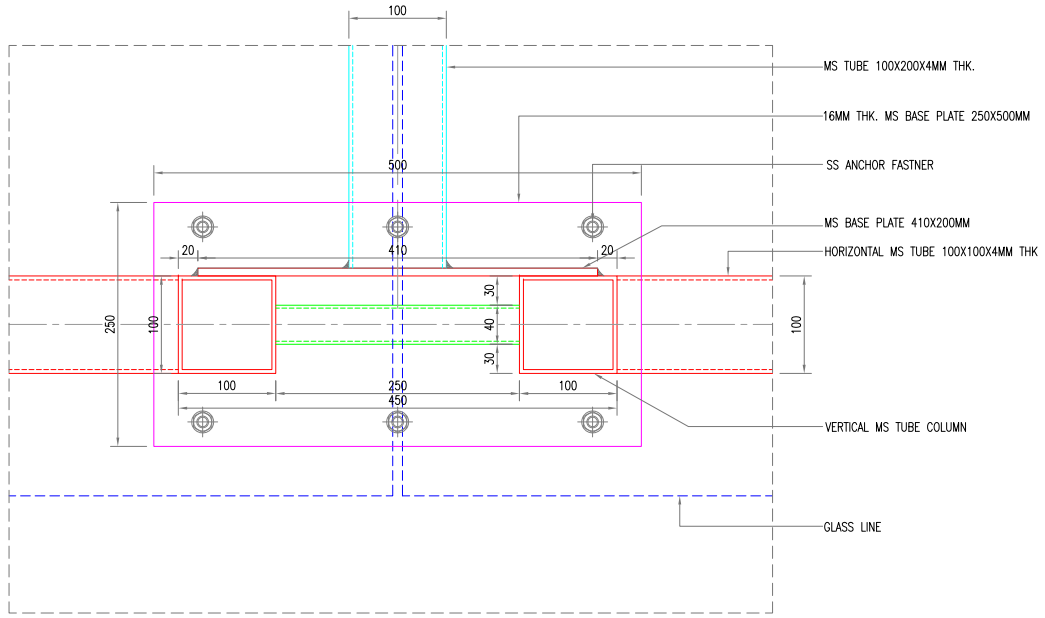

COLUMN PLAN DETAIL
DETAIL-1

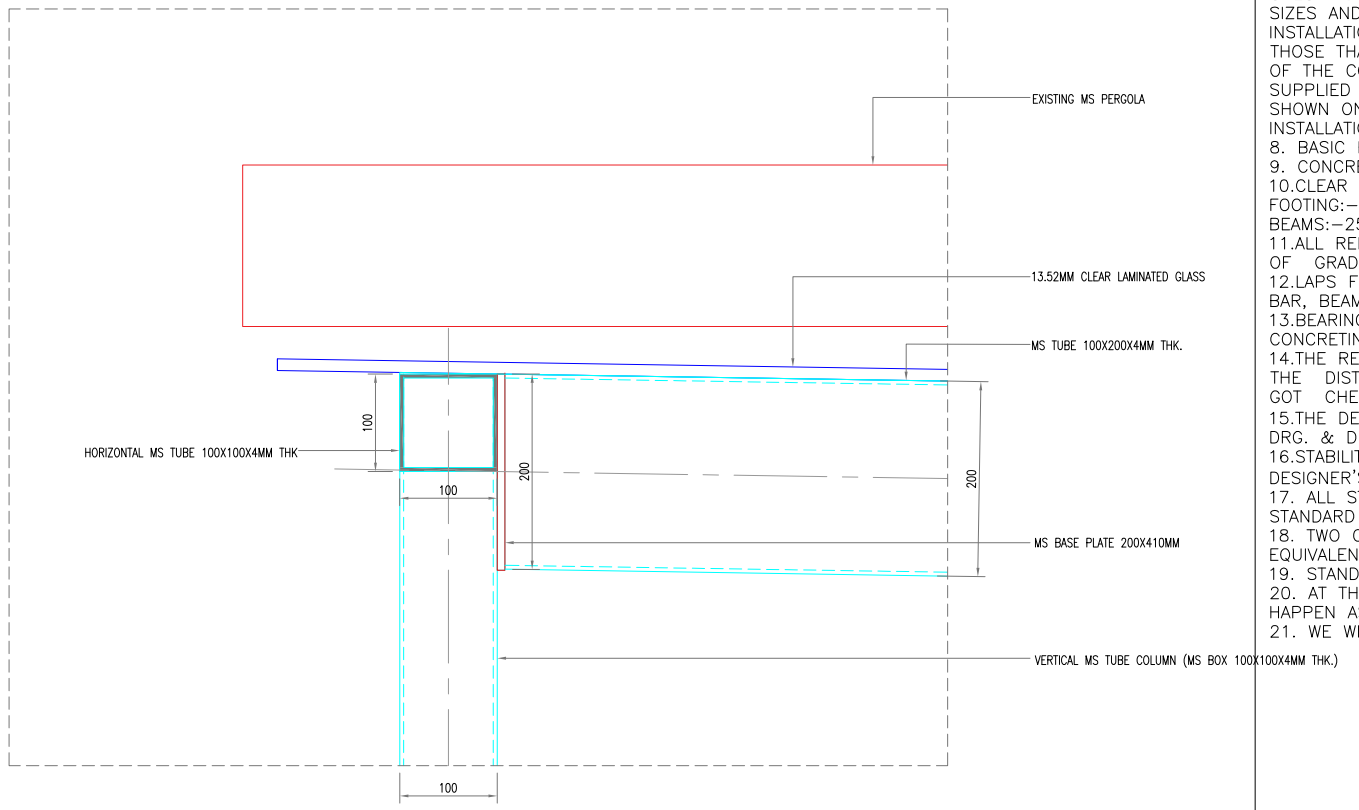

COLUMN SECTIONAL DETAIL
DETAIL- 2

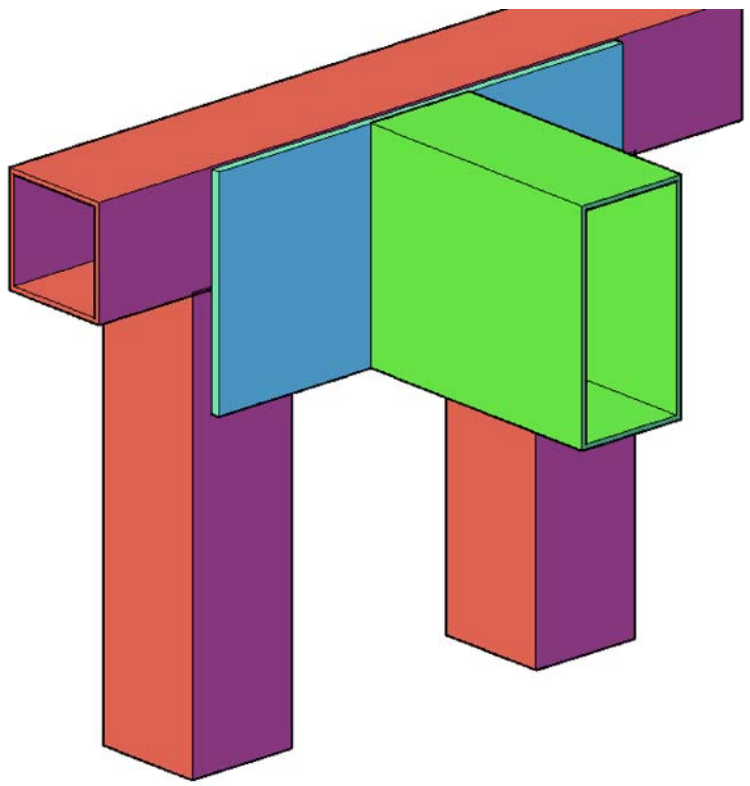

3D VIEW

GENERAL NOTES :
1. ALL DIMENSIONS ARE IN MM.
2. DO NOT SCALE FROM THIS DRAWING.
3. ALL DIMENSIONS TO BE VERIFIED ON SITE.
4. THIS DRAWING IS TO BE READ IN CONJUNCTION WITH RELEVANT ARCHITECTURAL DETAILS, M & E DRAWINGS AND SPECIFICATIONS. CONTRACTOR SHALL CO-ORDINATE THESE DRAWINGS AND REPORT ANY DISCREPANCY FOR CLARIFICATION BEFORE PROCEEDING WITH WORKS.
5. ALL MATERIALS TO BE APPROVED BY ARCHITECT/ENGINEER.
6. CONTRACTOR SHOULD SUBMIT SHOP DRAWING FOR APPROVAL.
7. CONTRACTOR WILL BE RESPONSIBLE FOR THE CHECKING AND VERIFICATION OF ALL DIMENSIONS, SIZES AND TOLERANCES NEEDED FOR THE INSTALLATIONS OF ALL EQUIPMENT AND FITTINGS THOSE THAT ARE WITHIN THE SCOPE OF THE WORK OF THE CONTRACT AS WELL AS THOSE TO BE SUPPLIED BY OTHERS THEREFORE ALL DIMENSIONS SHOWN ON DRAWINGS RELEVANT TO THESE INSTALLATION ARE FOR
8. BASIC REFERENCE CODE: IS:456-2000
9. CONCRETE MIX IS M20 UNLESS STATED OTHERWISE.
10.CLEAR COVER TO MAIN REINFORCEMENT :- FOOTING:-50mm, COLUMNS:-40mm, SLABS:-20mm, BEAMS:-25mm
11.ALL REINFORCEMENT SHOWN T TO BE T.M.T. BARS OF GRADE Fe.500, @ INDICATES MILD STEEL.
12.LAPS FOR MAIN REINFORCEMENT :- COLUMNS - BAR, BEAMS & SLABS BAR
13.BEARING CAPACITY TO BE ASCERTAINED BEFORE CONCRETING BY THE CONTRACTOR.
14.THE RESPONSIBILITY OF THE DESIGNER SEIZES IF THE DISTRIBUTION OF THE REINFORCEMENT IS NOT GOT CHECKED PRIOR TO CONCRETING.
15.THE DESIGNER'S RESPONSIBILITY LIMITED TO THE DRG. & DESIGN ONLY & NOT FOR EXECUTION.
16.STABILITY OF CONCRETING WORK IS NOT DESIGNER'S RESPONSIBILITY.
17. ALL STRUCTURE MEMBER USED AS PER ISI STANDARD
18. TWO COAT ENAMEL PAINT OF BURGER OR EQUIVALENT OR MARKET AVAILABLY.
19. STANDARD MAKE OF GYPSUM FALSE CEILING
20. AT THE TIME OF EXECUTION SOME CHANGES WILL HAPPEN AS PER DESIGN
21. WE WILL MAKE FINAL DRAWING BEFORE EXECUTION.

DATE	NO.	DESCRIPTION	DRN BY	CHK BY	APP BY

REVISIONS:

CLIENT:

PROJECT:
ROOF TOP RESTAURANT

TITLE:
GLASS ROOF DETAILS
SOLAR PANEL SHED

DRAWING NO.: AHE-HE-21-22-01

SCALE:	AS SHOWS	DATE:	12.09.2022
DRN BY:	SACHIN	CHK BY:	PRAKASH
APP BY:	S. BHUTKAR	ORIGIN:	PUNE
ACAD REF:	--		

ISSUED-FOR-APPROVAL

HERAMB ENTERPRISES
STRUCTURAL CONSULTANT
REGISTERED OFFICE:
KATRAJ KONDHAWA ROAD,
KATRAJ PUNE- 411046
MAHARASHTRA, INDIA
Email : prakashvw@in.com