


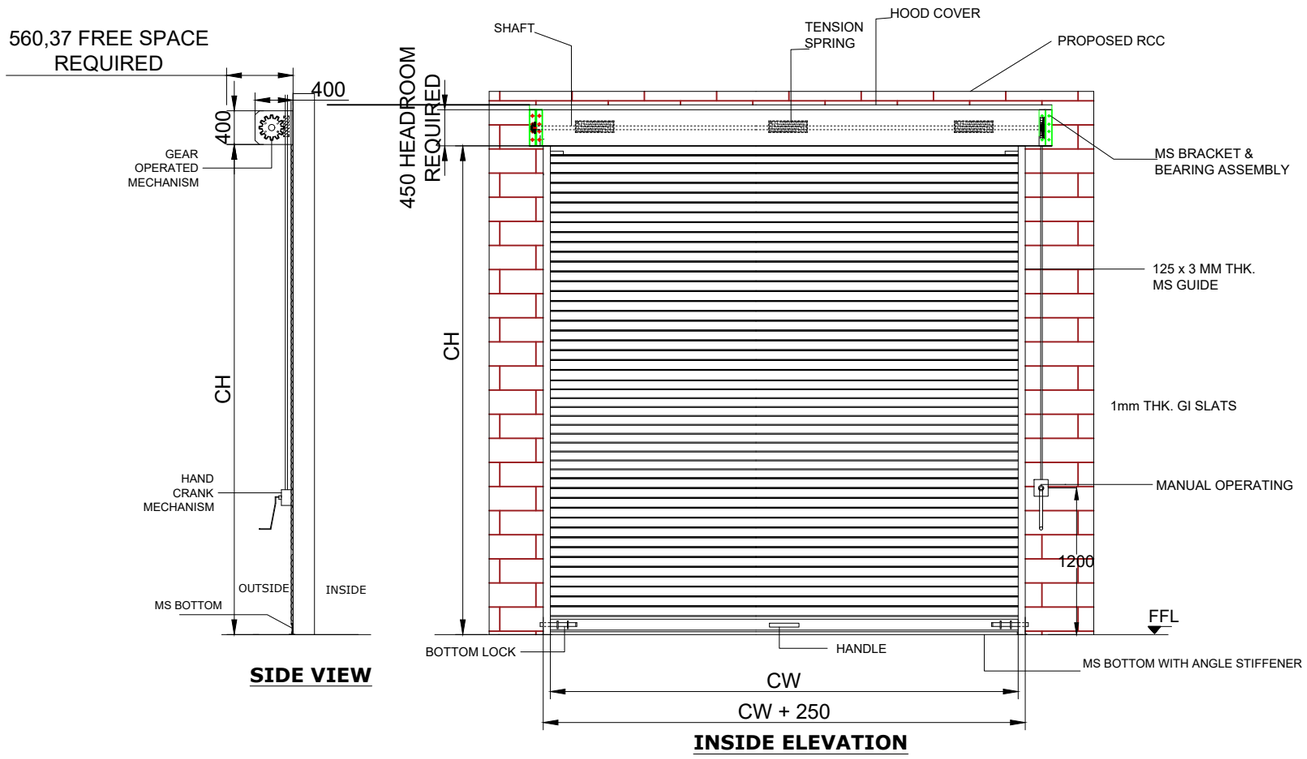


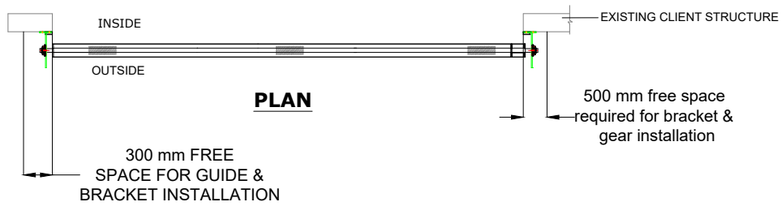

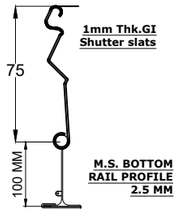

M.S. BOTTOM RAIL PROFILE 2.5MM

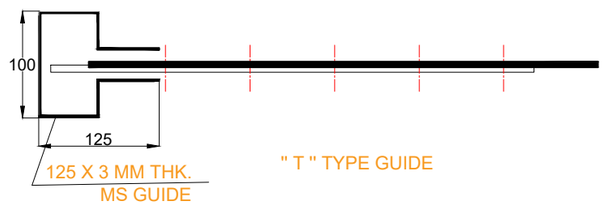

NOTE-
1. ALL CIVIL WORK WILL BE CLIENT'S SCOPE.
2.IF STRUCTURE REQUIRED FOR SHUTTER IS IN CLIENT'S SCOPE.

TECHNICAL SPECIFICATION:-

SR.	SPECIFICATION	DETAILS
1.	DESCRIPTION & DRIVE	GEAR OPERATED SHUTTER
2.	LOCATION AREA	INSIDE AREA / OUTSIDE AREA
3.	MOUNTING SURFACE	SIDE BRACKETS: ON CONCRETE
4.	SLAT	75 MM WIDE - 1 MM THICK GI
5.	BOTTOM PROFILE	M.S. PLATE 100X2.5 MM THICK WITH ANGLE STIFFNER
6.	GUIDE PROFILE	M.S."T" SHAPE -100X125X3 MM THK .
7.	HOOD COVER	MADE OF GI SHEET THICKNESS 0.9 MM.
8.	MATERIAL FINISH	SYNTHETIC ENAMEL PAINT

SR NO	(CW) CLEAR WIDTH	(CH) CLEAR HEIGHT	QUANTITY
1	3000	4000	04 NOS

This drawing & design is the property of NIHVA TECHNOLOGIES. Not to be sold or copied to any other concern.

	NAME	SIGN	DATE
DRAWN	V.W.		08.11.2025
CHECK	B.S.		08.11.2025
APPRD.	V.T.		08.11.2025

TITLE: GEAR OPERATED ROLLING SHUTTER

NIHVA TECHNOLOGIES PVT. LTD.
NIHVA TECHNOLOGIES PVT. LTD. PUNE
Tel : 020 66304033
Website:- www.nihva.com
Email:- info@nihva.com

CLIENT - ARCESGES BUILDING INDIA LLP

PROJECT -

SITE LOCATION -

If any queries contact : design@nihva.com

DWG. NO. : NIHVA/21-22/VDR/020

REV- R00

ALL DIMENSION ARE IN mm

SCALE: NTS

WT:

SHEET: 01 OF 01