
Steel sections by WPI

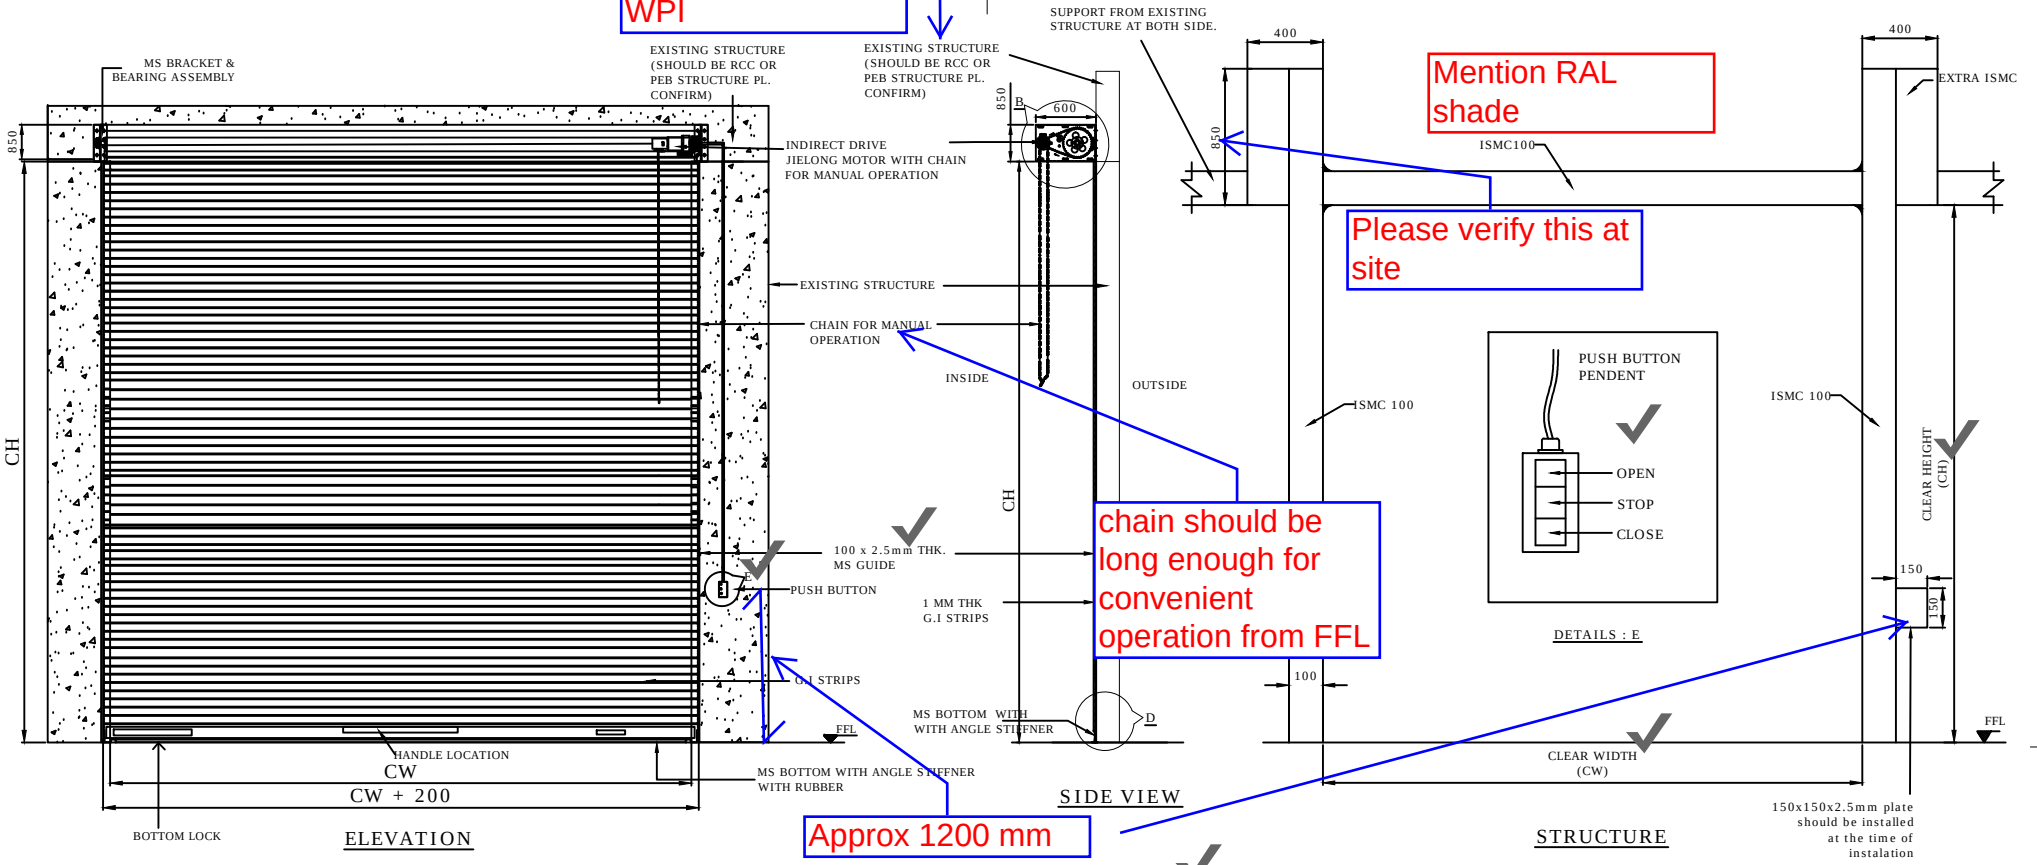



Mention RAL shade

Please verify this at site


chain should be long enough for convenient operation from FFL

Approx 1200 mm

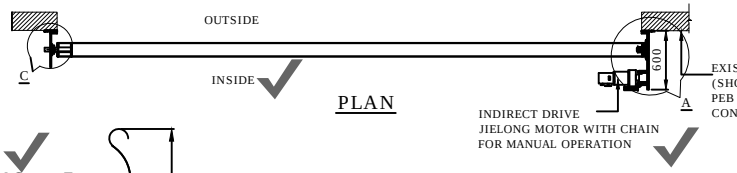


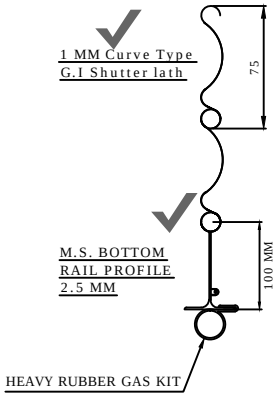

DETAILS : D

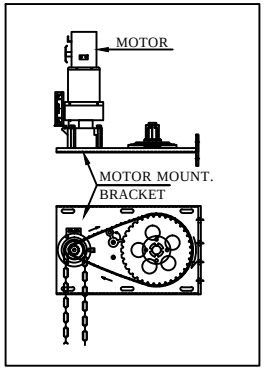

DETAILS : A & B

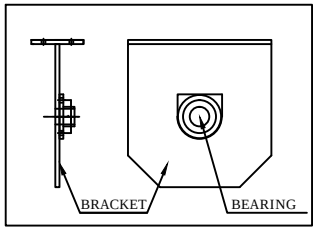

DETAILS : C

(NOTE: REQUIRED TECHANICAL STRUCTURE FOR SHUTTER IN CLIENT SCOPE)

3000	3000	1	RAL -
CLEAR WIDTH (CW)	CLEAR HEIGHT (CH)	QUANTITY	RAL COLOR

This drawing & design is the property of NIHVA TECHNOLOGIES. Not to be sold or copied to any other concern.

TITLE	MOTORIZED ROLLING SHUTTER			NIHVA TECHNOLOGIES PVT. LTD. PUNE Tel : 020 66304033 Email:- info@nihva.com Website:- www.nihva.com
	NAME	SIGN	DATE	
DRAWN	P.A		19.11.2019	CLIENT - WANI
CHECK	G.J		19.11.2019	PROJECT - BRIDGESTONE
APPRD.				SITE LOCATION - CHAKAN
If any queries contact : design@nihva.com				DWG. NO. : NIHVA/19-20/0154 REV- R00
ALL DIMENSION ARE IN mm				SCALE: NTS WT: SHEET: