


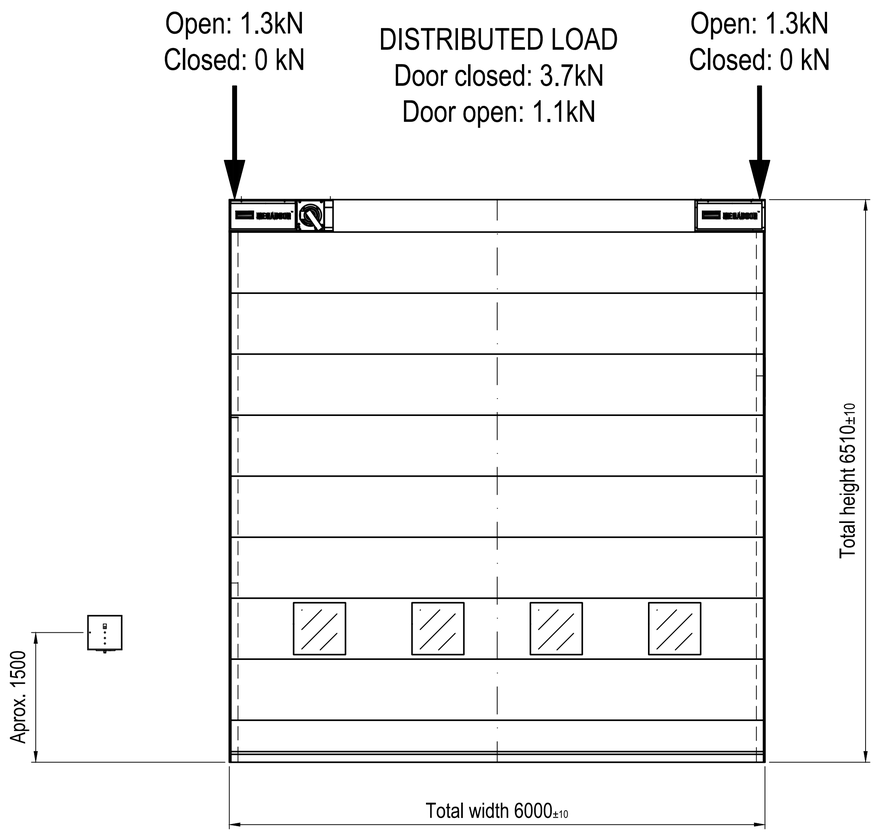


Exterior view, Door closed

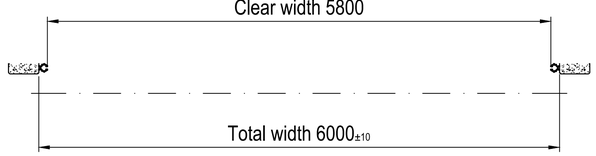

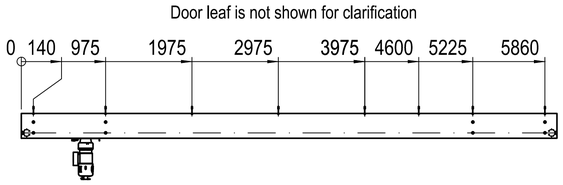

With hole pattern for header box attachment

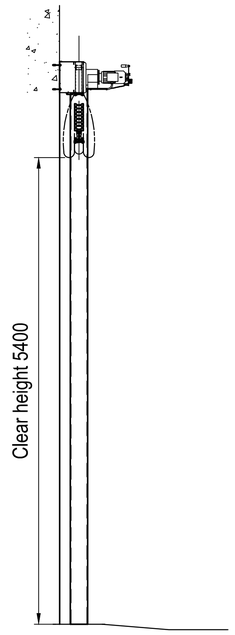

NOT INCLUDED IN DOOR SUPPLY:

1. Design and supply of all door supporting structural components.
2. Design and supply of all closure between door and adjacent steel.
3. Door jambs adjustable for overall door width and true to plumb.
4. Paint job after completed door installation.
5. Any frameworks being provided by ASSA ABLOY will be clearly indicated as "by ASSA ABLOY".

REQUIREMENTS ON BUILDING:

6. Door head support must be straight within 1/600 of span in the in/out direction and free from protrusions of any kind.
7. For a single door leaf, door head support should be horizontal and straight within 1/600 of span at distributed full door load.
8. Door side jambs must be smooth, straight and parallel, out of plumb must not exceed 2mm/m (total deviation at full length 5 mm) in any direction.
9. Any footings at bottom of jamb columns must not interfere with installation of guide rails at floor level.
10. At time of installation, finished floor, free from obstructions, out to a distance of 2 m on each side of door centreline must be available.
11. Header box must be accessible from both sides during installation.


DOOR PROPERTIES:


12. The door is designed to withstand a differential pressure of 1.15kPa x 1.5 FOS.
13. Metal trim: motor side
14. Side profiles
15. Fabric colour: Please specify

ELECTRICAL:


14. One main control panel provided of PLC type.
15. Audible and visual alarm
16. Safety edge
17. Back-up power switch
18. Approx. size of main control panel: WxHxD (500mm x 600mmx250 mm),
19. Power: 1.4kW
20. Nom. current: 3.3A
21. (max. allowed voltage drop at start: 5%)

BELT HOIST UNITS:
Sk 773.1-90S/4 Z dual brake

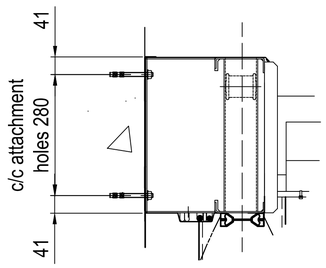

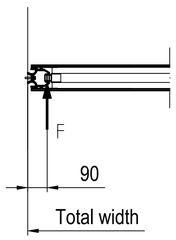

Force by differential pressure transferred to guide rail at each intermediate position.
F= 2.5 kN

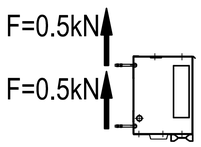

Load on header box attachment (each screw), due to wind load and door weight

DESIGNED KMÖ		SIZE A2	SCALE 1:50
CODE 84690	If not otherwise stated: Tolerances ISO 2768-m EN ISO 13920-B	Delhi Fire Station ARFF4	
ITEM NO		India	
DATE 2021-08-12	Cutting class ISO 9013-442	Megadoor 5800 x 5400	PLOT DATE
ASSA ABLOY	Weld class ISO 5817-C Surface finish Smooth raw surface	Sales Interface	
		DRAWING NO 74148-R01	REVISION --

This document is the property of ASSA ABLOY Entrance Systems AB and shall not without our written permission be copied, imparted to a third party or used for any other unauthorized purpose.