
| REV NO | DATE | DRAWN | REMARK |
|---|---|---|---|
| R01 | 22.06.19 | P.V.A | 1. REVISED AS PER COMMENT |
| R02 | 26.06.19 | P.V.A | 2. REVISED AS PER COMMENT |

| DOCK LEVELER SIZE | WIDTH (W) | LENGTH ( L) | HEIGHT (H) | LIP (C) LENGTH | BUMPER SIZE |
|---|---|---|---|---|---|
| | 2200 | 3000 | 550 | 400 | 250X330X100 |

TO BE CONFIRM FROM CLIENT

| PIT DIMENSION | WIDTH (W 1) | LENGTH ( L 1) | DEPTH (D) | ALL DIMENSIONS ARE IN mm |
|---|---|---|---|---|
| | 2240 | 3000 | 555 | |


TRUNCH FOR SUPPLY CABLE 4" (2" NOT POSSIBLE ) DIA FROM PANEL POSITION (CIVIL WORK WILL BE IN CLIENT SCOPE)
TO THE BOTH SIDE BOTTOM OF PIT.

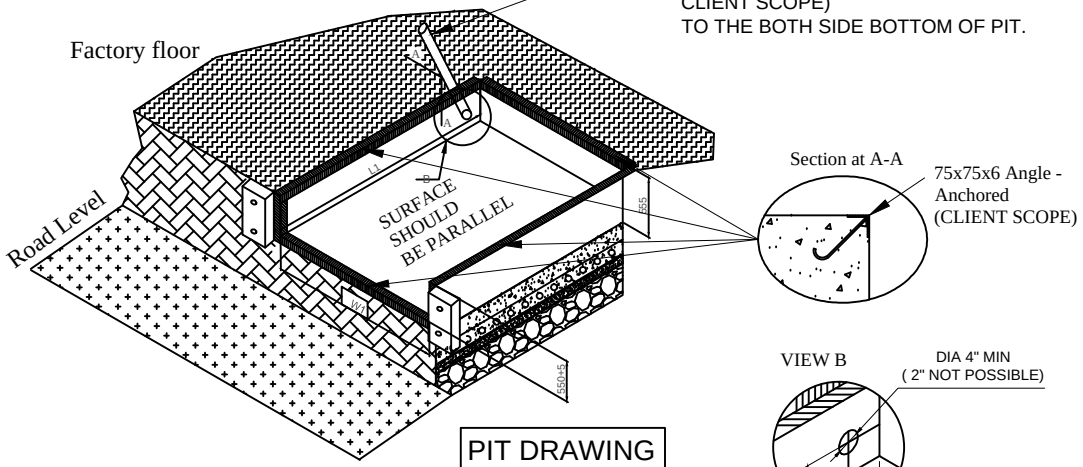


PIT DRAWING





75x75x6 Angle - Anchored (CLIENT SCOPE)

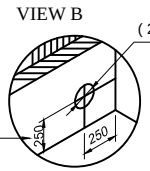



DIA 4" MIN ( 2" NOT POSSIBLE)


75 MM IS NOT POSSIBLE

1. MOC : ALL MATERIAL IS MILD STEEL.
2. CHEQ. SHEET THK : 8 MM.

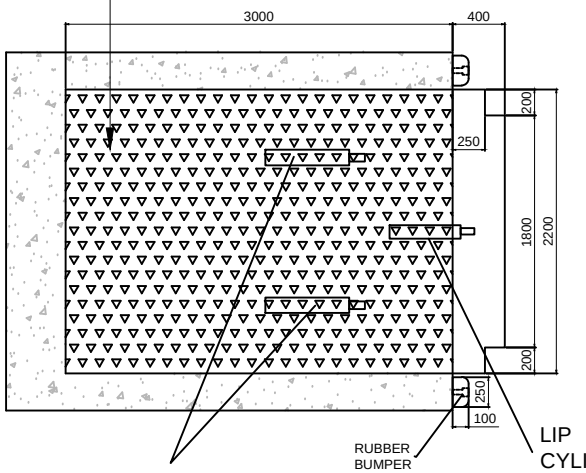

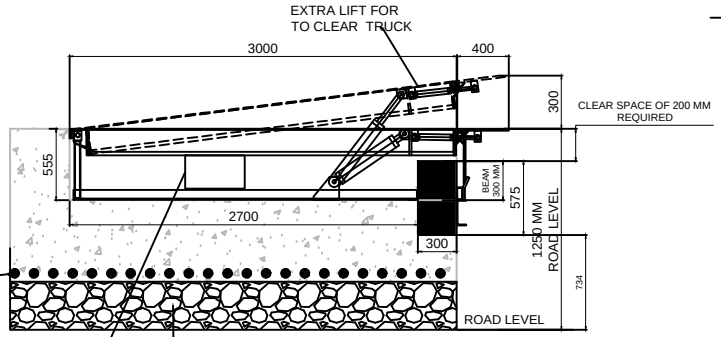
NON FLAME PROOF CONTROL PANEL

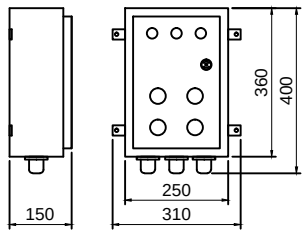


| SR.NO | COLOR RAL CODE | COLOR RAL SHADE | APPROVE |
|---|---|---|---|
| 2 | RAL 5002 | ULTRA MARINE BLUE | |
| 1 | RAL 1004 | GOLDEN YELLOW ( DECK ) BLACK ( BOTTOM SIDE ) | |

TO BE CONFIRM FROM CLIENT

NOTE: -
1. PROPER DRAINAGE SHOULD BE DONE
2. TRENCH AS SHOWN SHOULD BE MADE BY DECIDING THE CONTROL PANEL POSITION.
3. CABLE FROM POWER PACK TO CONTROL PANEL LENGTH IS 7000 MM.(NIHVA SCOPE - EACH DOCK)
4. MAIN SUPPLY CABLE IS IN CLIENT SCOPE. (4 CORE X 2.5 SQ. MM).
5. LEVEL OF THE PIT SHOULD BE PLAIN AND SHOULD TAKE AT LEAST 20000 KGS FLOOR LOAD.
6. FABRICATION TOLERANCE FOR PLATFORM SIZE WILL BE + 10 MM
7. SAFETY FEATURES : DOCK BUMPER IS PROVIDED FOR PROTECT DOCK FROM DIRECT VEHICLE IMPACT.

# DOCK LEVELER- 15 TON CAPACITY - 04 NOS

IMP NOTE: -
1.PLEASE NOTE THAT THE CAPACITY OF DOCK LEVELER CONSIDERED IS THE CAPACITY AFTER THE LIP IS RESTED ON THE VEHICLE.
2.CYLINDERS PROVIDED ARE INTENDENT TO BE USED ONLY FOR LIFTING OF BARE DOCK & CAN NOT LIFT OTHER LOADS.

TOLERANCE :- ± 10mm

CONSULTANT NAME : SPECTRUM PHARMATECH CONSULTANT PVT LTD.

This drawing & design is the property of NIHVA TECHNOLOGIES. Not to be sold or copied to any other concern.

TITLE: DOCK LEVELER

| | NAME | SIGN | DATE |
|---|---|---|---|
| DRAWN | P.V.A | | 12.06.2019 |
| CHECK | V.M.T | | 12.06.2019 |
| APPRD. | | | |

NIHVA TECHNOLOGIES PVT. LTD.
Website:- www.nihva.com
NIHVA TECHNOLOGIES PVT. LTD. PUNE
Tel : 020 66304033
Email:- info@nihva.com

CLIENT -
PROJECT -
SITE LOCATION -
If any queries contact : design@nihva.com
DWG. NO. : NIHVA/19-20/0027/R02
REV- R02
ALL DIMENSION ARE IN mm
SCALE: NTS
WT:
SHEET: 01 OF 01