



DRAWING

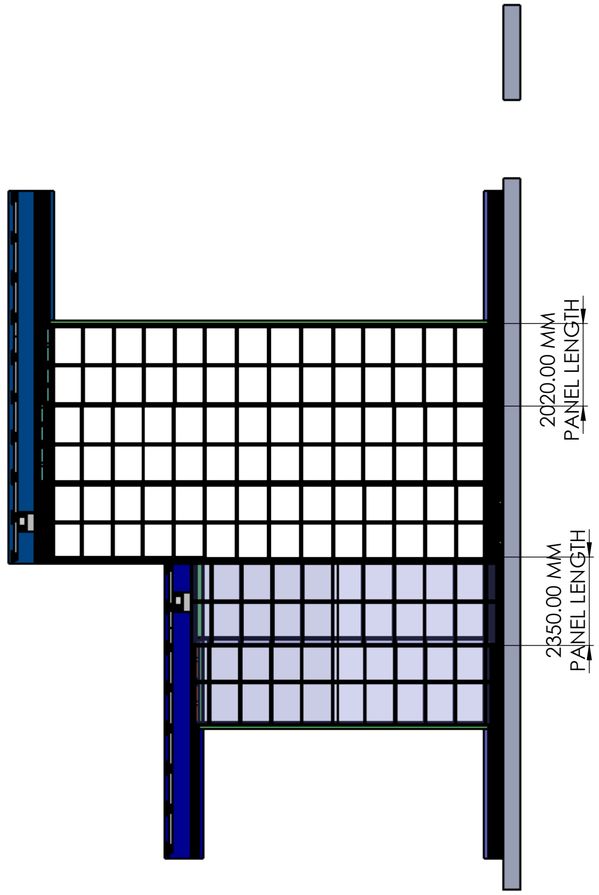


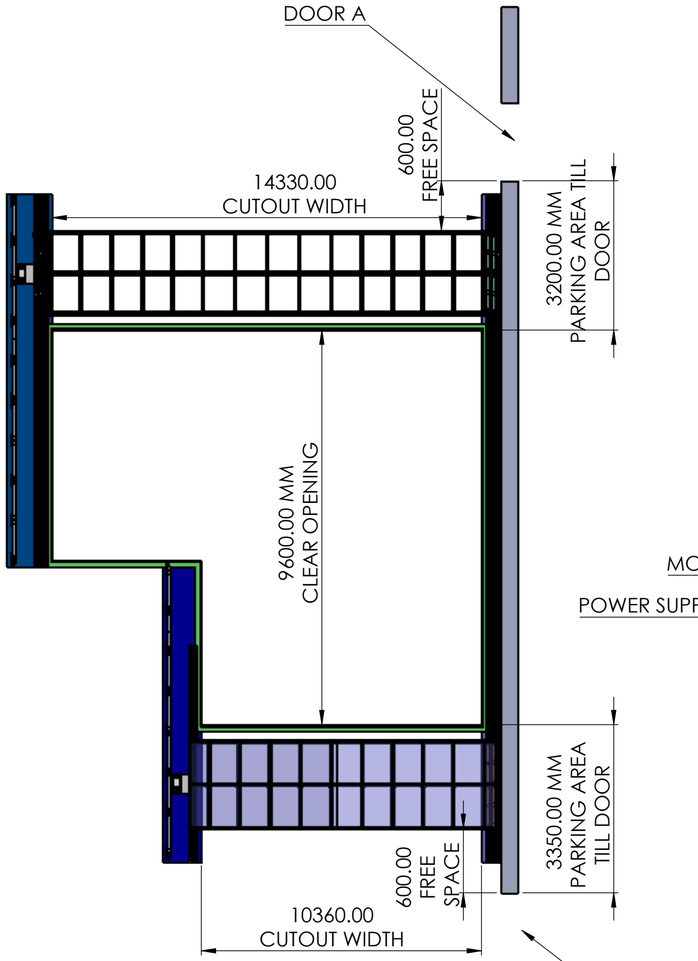

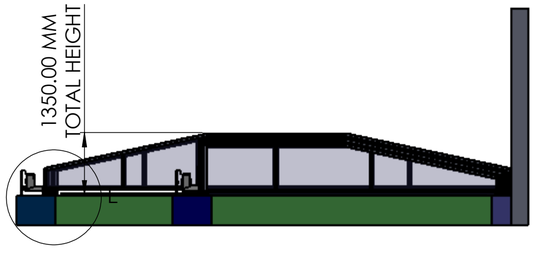


SLIDING DIRECTION

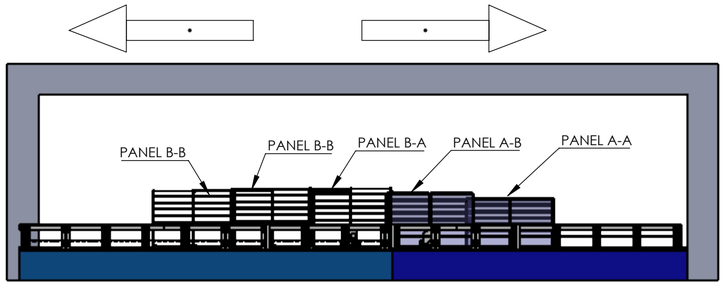


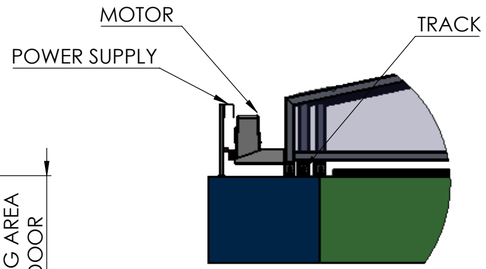

DETAIL E
SCALE 1 : 35

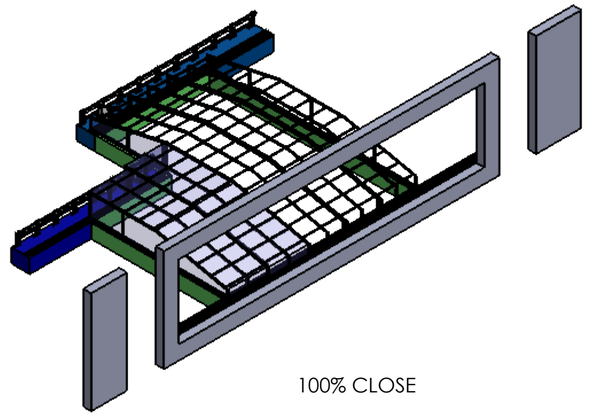

100% CLOSE

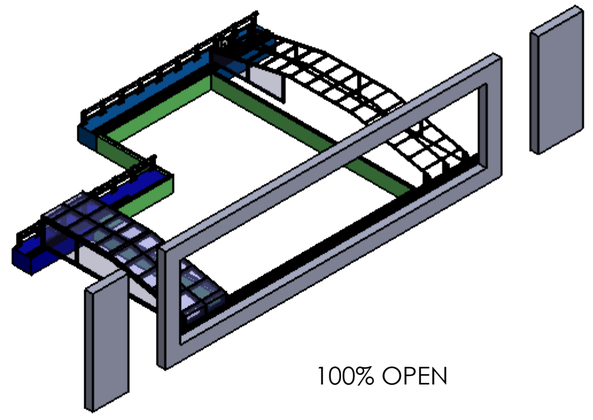

100% OPEN

NOTE :

THIS DRAWING ONLY FOR CLIENT APPROVAL
CIVIL STU. IN CLIENT SCOPE.

SPECIAL INSTRUCTION'S :

TITLE - ROOF AUTOMATION			NIHVA TECHNOLOGIES PVT.LTD.PUNE Website - www.nihva.com
DWG NO - NTPL-000-PM-001-00-00-00			
	NAME	SIGNATURE	DATE
DRAWN	J.P.		06-05-2026
CHK'D	B.S.		06-05-2026
APPV'D	V.T.		06-05-2026
If any queries contact - Design@nihva.com			
ALL DIMENSION ARE IN mm			A2
PRODUCT - RETRACTABLE ROOF			
PROJECT NO - NTPL-000-PM			REVISION - 00
SITE LOCATION - HYDERABAD			
MATRIAL -			QTY - 1
PROJECTION METHOD:			SCALE :
			SHEET 1 OF 1