


DWG.NO: SALT_1729_STR_02_R0

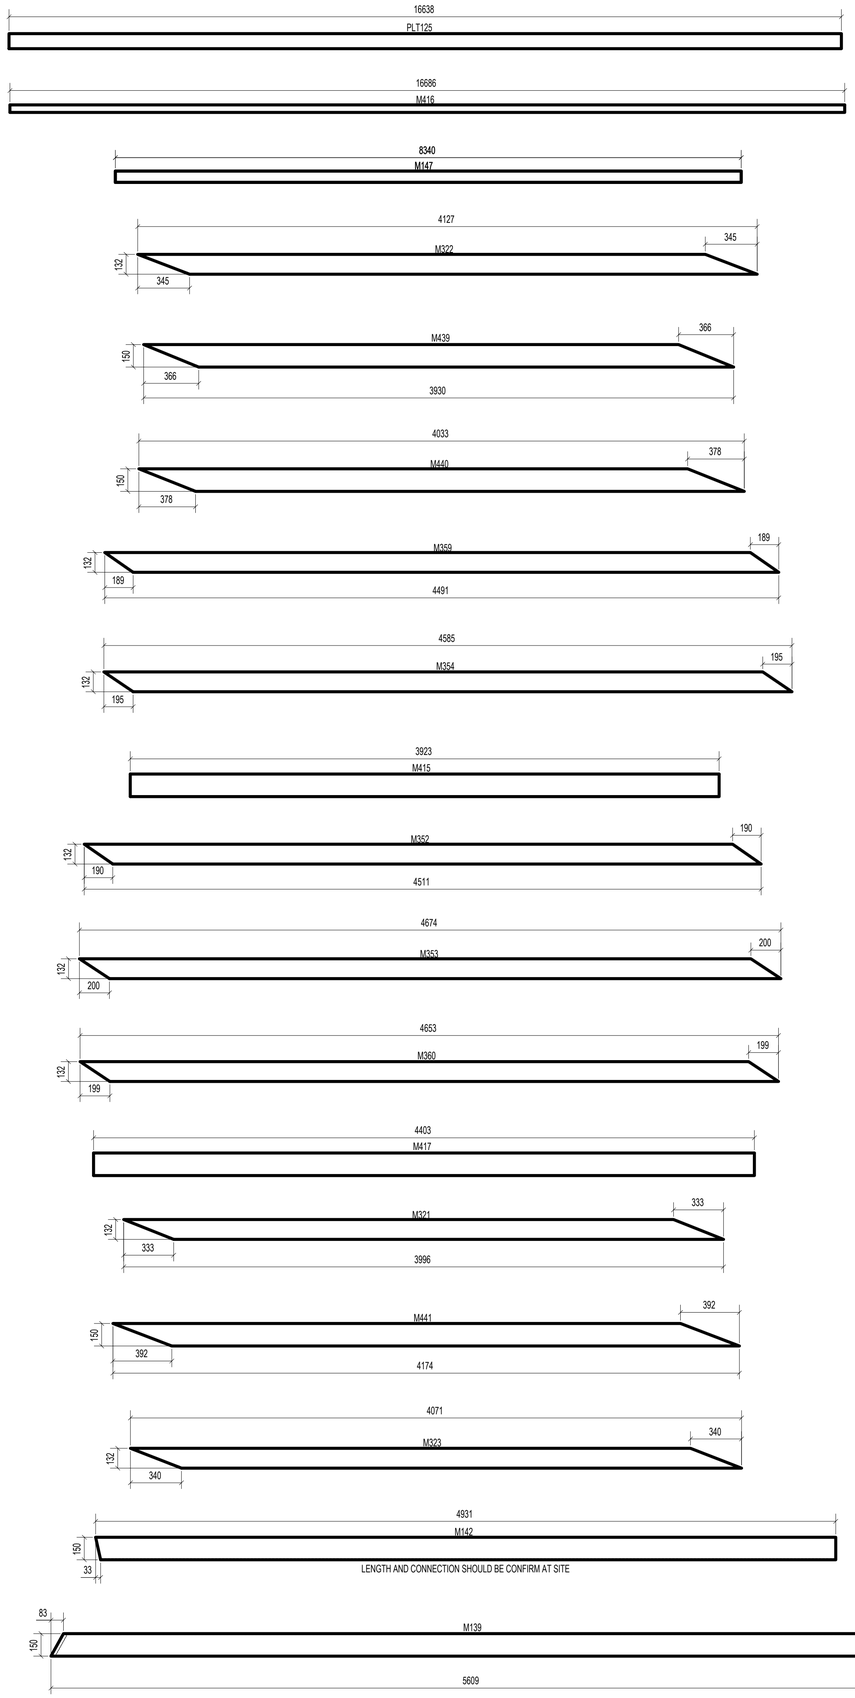


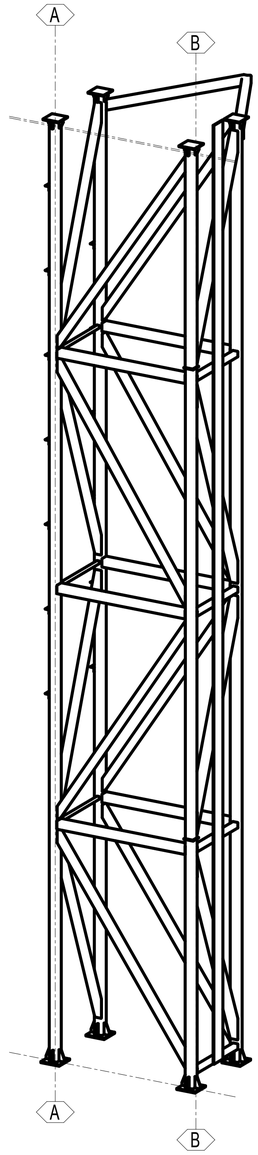



ISOMETRIC VIEW
1:50


CUTTING DETAIL BETWEEN GRID A & GRID B						
PartPos	Profile	No.	Material	Length	Net Weight(kg	Gross Weight(kg
M117	SHS50*3.6	3	IS2062	1350	7.08	21.24
M139	SHS150*8	1	IS2062	5609	198.06	198.06
M142	SHS150*8	1	IS2062	4931	175.32	175.32
M147	SHS150*8	1	IS2062	8340	297.49	297.49
M321	SHS132.0X132.0X4.8	1	IS2062	3996	68.37	68.37
M322	SHS132.0X132.0X4.8	2	IS2062	4127	70.58	141.16
M323	SHS132.0X132.0X4.8	1	IS2062	4071	69.64	69.64
M352	SHS132.0X132.0X4.8	1	IS2062	4511	80.73	80.73
M353	SHS132.0X132.0X4.8	2	IS2062	4674	83.59	167.18
M354	SHS132.0X132.0X4.8	2	IS2062	4585	82.03	164.06
M359	SHS132.0X132.0X4.8	1	IS2062	4491	80.38	80.38
M360	SHS132.0X132.0X4.8	2	IS2062	4653	83.24	166.48
M415	SHS150.0X150.0X5.0	1	IS2062	3923	87.34	87.34
M416	SHS150.0X150.0X5.0	3	IS2062	16686	371.47	1114.41
M417	SHS150.0X150.0X5.0	1	IS2062	4403	98.02	98.02
M424	SHS150.0X150.0X5.0	6	IS2062	2464	54.86	329.16
M439	SHS150.0X150.0X5.0	2	IS2062	3931	79.16	158.32
M440	SHS150.0X150.0X5.0	1	IS2062	4033	81.2	81.2
M441	SHS150.0X150.0X5.0	1	IS2062	4174	83.99	83.99
M495	SHS100.0X100.0X6.0	4	IS2062	1350	22.92	91.68
M535	ISA75X75X6	14	IS2062	150	1.02	14.28
PLT11	PL16*300	4	IS2062	300	11.3	45.2
PLT17	PL20*350	4	IS2062	350	19.23	76.92
PLT25	PL10*180	2	IS2062	180	2.54	5.08
PLT117	PL10*193	1	IS2062	210	3.18	3.18
PLT121	PL10*100	16	IS2062	200	1.21	19.36
PLT122	PL10*75	16	IS2062	150	0.66	10.56
PLT125	PLT16*300	1	IS2062	16638	626.92	626.92
	TOTAL					4475.73

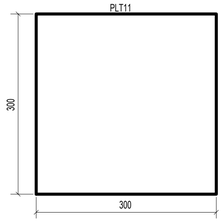


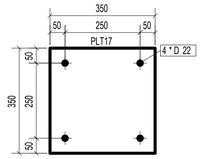


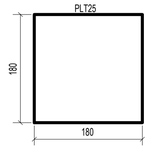

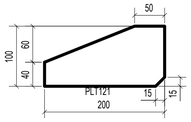


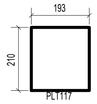


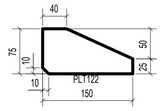

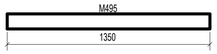



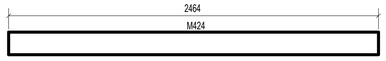

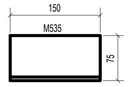

NOTES :–

1. ALL DIMENSIONS ARE IN MM & LEVEL ARE IN METER.
2. ALL STRUCTURAL STEEL AS PER IS:2062.
3. PROVIDE WELDING AS PER IS:816.
4. PROVIDE MIN. 6MM WELD WITH MIN. WELD LENGTH OF 150MM.
5. USE ELECTRODS AS PER IS:814 (PT.–I).
6. FILLET/ BUTT WELD SHALL BE OF 6MM SIZE AND SHALL BE CONTINUOUS.
7. FABRICATION AND ERECTION SHALL BE AS PER IS:800 AND IS:803.
8. WELD SHALL BE GROUND SMOOTH.
9. ALL GUSSET PLATES SHALL BE MIN. 10 THK.
10. ALL M.S. BLACK BOLTS AND NUTS SHALL CONFORM TO IS:1363(PT. 1 TO 3).
11. STRUCTURE SHALL BE APPLIED WITH ONE COAT OF RED OXIDE ZINC CROMATE PRIMER AFTER FABRICATION FOLLOWED ONE MORE COAT BEFORE ERECTION. FINALLY APPLY 2 COATS OF SYNTHETIC ENAMAL OF APPROVED QUALITY.

REV.NO.	DESCRIPTION.	REV.DATE	DRAWN.	CHKD.	APPD.
0	DRAWING FOR APPROVAL	27.12.22	AAK	HAB	HAB

DWG.TITLE :- CUTTING DETAIL BETWEEN GRID A & B
DRAWING FOR DOOR FRAME

PROJECT: MEGADOOR INSTALLATION AT HYDRABAD AIRPORT

CLIENT: GMR

SALT Design Services
NIHVA NIHVA TECHNOLOGIES PVT.LTD.

SALT DESIGN SERVICES

NIHVA TECHNOLOGIES PVT. LTD. PUNE
Tel : 020 66304033
Email:- info@nihva.com
Website:- www.nihva.com

DRAWN :AAK	CHECKED : HAB	SCALE: 1:100
APPROVED : HAB	JOB CODE. : 1729	DATE: 27.12.2022

DWG.NO: SALT_1729_STR_02_R0 (SH-1OF1) REV. - R0 SIZE. - A1

A1 [841 x 594]