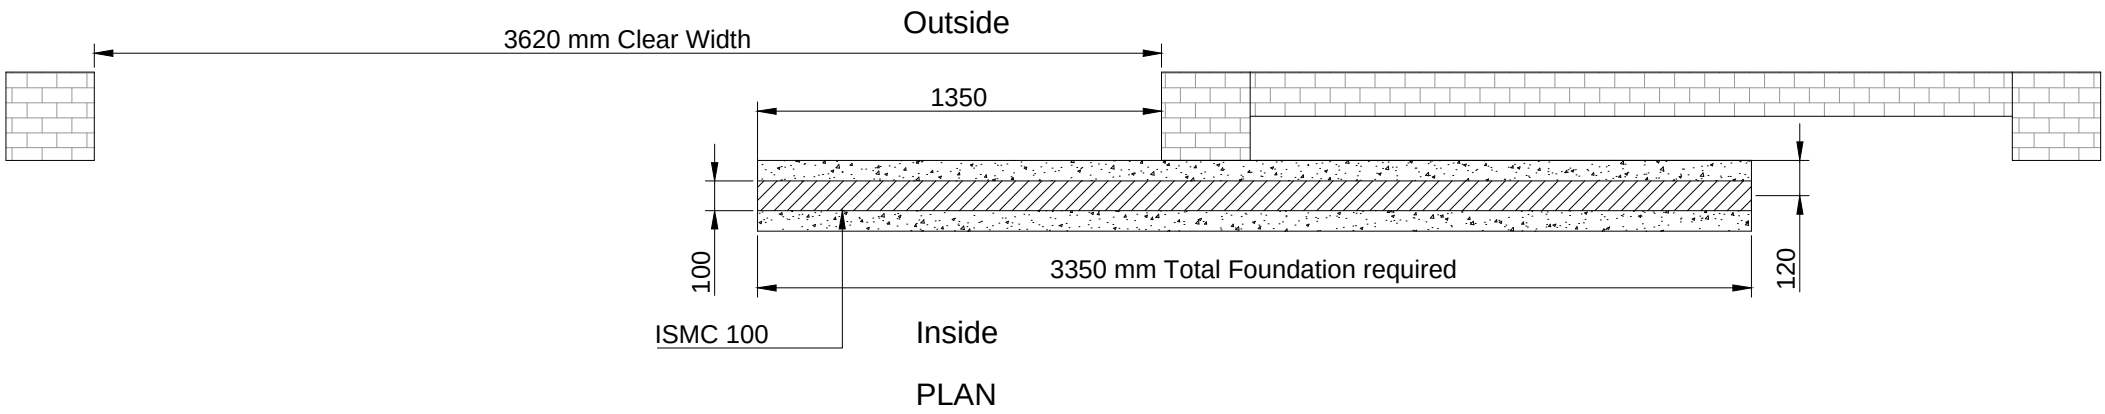

PLAN

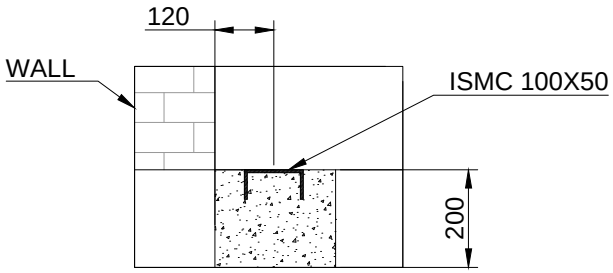

This drawing & designing is the property of NIHVA TECHNOLOGIES. Not to be sold or copied to any other concern.

TITLE: FOUNDATION FOR MANUAL SLIDING GATE			NIHVA TECHNOLOGIES PVT. LTD. PUNE Tel : 020 66304033 Email:- info@nihva.com Website:- www.nihva.com
	SIGN	DATE	
DRAWN	OMKAR	01/03/17	CLIENT - RBCC
CHECK	SAGAR P.	01/03/17	PROJECT - RESIDENCE PROJECT
REV.			SITE - AUNDH,PUNE
APPROVAL	R.K.	01/03/17	DWG. NO. : NIHVA/16-17/156
If any queries contact : projects@nihva.com			SCALE: NTS / WT: / SHEET: 01 OF 01
ALL DIMENSION ARE IN mm			