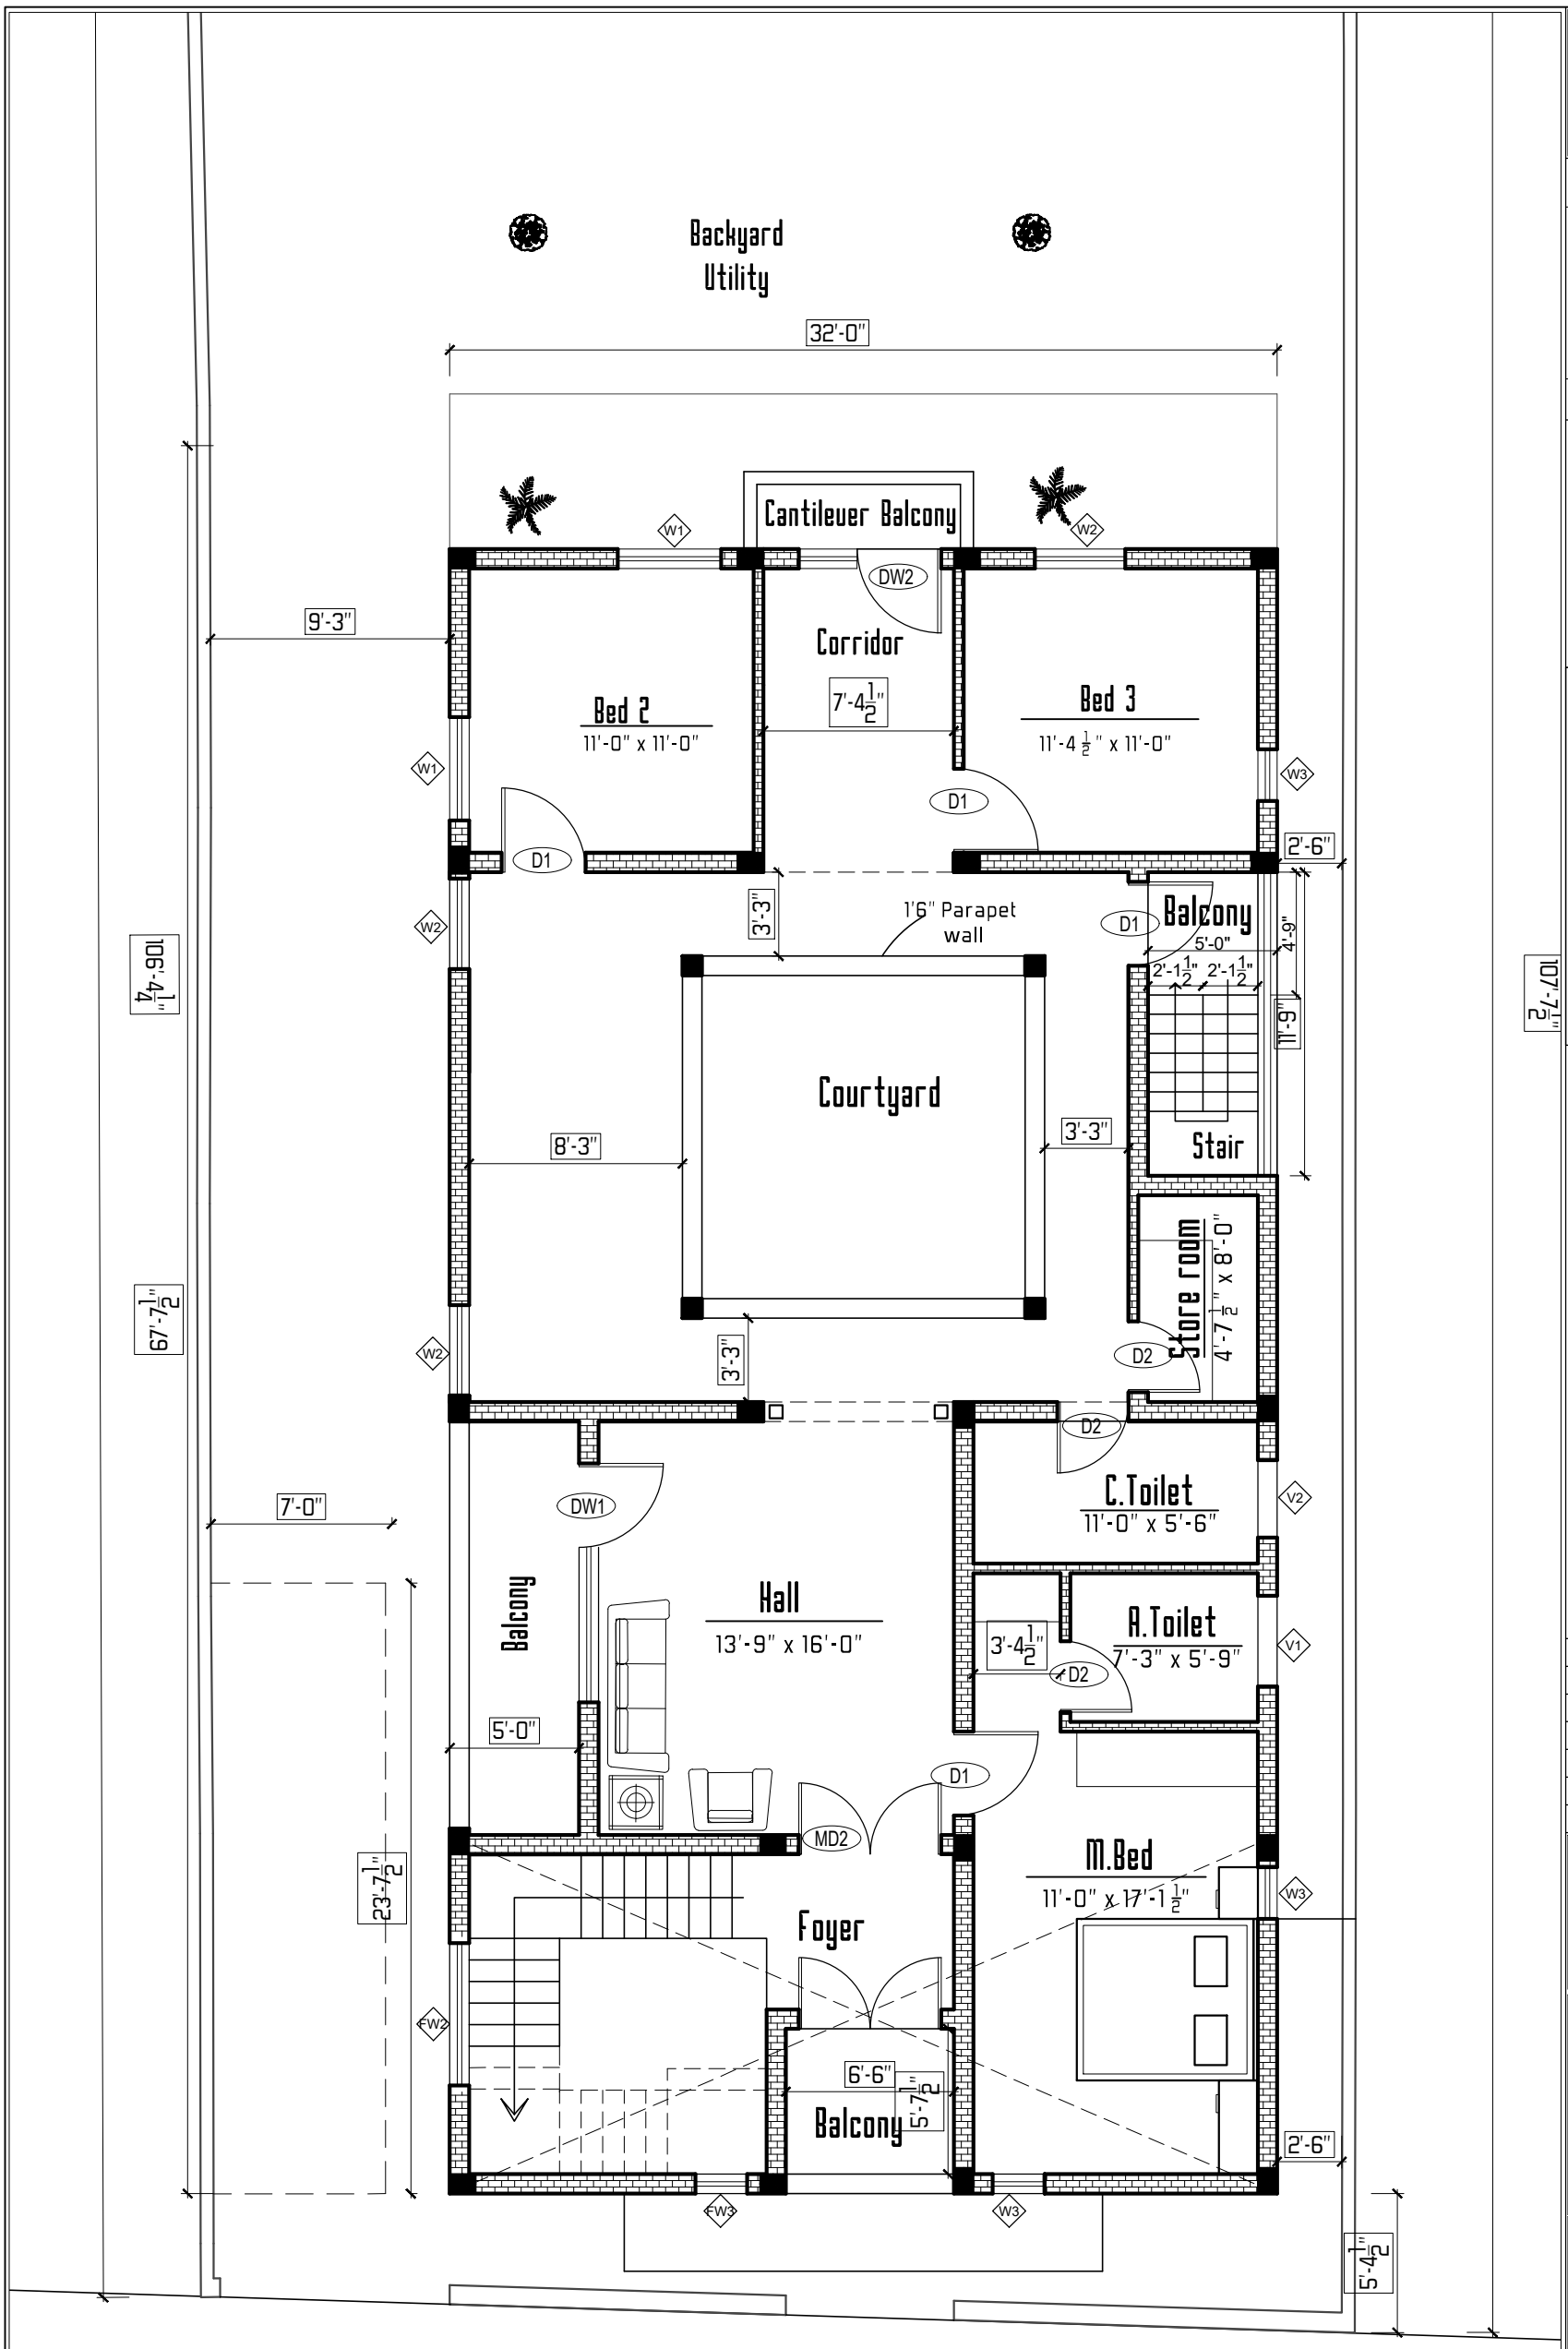


First Floor plan

Ownership & Disclaimer

The drawings and the details provided are the property of Naam Architects. The drawings should not be reproduced in any other format for any other project without the express content of the ARCHITECTS. The drawing and details produced are pertaining to the project mentioned in this sheet. The architects shall not be liable for unauthorized usage of the details in any other project or site.

Note:

1. Do not scale dimensions. figured dimensions only to be used.
2. All dimensions to be verified by the contractor and any discrepancies reported to the consultant before commencement of works.
3. All works, setting out, levels, components, materials and finishes are to be inspected and approved by the consultant before commencement of works.
4. This drawing is to be read with all related architects and engineers drawings, specifications and other, relevant information. any discrepancies are to be reported to the consultant immediately.

AREA STATEMENT

Ground Floor- 2135 Sqft
First Floor- 2075 Sqft
Back side veradah - 125 Sqft

rev	description	date
A	Issued for Construction	07.09.2021

Client:

Mr.Ameer
BEEMA NAGAR
TRICHY

Consultant Architect:

Naam Architects
architecture interior landscape
Ar. Kalilur rahman, M. B.arch.,
Ar. Jalaludeen, N. B.arch.,
Mob: 9042520000, 9043020000

Project title:

Ameer Residence
Beema nagar
Trichy

Sheet title:

First Floor Plan

Dwg no: A-02	Revision: A	dwn: PS
		checked: KR/JN
Project no: NA 253 AR		issued: KR/JN
Date: 07/09/2021	Scale:	DATE: ISSUED TO:

Sep07.2021