




SECTION- WALL C

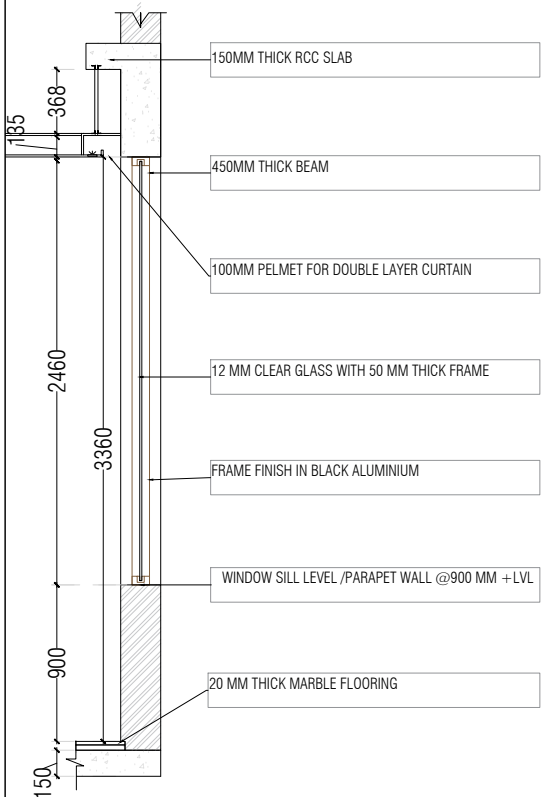

ELEVATION

C

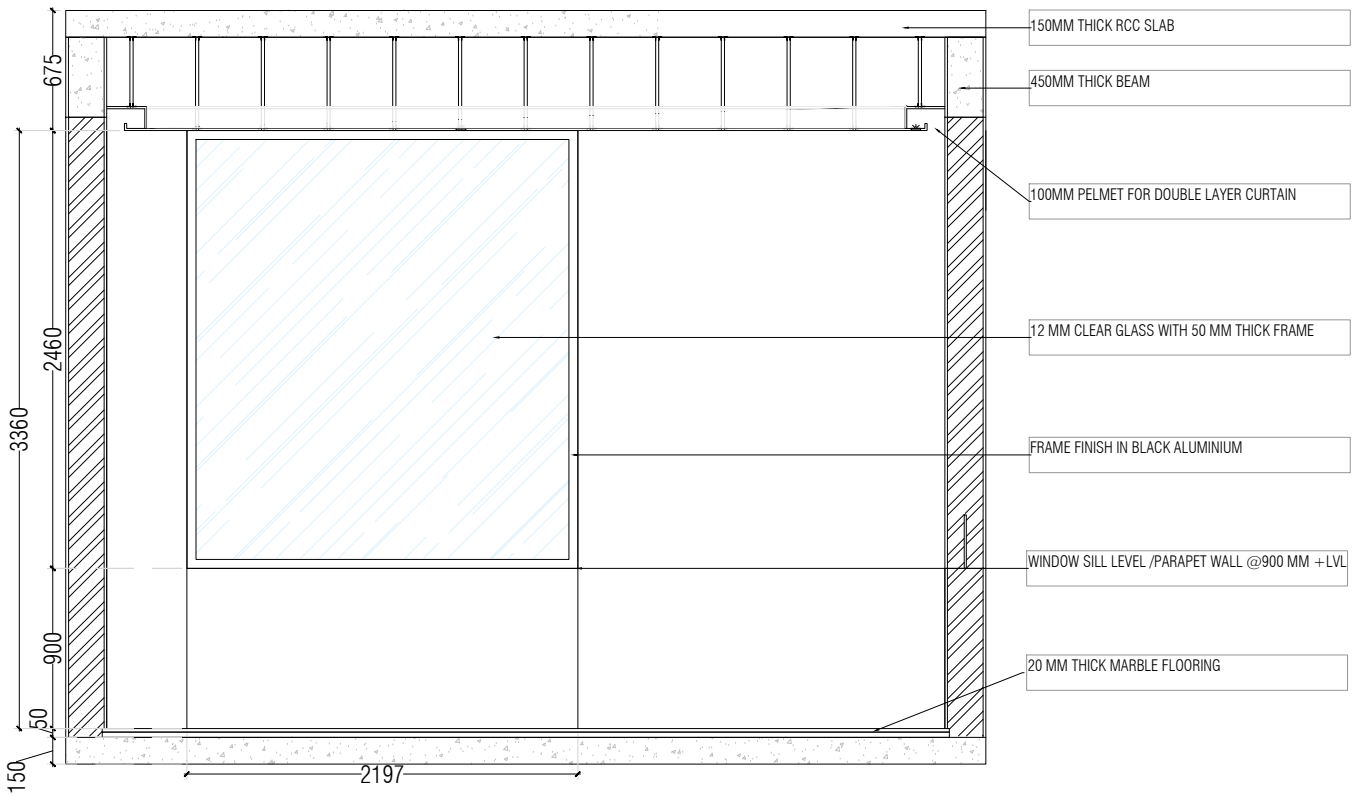

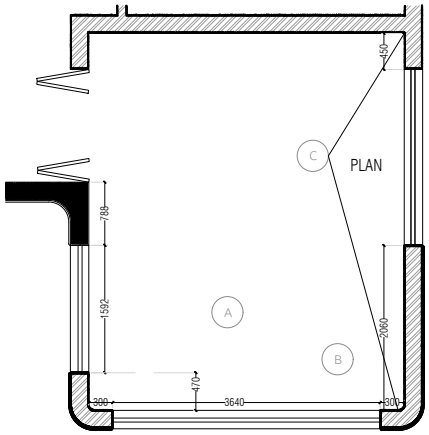

KEYPLAN



NAHATA HOUSE

PROJECT COORDINATOR:

DRAWN BY:	CHECKED BY:	ISSUE DATE:	REVISION NO:
GOKUL RAVI			R0

DRAWING TITLE:
WINDOW DETAILS

KEY PLAN:

PLOT DIRECTION:
N

choose any one

- SLD - SINGLE LINE DRAWING FOR TENDERING AND BOQ ONLY
- GFC - GOOD FOR CONSTRUCTION
- OFF SITE - NOT TO BE MADE AT SITE
- ON SITE - TO BE MADE AT SITE

DISCLAIMERS

- All construction activity at site to be done only with GFC drawings.
- All shop drawings provided by 3rd party consultants are to be approved by atelier astil before any material procurement or commencement of work based on 3rd party drawings.
- Site supervisor shall check and verify all dimensions before commencing any construction work, and discrepancy or omission to be immediately reported to the design team for issued revision drawings.
- Drawings are not to scale.
- All dimensions are in feet/inches unless otherwise specified. Only written dimension to be followed.
- All Clients are requested to co-relate and take prior approvals from independent Vastu Consultants before proceeding with site. atelier astil is not a Vastu Consultant.
- All drawings shall be shared digitally with a client appointed SPOC(single point of contact) and not to multiple 3rd parties.
- Check date and ignore previous drawings.


CLIENT APPROVAL :

DATE OF APPROVAL :


ATELIER ASTIL
ARCHITECTURE | INTERIOR | FURNITURE | BUILD

Lake villa ,126/1 gangadhar chetty road
Opposite Ulsoor lake, BANGALORE-42, Ph: 25592534,
E-mail: atelierastil@gmail.com

© The drawing and design is the copyright of atelier astil. No portion of this drawing may be reproduced without the written permission of Atelier Astil

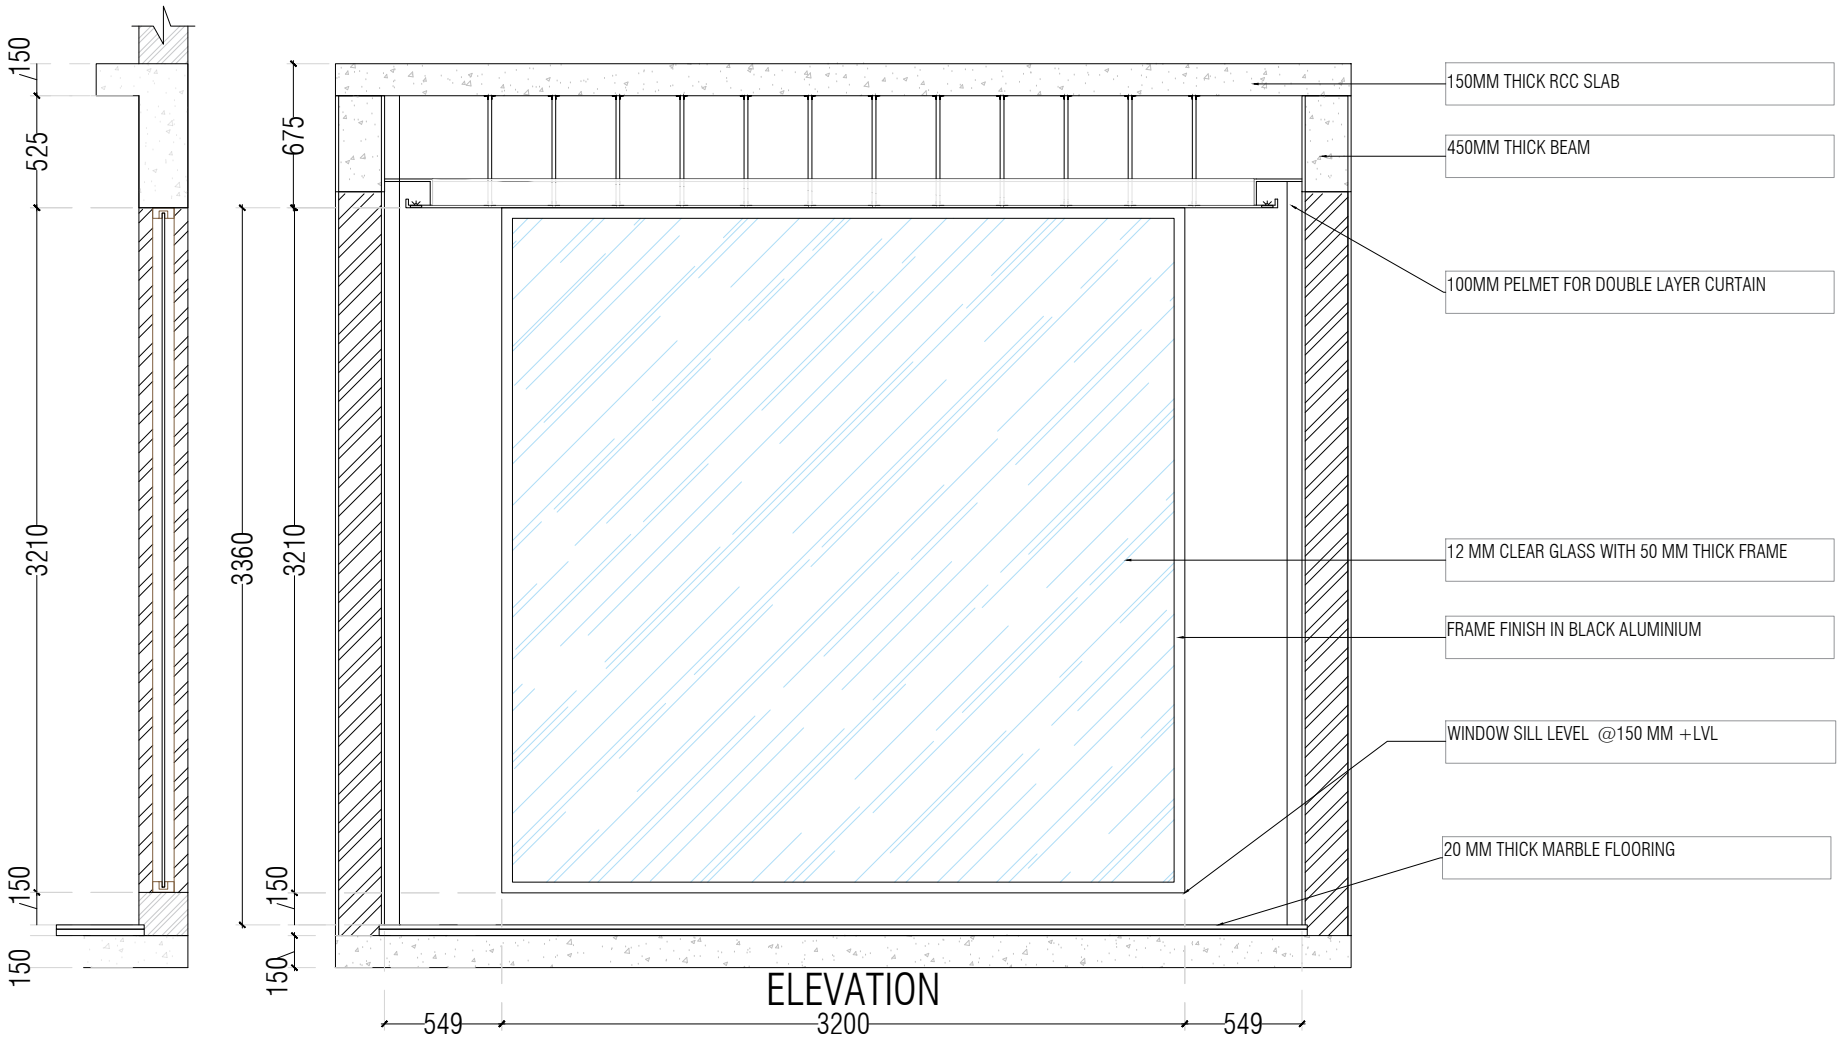

ELEVATION

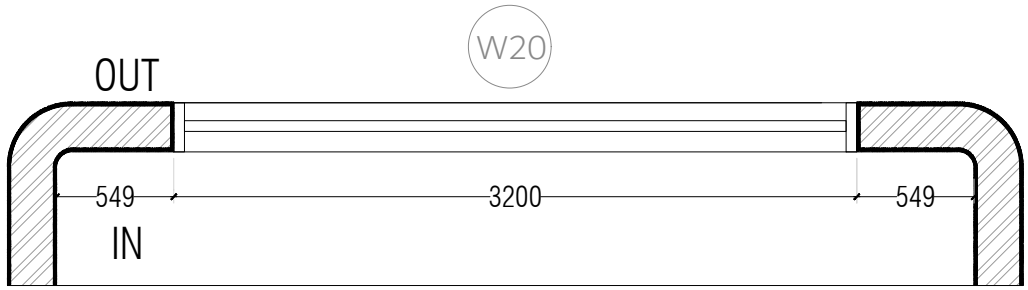

PLAN

NAHATA HOUSE

PROJECT COORDINATOR:

DRAWN BY:	CHECKED BY:	ISSUE DATE:	REVISION NO:
GOKUL RAVI			R0

DRAWING TITLE:
WINDOW DETAILS

KEY PLAN:

PLOT DIRECTION:
N

choose any one

- SLD - SINGLE LINE DRAWING FOR TENDERING AND BOQ ONLY
- GFC - GOOD FOR CONSTRUCTION
- OFF SITE - NOT TO BE MADE AT SITE
- ON SITE - TO BE MADE AT SITE

DISCLAIMERS

- All construction activity at site to be done only with GFC drawings.
- All shop drawings provided by 3rd party consultants are to be approved by atelier astil before any material procurement or commencement of work based on 3rd party drawings.
- Site supervisor shall check and verify all dimensions before commening any construction work, and discrepancy or omission to be immediately reported to the design team for issued revision drawings.
- Drawings are not to scale.
- All dimensions are in feet/inches unless otherwise specified.
  Only written dimension to be followed.
- All Clients are requested to co-relate and take prior approvals from independent Vastu Consultants before proceeding with site.
  atelier astil is not a Vastu Consultant.
- All drawings shall be shared digitally with a client appointed SPOC(single point of contact) and not to multiple 3rd parties.
- Check date and ignore previous drawings.


CLIENT APPROVAL :

DATE OF APPROVAL :


ATELIER ASTIL
ARCHITECTURE | INTERIOR | FURNITURE | BUILD

Lake villa ,126/1 gangadhar chetty road
Opposite Ulsoor lake, BANGALORE-42, Ph: 25592534,
E-mail: atelierastil@gmail.com

© The drawing and design is the copyright of atelier astil. No portion of this drawing may be reproduced without the written permission of Atelier Astil

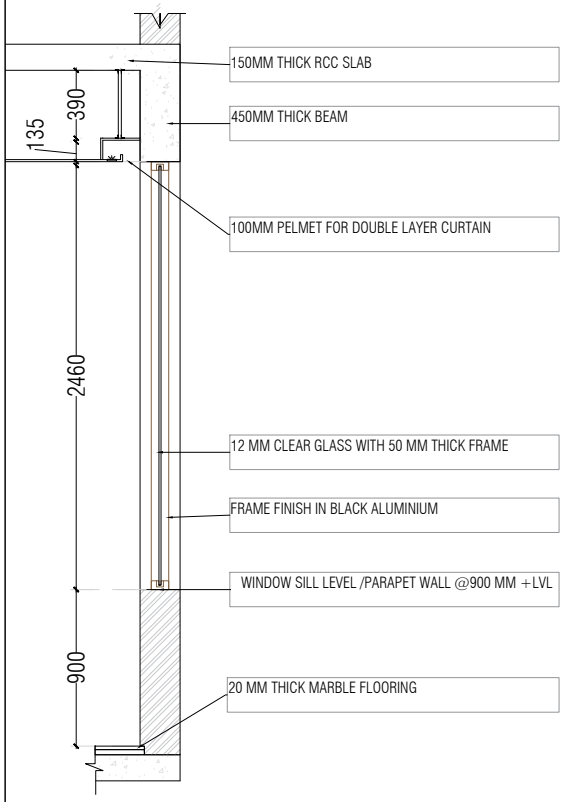


SECTION- WALL B

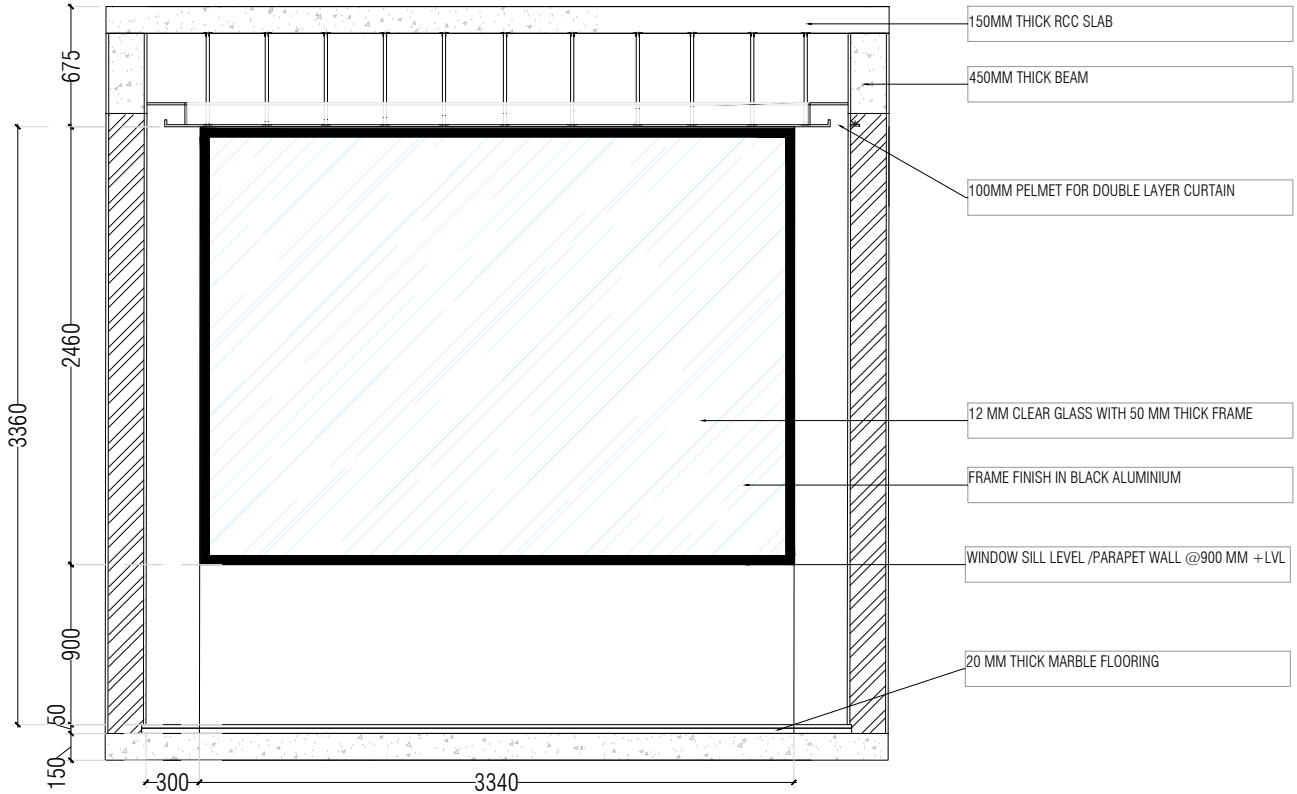

ELEVATION

B



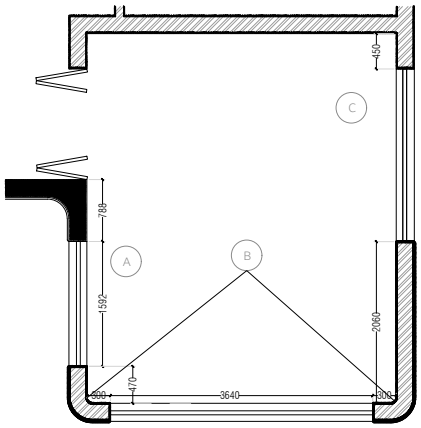

KEY PLAN



NAHATA HOUSE

PROJECT COORDINATOR:

DRAWN BY:	CHECKED BY:	ISSUE DATE:	REVISION NO:
GOKUL RAVI			R0

DRAWING TITLE:
WINDOW DETAILS

KEY PLAN:

PLOT DIRECTION:
N

choose any one

SLD - SINGLE LINE DRAWING FOR TENDERING AND BOQ ONLY

GFC - GOOD FOR CONSTRUCTION

OFF SITE - NOT TO BE MADE AT SITE

ON SITE - TO BE MADE AT SITE

DISCLAIMERS

- All construction activity at site to be done only with GFC drawings.
- All shop drawings provided by 3rd party consultants are to be approved by atelier astil before any material procurement or commencement of work based on 3rd party drawings.
- Site supervisor shall check and verify all dimensions before commencing any construction work, and discrepancy or omission to be immediately reported to the design team for issued revision drawings.
- Drawings are not to scale.
- All dimensions are in feet/inches unless otherwise specified.
  Only written dimension to be followed.
- All Clients are requested to co-relate and take prior approvals from independent Vastu Consultants before proceeding with site.
  atelier astil is not a Vastu Consultant.
- All drawings shall be shared digitally with a client appointed SPOC(single point of contact) and not to multiple 3rd parties.
- Check date and ignore previous drawings.


CLIENT APPROVAL :

DATE OF APPROVAL :


ATELIER ASTIL
ARCHITECTURE | INTERIOR | FURNITURE | BUILD

Lake villa ,126/1 gangadhar chetty road
Opposite Ulsoor lake, BANGALORE-42, Ph: 25592534,
E-mail: atelierastil@gmail.com

© The drawing and design is the copyright of atelier astil. No portion of this drawing may be reproduced without the written permission of Atelier Astil

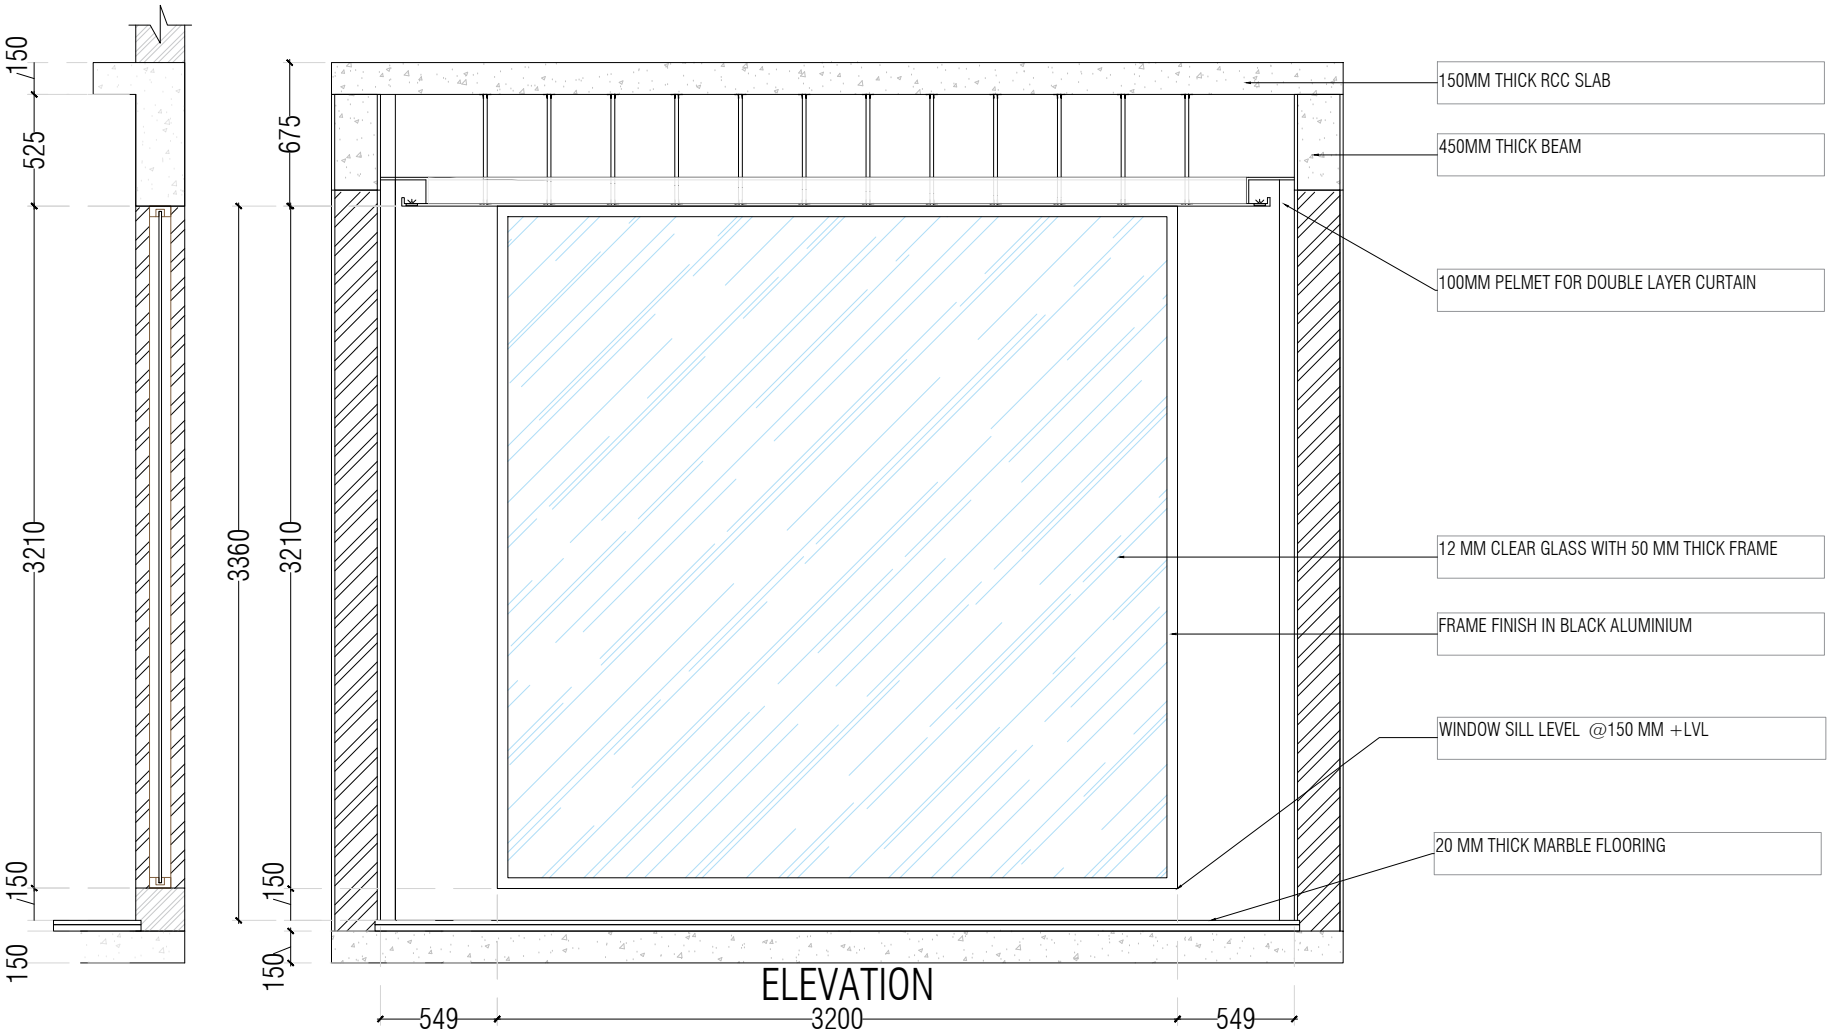

ELEVATION

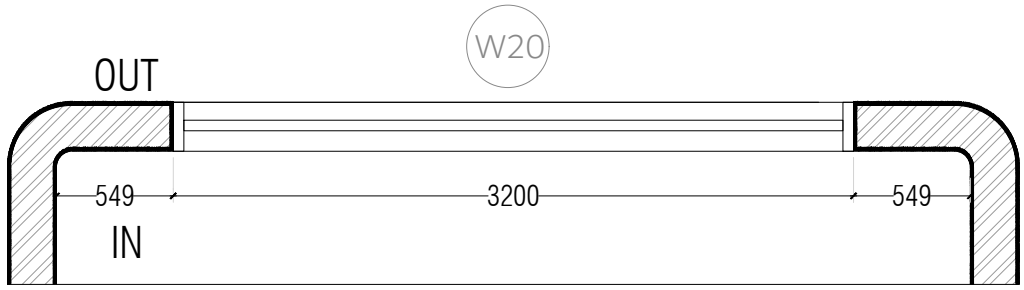

PLAN

NAHATA HOUSE

PROJECT COORDINATOR:

DRAWN BY:	CHECKED BY:	ISSUE DATE:	REVISION NO:
GOKUL RAVI			R0

DRAWING TITLE:
WINDOW DETAILS

KEY PLAN:

PLOT DIRECTION:
N

choose any one

- SLD - SINGLE LINE DRAWING FOR TENDERING AND BOQ ONLY
- GFC - GOOD FOR CONSTRUCTION
- OFF SITE - NOT TO BE MADE AT SITE
- ON SITE - TO BE MADE AT SITE

DISCLAIMERS

- All construction activity at site to be done only with GFC drawings.
- All shop drawings provided by 3rd party consultants are to be approved by atelier astil before any material procurement or commencement of work based on 3rd party drawings.
- Site supervisor shall check and verify all dimensions before commencing any construction work, and discrepancy or omission to be immediately reported to the design team for issued revision drawings.
- Drawings are not to scale.
- All dimensions are in feet/inches unless otherwise specified.
  Only written dimension to be followed.
- All Clients are requested to co-relate and take prior approvals from independent Vastu Consultants before proceeding with site.
  atelier astil is not a Vastu Consultant.
- All drawings shall be shared digitally with a client appointed SPOC(single point of contact) and not to multiple 3rd parties.
- Check date and ignore previous drawings.


CLIENT APPROVAL :


DATE OF APPROVAL :

ATELIER ASTIL
ARCHITECTURE | INTERIOR | FURNITURE | BUILD

Lake villa ,126/1 gangadhar chetty road
Opposite Ulsoor lake, BANGALORE-42, Ph: 25592534,
E-mail: atelierastil@gmail.com

© The drawing and design is the copyright of atelier astil. No portion of this drawing may be reproduced without the written permission of Atelier Astil

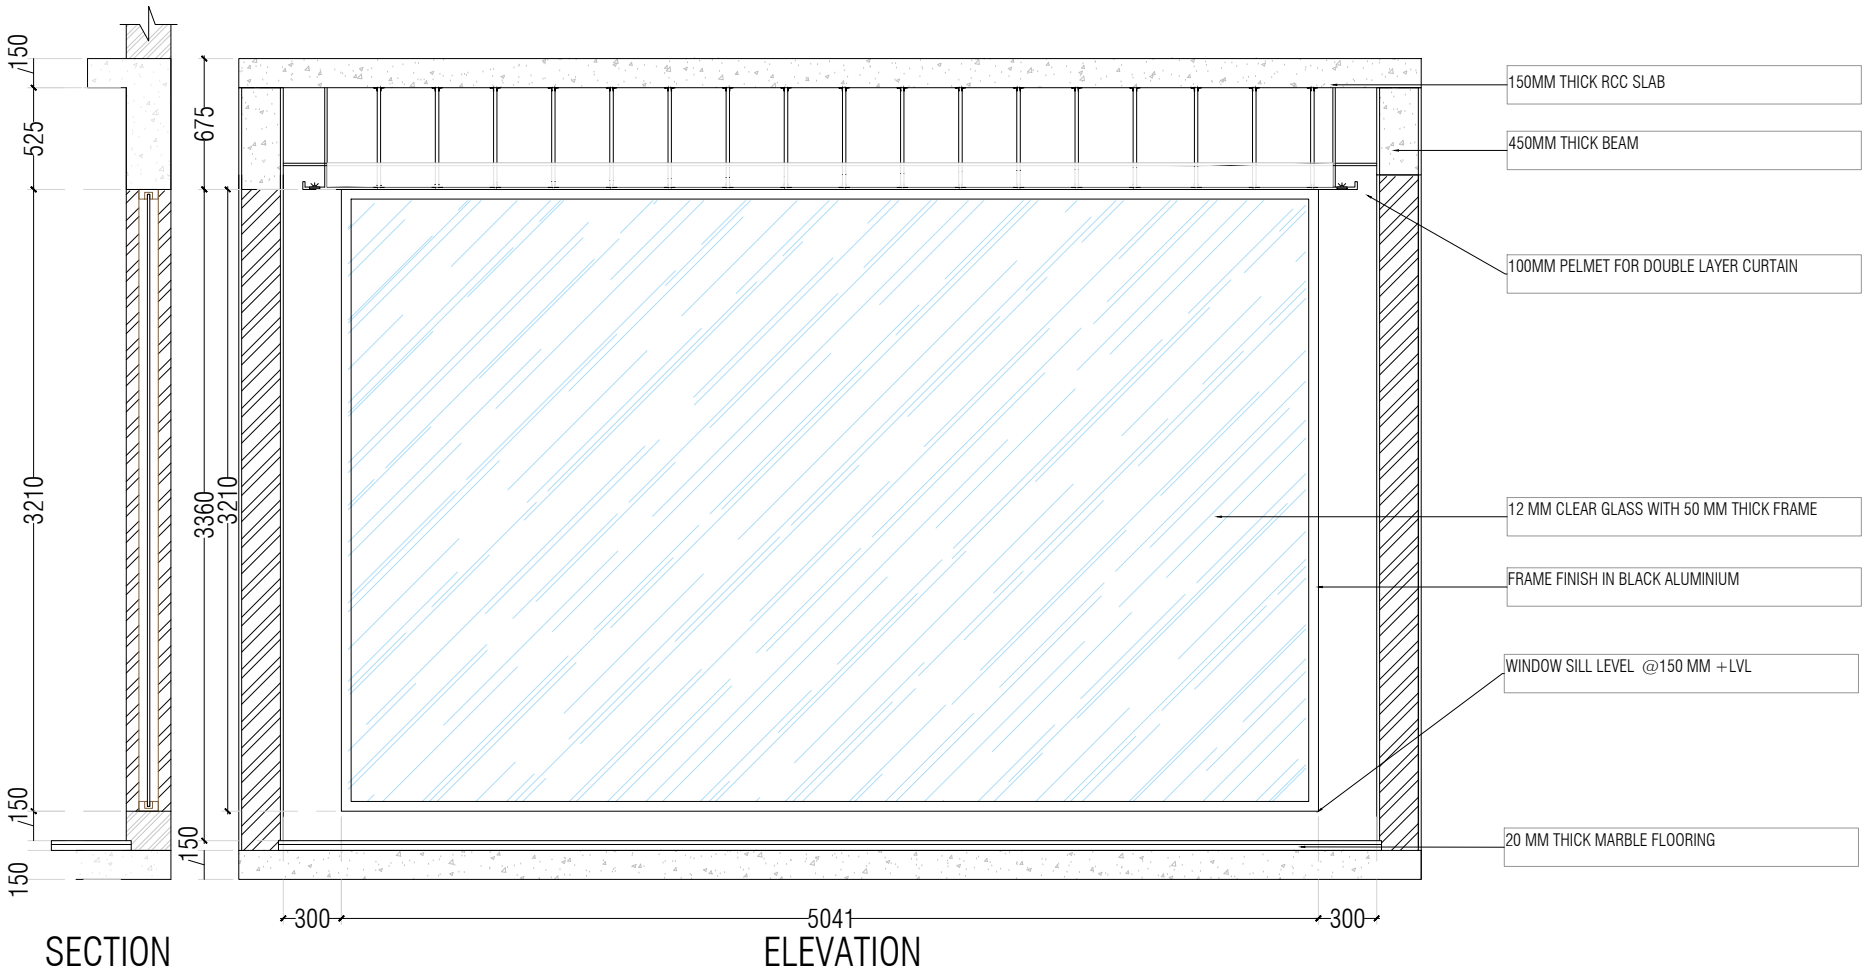

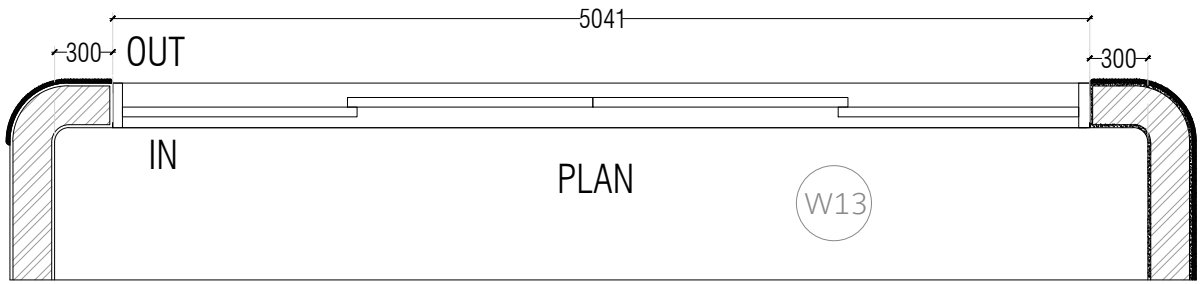

NAHATA HOUSE

PROJECT COORDINATOR:

DRAWN BY:	CHECKED BY:	ISSUE DATE:	REVISION NO.:
GOKUL RAVI			R0

DRAWING TITLE:
WINDOW DETAILS

KEY PLAN:

PLOT DIRECTION:
N

choose any one

- SLD - SINGLE LINE DRAWING FOR TENDERING AND BOQ ONLY
- GFC - GOOD FOR CONSTRUCTION
- OFF SITE - NOT TO BE MADE AT SITE
- ON SITE - TO BE MADE AT SITE

DISCLAIMERS

- All construction activity at site to be done only with GFC drawings.
- All shop drawings provided by 3rd party consultants are to be approved by atelier astil before any material procurement or commencement of work based on 3rd party drawings.
- Site supervisor shall check and verify all dimensions before commencing any construction work, and discrepancy or omission to be immediately reported to the design team for issued revision drawings.
- Drawings are not to scale.
- All dimensions are in feet/inches unless otherwise specified.
  Only written dimension to be followed.
- All Clients are requested to co-relate and take prior approvals from independent Vastu Consultants before proceeding with site.
  atelier astil is not a Vastu Consultant.
- All drawings shall be shared digitally with a client appointed SPOC(single point of contact) and not to multiple 3rd parties.
- Check date and ignore previous drawings.


CLIENT APPROVAL :

DATE OF APPROVAL :


ATELIER ASTIL
ARCHITECTURE | INTERIOR | FURNITURE | BUILD

Lake villa ,126/1 gangadhar chetty road
Opposite Ulsoor lake, BANGALORE-42, Ph: 25592534,
E-mail: atelierastil@gmail.com

© The drawing and design is the copyright of atelier astil. No portion of this drawing may be reproduced without the written permission of Atelier Astil

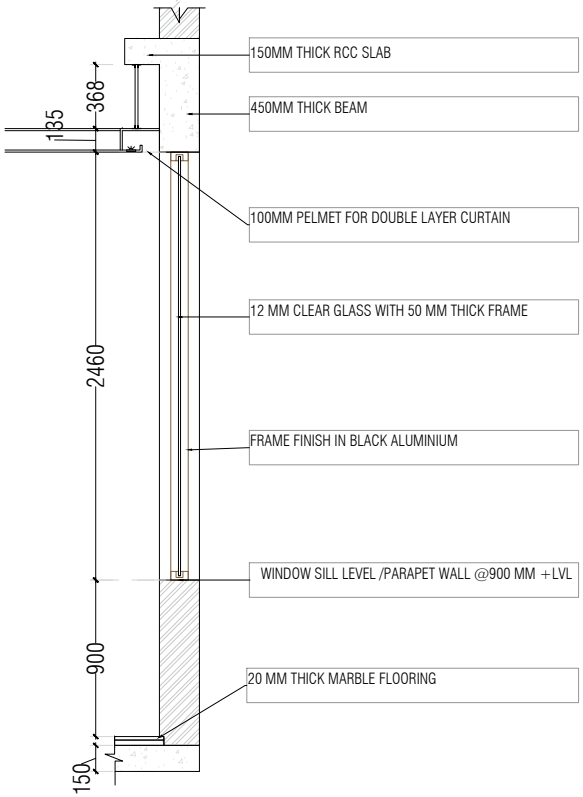


SECTION- WALL A

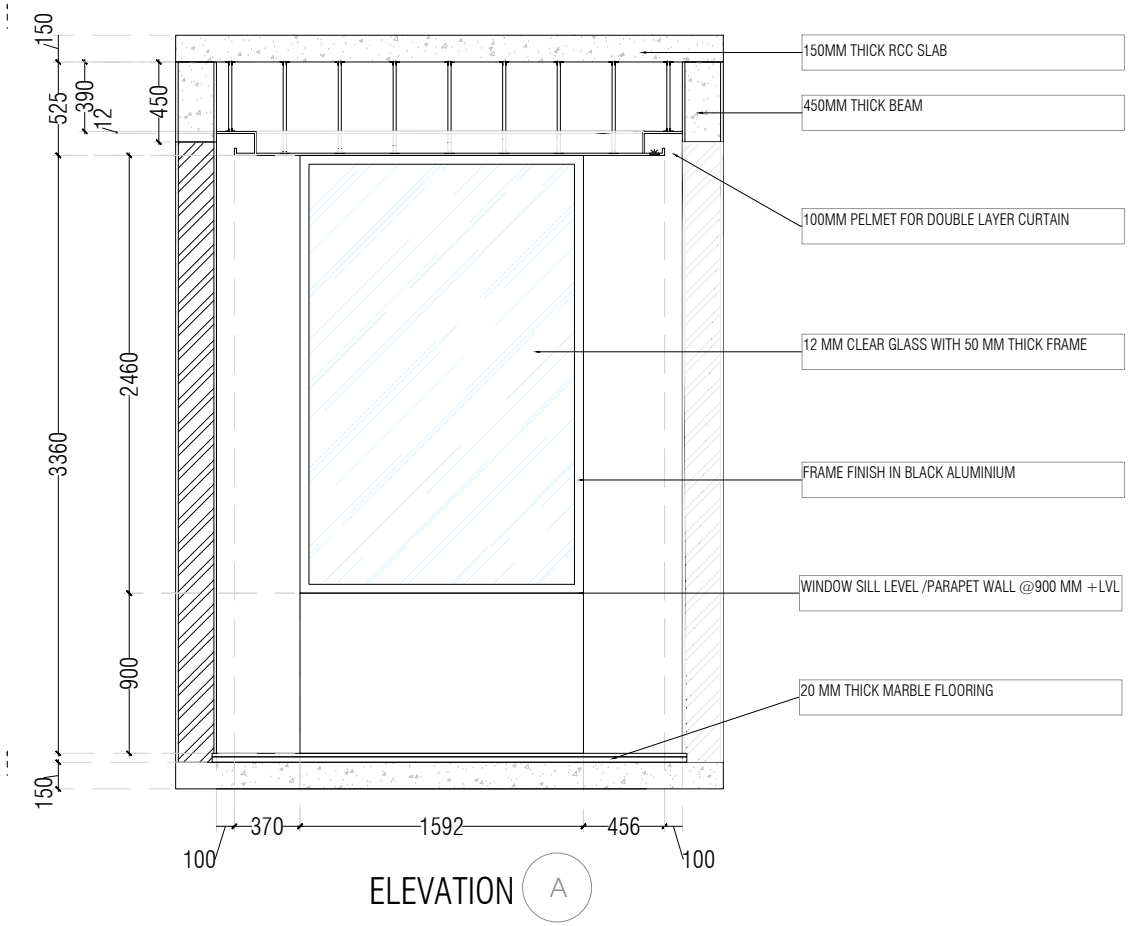

ELEVATION A



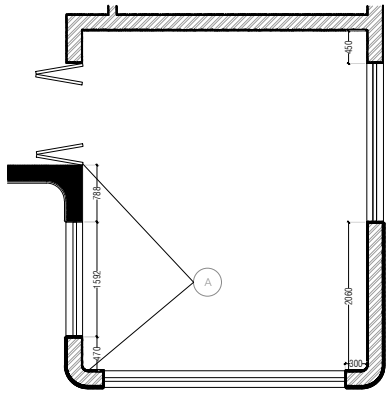

KEY PLAN



NAHATA HOUSE

PROJECT COORDINATOR:

DRAWN BY:	CHECKED BY:	ISSUE DATE:	REVISION NO:
GOKUL RAVI			R0

DRAWING TITLE:
WINDOW DETAILS

KEY PLAN:

PLOT DIRECTION:
N

choose any one

- SLD - SINGLE LINE DRAWING FOR TENDERING AND BOQ ONLY
- GFC - GOOD FOR CONSTRUCTION
- OFF SITE - NOT TO BE MADE AT SITE
- ON SITE - TO BE MADE AT SITE

DISCLAIMERS

- All construction activity at site to be done only with GFC drawings.
- All shop drawings provided by 3rd party consultants are to be approved by atelier astil before any material procurement or commencement of work based on 3rd party drawings.
- Site supervisor shall check and verify all dimensions before commencing any construction work, and discrepancy or omission to be immediately reported to the design team for issued revision drawings.
- Drawings are not to scale.
- All dimensions are in feet/inches unless otherwise specified.
  Only written dimension to be followed.
- All Clients are requested to co-relate and take prior approvals from independent Vastu Consultants before proceeding with site.
  atelier astil is not a Vastu Consultant.
- All drawings shall be shared digitally with a client appointed SPOC(single point of contact) and not to multiple 3rd parties.
- Check date and ignore previous drawings.


CLIENT APPROVAL :

DATE OF APPROVAL :

ATELIER ASTIL
ARCHITECTURE | INTERIOR | FURNITURE | BUILD


Lake villa ,126/1 gangadhar chetty road
Opposite Ulsoor lake, BANGALORE-42, Ph: 25592534,
E-mail: atelierastil@gmail.com

© The drawing and design is the copyright of atelier astil. No portion of this drawing may be reproduced without the written permission of Atelier Astil

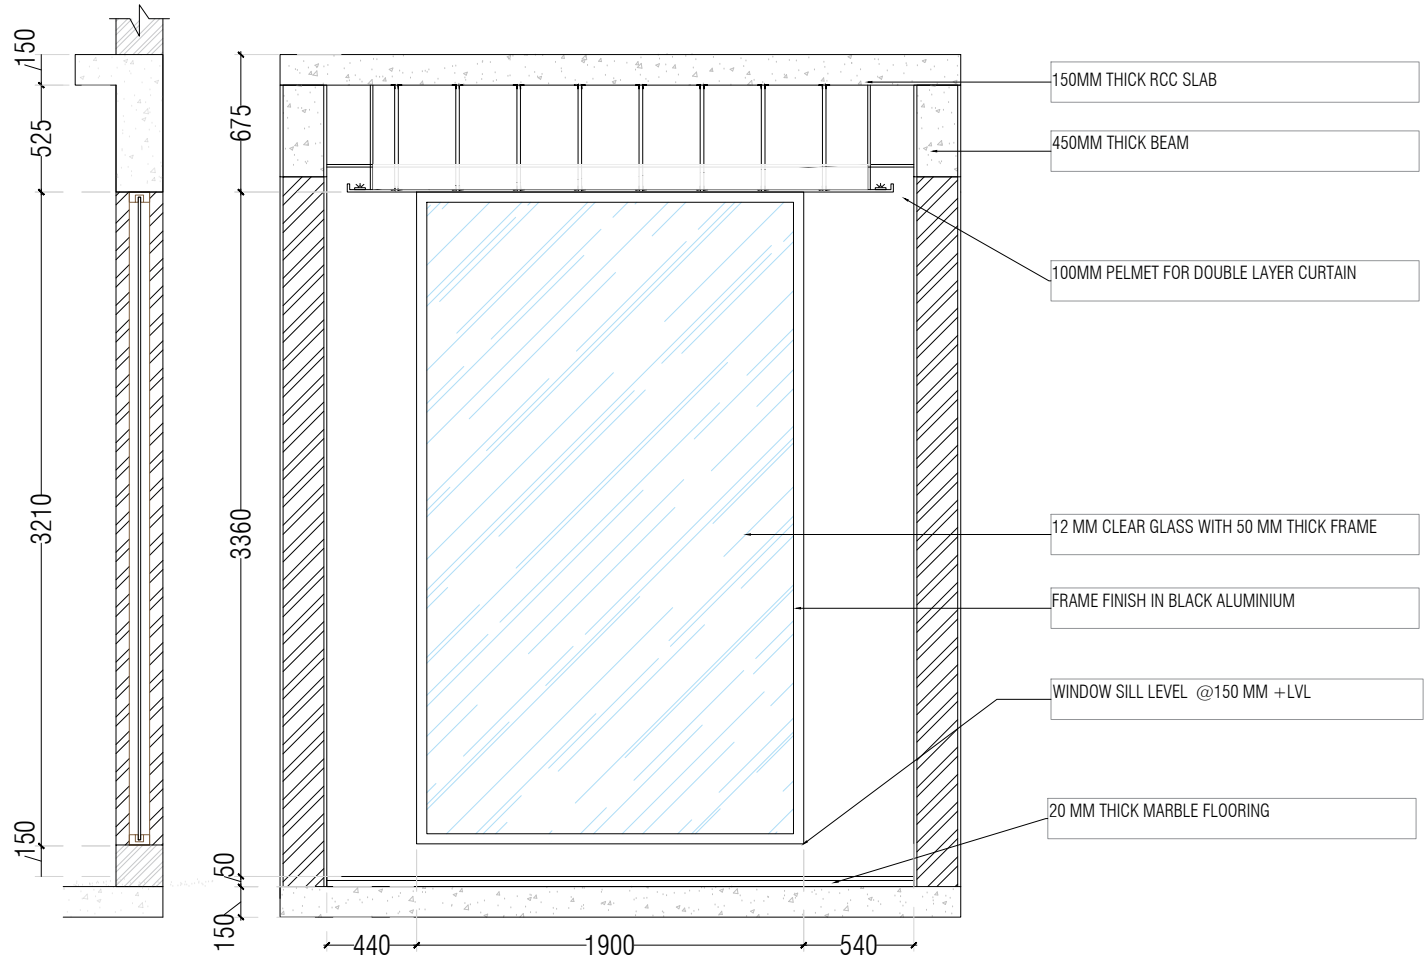

SECTION

ELEVATION

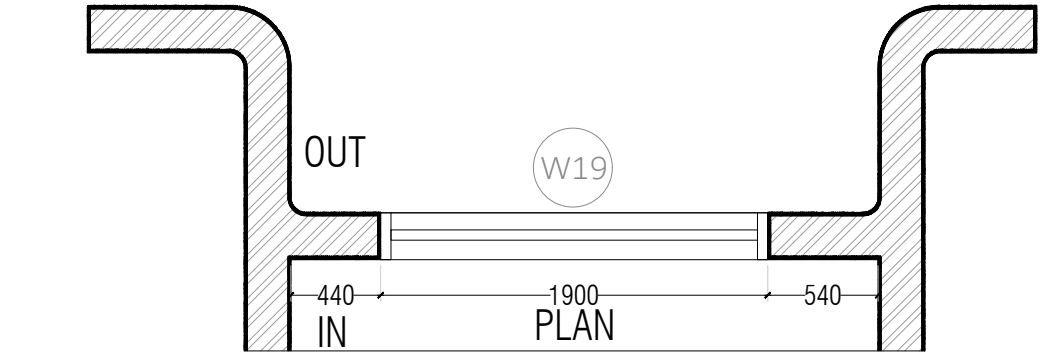

PLAN

NAHATA HOUSE

PROJECT COORDINATOR:

DRAWN BY:	CHECKED BY:	ISSUE DATE:	REVISION NO:
GOKUL RAVI			R0

DRAWING TITLE:

WINDOW DETAILS

KEY PLAN:

PLOT DIRECTION:

N

choose any one

- SLD - SINGLE LINE DRAWING FOR TENDERING AND BOQ ONLY
- GFC - GOOD FOR CONSTRUCTION
- OFF SITE - NOT TO BE MADE AT SITE
- ON SITE - TO BE MADE AT SITE

DISCLAIMERS

- All construction activity at site to be done only with GFC drawings.
- All shop drawings provided by 3rd party consultants are to be approved by atelier astil before any material procurement or commencement of work based on 3rd party drawings.
- Site supervisor shall check and verify all dimensions before commencing any construction work, and discrepancy or omission to be immediately reported to the design team for issued revision drawings.
- Drawings are not to scale.
- All dimensions are in feet/inches unless otherwise specified.
  Only written dimension to be followed.
- All Clients are requested to co-relate and take prior approvals from independent Vastu Consultants before proceeding with site. atelier astil is not a Vastu Consultant.
- All drawings shall be shared digitally with a client appointed SPOC(single point of contact) and not to multiple 3rd parties.
- Check date and ignore previous drawings.


CLIENT APPROVAL :

DATE OF APPROVAL :

ATELIER ASTIL
ARCHITECTURE | INTERIOR | FURNITURE | BUILD


Lake villa ,126/1 gangadhar chetty road
Opposite Ulsoor lake, BANGALORE-42, Ph: 25592534,
E-mail: atelierastil@gmail.com

© The drawing and design is the copyright of atelier astil. No portion of this drawing may be reproduced without the written permission of Atelier Astil

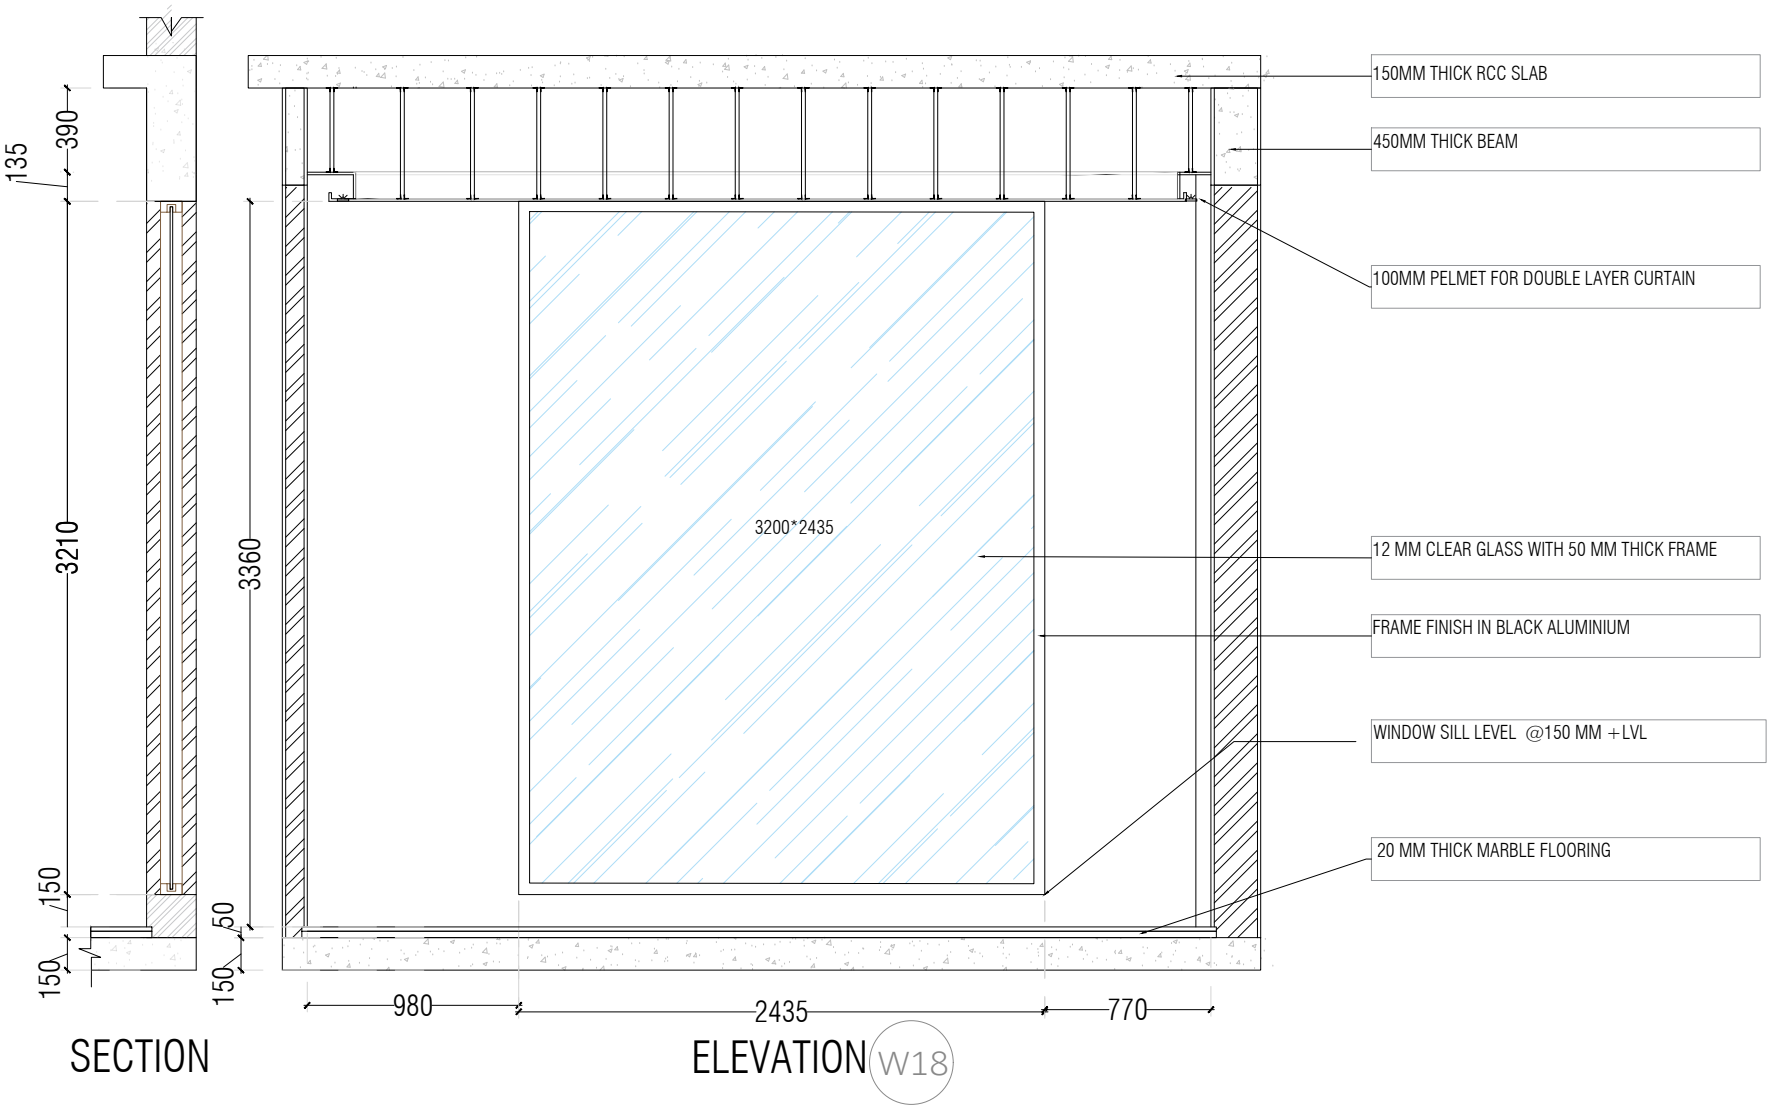

SECTION

ELEVATION W18

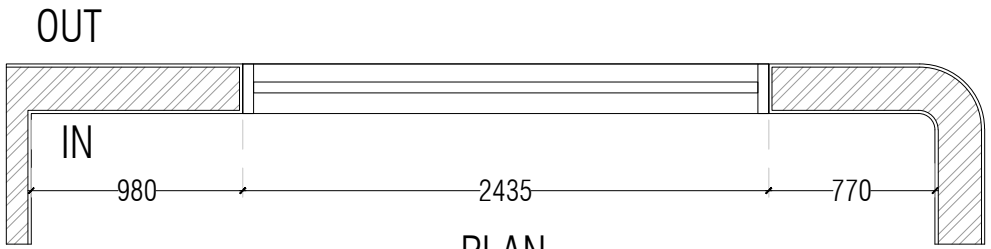

PLAN

NAHATA HOUSE

PROJECT COORDINATOR:

DRAWN BY:	CHECKED BY:	ISSUE DATE:	REVISION NO:
GOKUL RAVI			R0

DRAWING TITLE:
WINDOW DETAILS

KEY PLAN:

PLOT DIRECTION:
N

choose any one

- SLD - SINGLE LINE DRAWING FOR TENDERING AND BOQ ONLY
- GFC - GOOD FOR CONSTRUCTION
- OFF SITE - NOT TO BE MADE AT SITE
- ON SITE - TO BE MADE AT SITE

DISCLAIMERS

- All construction activity at site to be done only with GFC drawings.
- All shop drawings provided by 3rd party consultants are to be approved by atelier astil before any material procurement or commencement of work based on 3rd party drawings.
- Site supervisor shall check and verify all dimensions before commencing any construction work, and discrepancy or omission to be immediately reported to the design team for issued revision drawings.
- Drawings are not to scale.
- All dimensions are in feet/inches unless otherwise specified.
  Only written dimension to be followed.
- All Clients are requested to co-relate and take prior approvals from independent Vastu Consultants before proceeding with site.
  atelier astil is not a Vastu Consultant.
- All drawings shall be shared digitally with a client appointed SPOC(single point of contact) and not to multiple 3rd parties.
- Check date and ignore previous drawings.

CLIENT APPROVAL :

DATE OF APPROVAL :

ATELIER ASTIL
ARCHITECTURE | INTERIOR | FURNITURE | BUILD

Lake villa ,126/1 gangadhar chetty road
Opposite Ulsoor lake, BANGALORE-42, Ph: 25592534,
E-mail: atelierastil@gmail.com

© The drawing and design is the copyright of atelier astil. No portion of this drawing may be reproduced without the written permission of Atelier Astil