ITEM NO.	PART NUMBER	DESCRIPTION	MATERIAL	QTY
1	INTERMEDIATE SUPPORT	SQ TUBE 50X50X1174	AL	1
2	INTERMEDIATE SUPPORT WELDNG PLATE	120X50 3 MM THK	AL	2

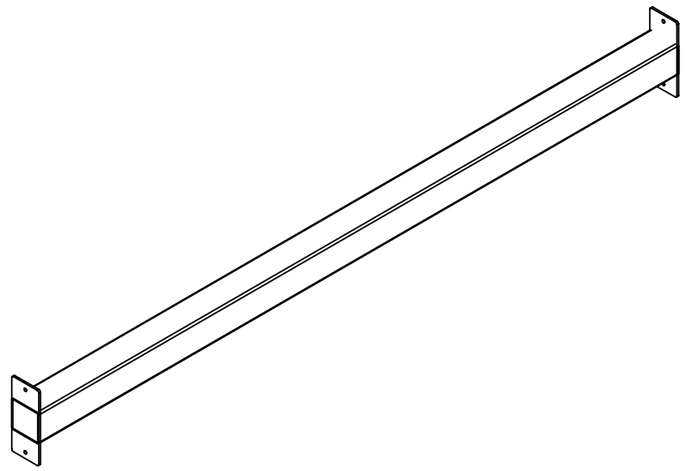

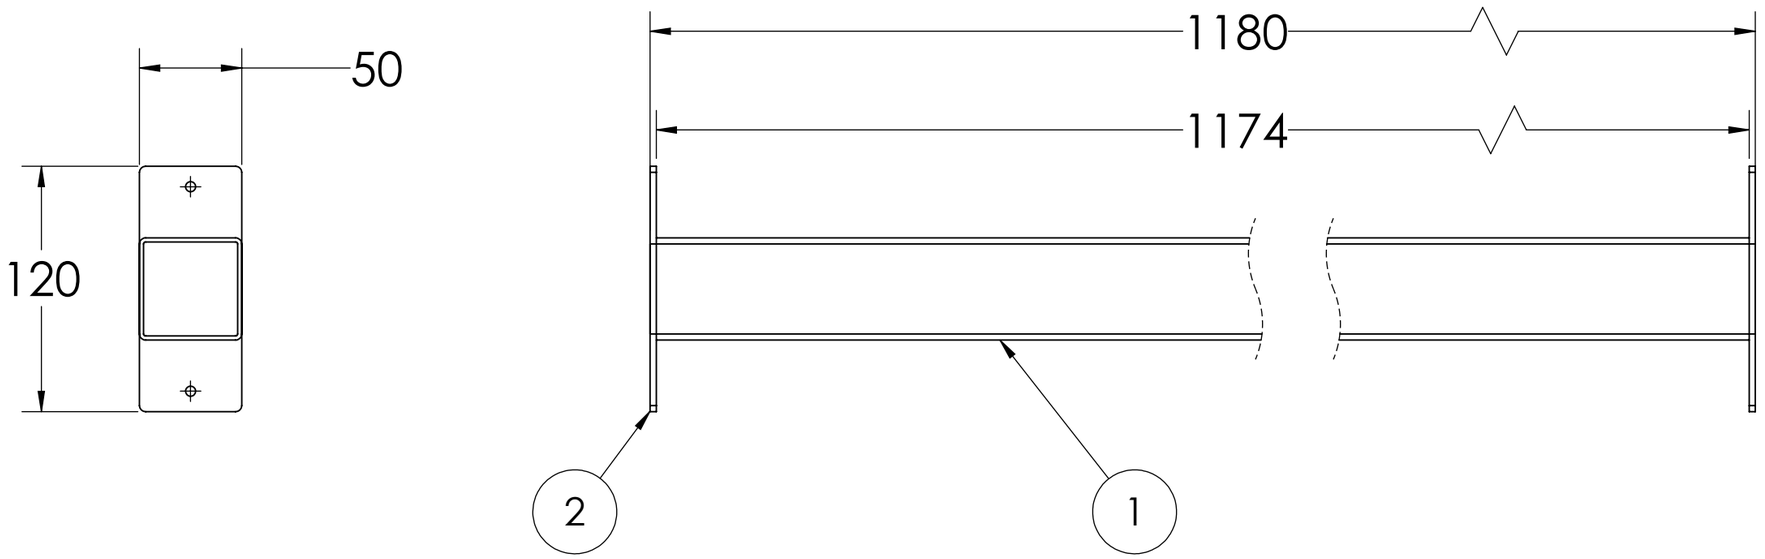

TITLE - INTERMEDIATE SUPPORT				NIHVA TECHNOLOGIES PVT.LTD.PUNE
DWG NO - NTPL189-INTERMEDIATE SUPPORT			QTY - 15	Website - www.nihva.com
	NAME	SIGNATURE	DATE	PROJECT NO - NTPL189
DRAWN	D.V.		16.09.2023	PRODUCT - RETRACTABLE ROOF
CHK'D	P.M.		16.09.2023	
APPV'D	V.T.		16.09.2023	
if any queries contact - operation@nihva.com				REVISION -
ALL DIMENSION ARE IN mm			A3	SCALE - SHEET 1 OF 1