
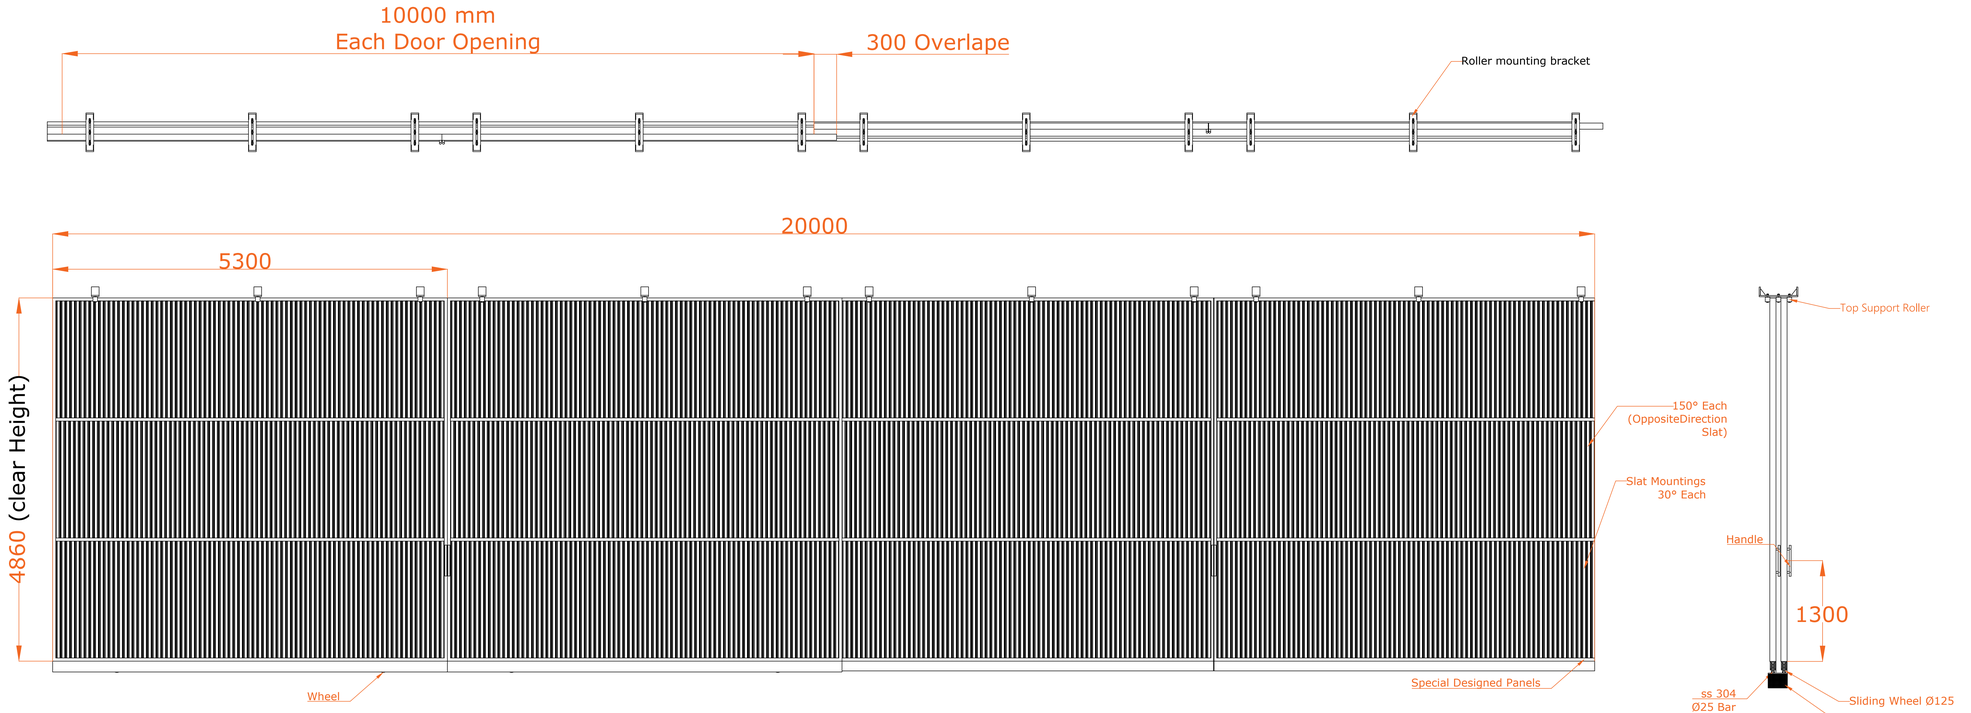


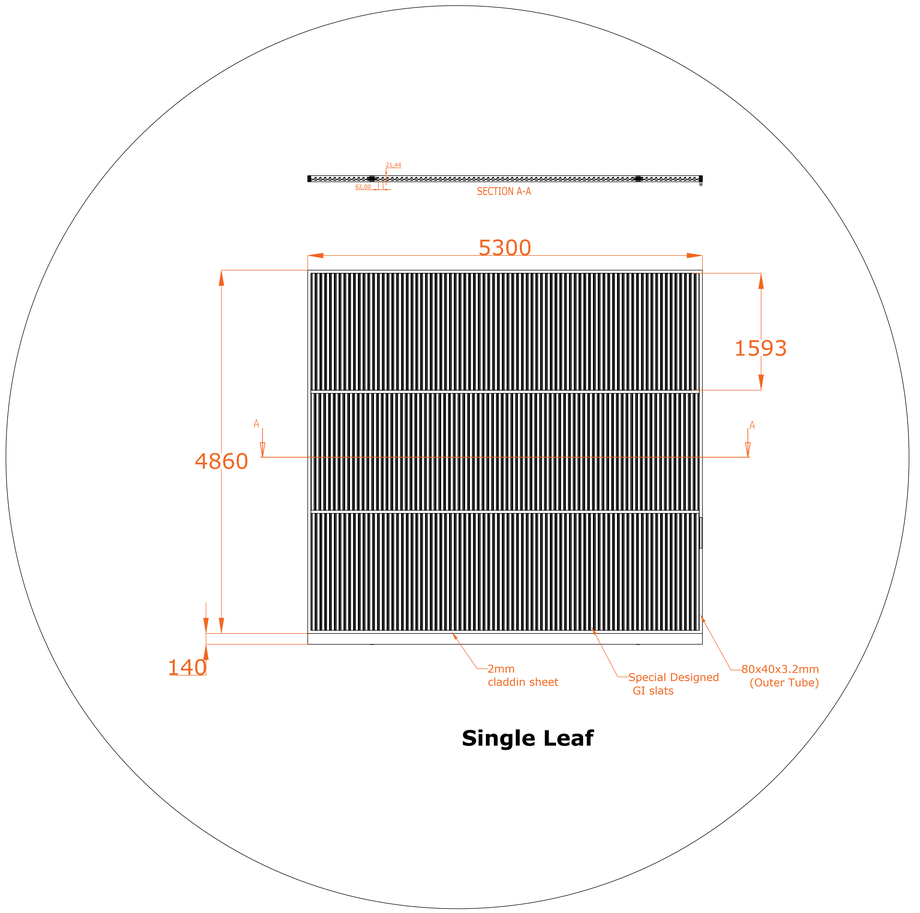

Single Leaf

Shown GA IS ONLY FOR 4 LEAFS
(Total leafs - 14 x 5.3 =70 meter)

TECHNICAL SPECIFICATION:-

SR.	SPECIFICATION	DETAILS
1.	Slat	Straight 80 mm GI Sheet - 1.0 mm Thk.
2.	Leaf Size	5300 mm x 4860mm= 14 qty
3.	Overlap	Overlap considered 300 mm between 2 gates

This drawing & designing is the property of NIHVA TECHNOLOGIES. Not to be sold or copied to any other concern.

TITLE :- Manual Sliding Gate

NIHVA TECHNOLOGIES PVT. LTD. PUNE
Tel : 020 66304033
Email:- info@nihva.com
Website:- www.nihva.com

	NAME	DATE
DRAWN	S.J	13/04/2024
CHECK	B.B	13/04/2024
APPROVAL	V.T.	13/04/2024

CLIENT - Panchashil
PROJECT - Manual Sliding Gate
FORMAT NO - NIHVA-DD-F-03
DWG. NO. : NIHVA/23-24/XX | REV-03
SCALE: NTS | WT: | SHEET: 01 OF 01
ALL DIMENSION ARE IN mm
If any queries contact : design@nihva.com