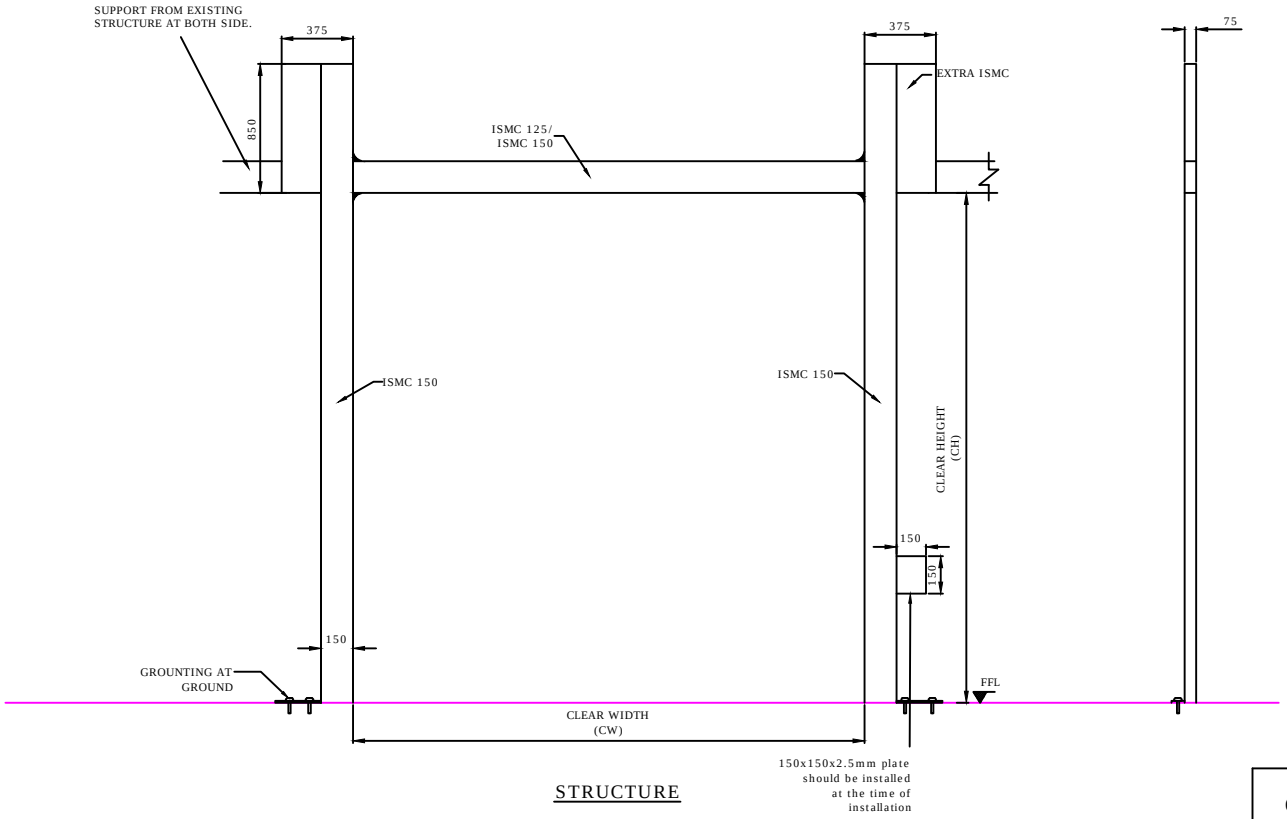

STRUCTURE

SR NO	CLEAR WIDTH(CW)	CLEAR HEIGHT(CH)	QTY	LOCATION
6	6110	6205	1	A-GRET
5	6070	6250	1	G-GRET
4	6070	8000	1	G-19
3	6060	8000	1	H-19
2	6060	8000	1	F-1
1	6070	8000	1	B-1

NOTES-
(1) MS STRUCTURE , FITTING & ALL CIVIL WORK IS IN CLIENT SCOPE.
(2) SHUTTER WILL BE ONLY INSTALLED AFTER READINESS OF STRUCTURE AS PER DRAWING PROVIDED.
(3) SPACE OF 850 mm ABOVE CLEAR HEIGHT IS REQUIRED FOR INSTALLATION OF MOTORIZED ROLLING SHUTTER. IN CASE SPACE IS NOT AVAILABLE , REDUCTION IN CLEAR HEIGHT IS REQUIRED .

This drawing & design is the property of NIHVA TECHNOLOGIES. Not to be sold or copied to any other concern.

TITLE- GI SLAT MOTORIZED ROLLING SHUTTER

NIHVA TECHNOLOGIES PVT. LTD.

NIHVA TECHNOLOGIES PVT. LTD. PUNE
Tel : 020 66304033
Email:- info@nihva.com
Website:- www.nihva.com

	NAME	SIGN	DATE
DRAWN	SIDDHESHWAR		28.11.2020
CHECK	SIDDHESHWAR		28.11.2020
APPRD.			

CLIENT - GS PEB & CIVIL WORKS PVT LTD
PROJECT - SANY HEAVY INDUSTRY INDIA PVT LTD
SITE LOCATION - PUNE

If any queries contact : projectsupport@nihva.com

DWG. NO. : NIHVA/20-21/0098 REV- R00

ALL DIMENSION ARE IN mm

SCALE: NTS WT: SHEET: