THIS PRINT IS THE PROPERTY OF NIHVA IT IS TO BE USED ONLY FOR THE PURPOSE FOR WHICH IT WAS LENT
AND MUST NOT BE USED IN ANY WAY DERTIMENTAL TO THE INTEREST OF THIS COMPANY AND IS SUBJECT TO RETURN ON DEMAND.

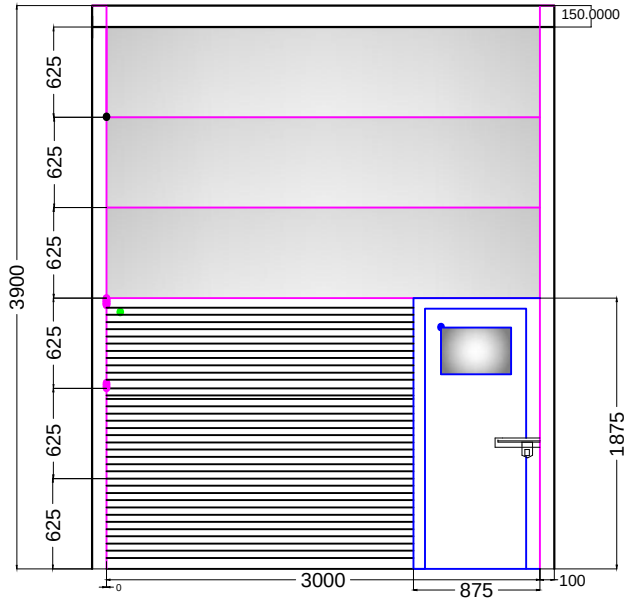

TITLE: WICKET DOOR WITH PUF INSULATED PANNEL.	DO NOT SCALE DRAWING		NIHVA TECHNOLOGIES PVT.LTD
		SIGN	DATE	
CLIENTS APPROVEL:–	DRAWN P.P			CLIENT: SKFPUNE
	CHECK R.K.			PROJECT / SITE:
	ENG			WICKET DOOR WITH PUF INSULATED PANNELS
UNLESS & OTHERWISE SPECIFIED DIMENSION ARE IN M.M.	APPRD.			DWG. NO.:
	PROD			REV.: 0
	MFG			SCALE: NTS WT: SHEET: 1 OF 1
	Ref. No.			