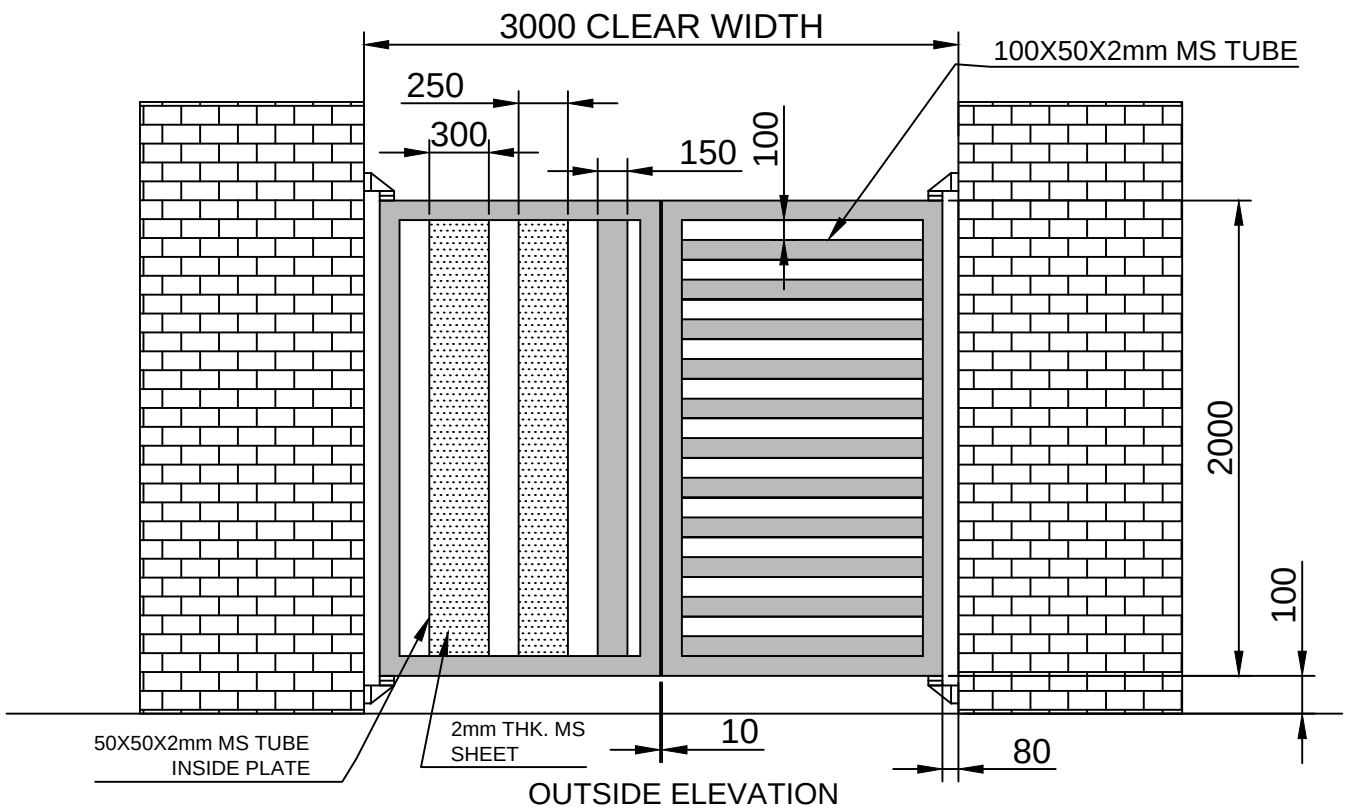

OUTSIDE ELEVATION

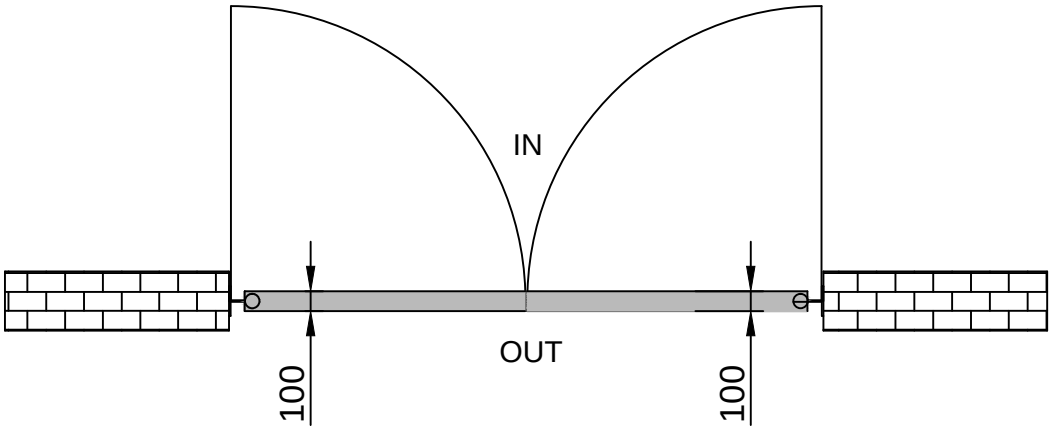

TUBES SPECIFICATION	
SR NO	SIZES
1	100x100x2 mm MS SQ. TUBE
2	100x50x2 mm MS REC. TUBE
3	150x50x3.5 mm MS REC. TUBE
4	50x50x2 mm MS REC. TUBE
5	14 GAUGE MS PERFORATED SHEET

DIMENSION :

CLEAR WIDTH	CLEAR HEIGHT	QUANTITY
3000 mm	2000 mm	1 NOS.

MATERIAL :

THICKNESS :

NOTE: ALL REQUIRED CIVIL WORK WILL BE IN CLIENT'S SCOPE.

NIHVA TECHNOLOGIES PVT. LTD.
NIHVA TECHNOLOGY PVT. LTD. PUNE
Email:- info@nihva.com
Website:- www.nihva.com

TITLE:

SWING GATE

CLIENT'S APPROVAL :

CLIENT - SUROJ BUILDCON PVT. LTD.

PROJECT - KSB

SITE LOCATION - SHIRWAL, MIDC

DWG. NO. : NIHVA/16-17/0072

SCALE: NTS	WT:	SHEET:1 OF 1

DRAWN BY: OMKAR	DATE: 10-09-2016
CHECK : ANIL	DATE: 10-09-2016

If any queries contact : projects@nihva.com

NOTE: ALL DIMENSION ARE IN mm

THIS DRAWING & DESIGNING IS THE PROPERTY OF NIHVA TECHNOLOGIES. NOT BE SOLD OR COPY TO ANY OTHER CONCERN.