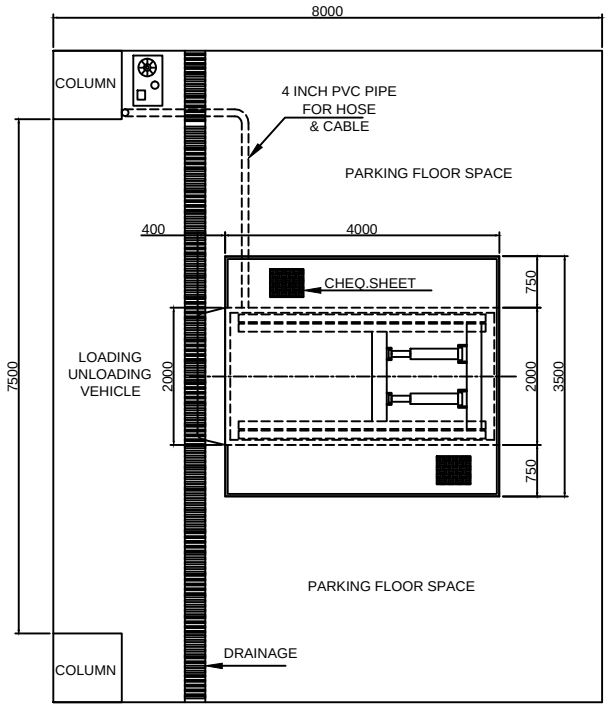

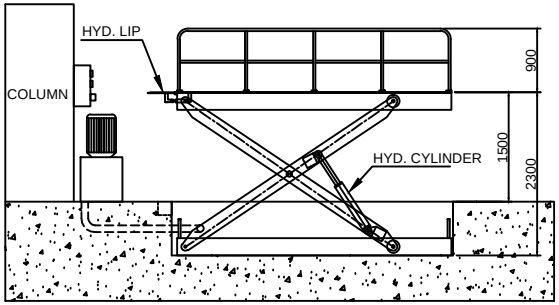

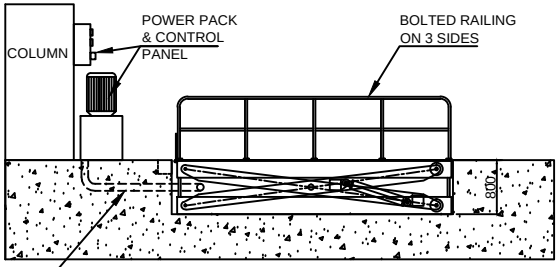

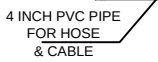

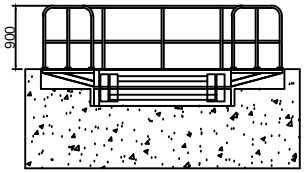

PIT DRAWING

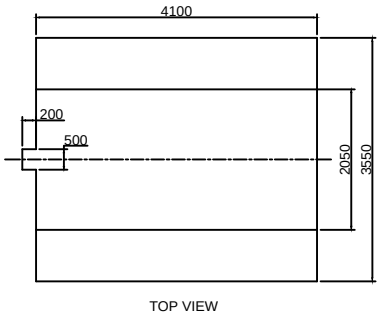

TOP VIEW

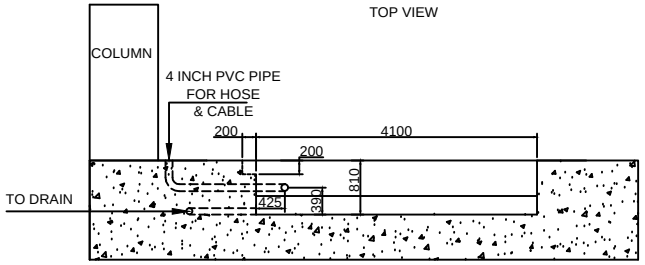

FRONT VIEW

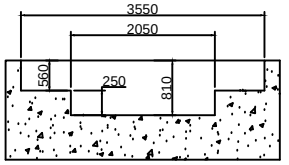

SIDE VIEW

NOTE :
1. HYDRAULIC HOSE LENGTH : 12 MTR
2. ELECTRICAL CABLE : 12 MTR
3. PIT / CIVIL / PVC PIPE WILL BE IN CLIENT SCOPE.
4. COLOR : A. GOLDEN YELLOW.
   B. ULTRA MARINE BLUE.
5. INPUT SUPPLY : 400 VOLT 3 PHASE WITH NEUTRAL.

CAPACITY	4.5 TON
PLATFORM SIZE	4000(L) X 3500(W)
POWER PACK	7.5 HP, 3 PH
SHUT HEIGHT	800 MM
LIFT HEIGHT	1500 MM
OPEN HEIGHT	2300 MM

This drawing & design is the property of NIHVA TECHNOLOGIES. Not to be sold or copied to any other concern.

TITLE
SCISSOR LIFT

NIHVA TECHNOLOGIES PVT. LTD.

NIHVA TECHNOLOGIES
PVT. LTD. PUNE
Tel : 020 66304033
Email:- info@nihva.com
Website:- www.nihva.com

	NAME	SIGN	DATE
DRAWN	P.V.A		13.08.2019
CHECK	V.M.T		13.08.2019
APPRD.			

CLIENT - IKEA
PROJECT - R CITY MALL
SITE LOCATION - MUMBAI
If any queries contact : design@nihva.com
DWG. NO. : NIHVA/19-20/0076
REV- 0
ALL DIMENSION ARE IN mm
SCALE: NTS
WT:
SHEET: 01 OF 01