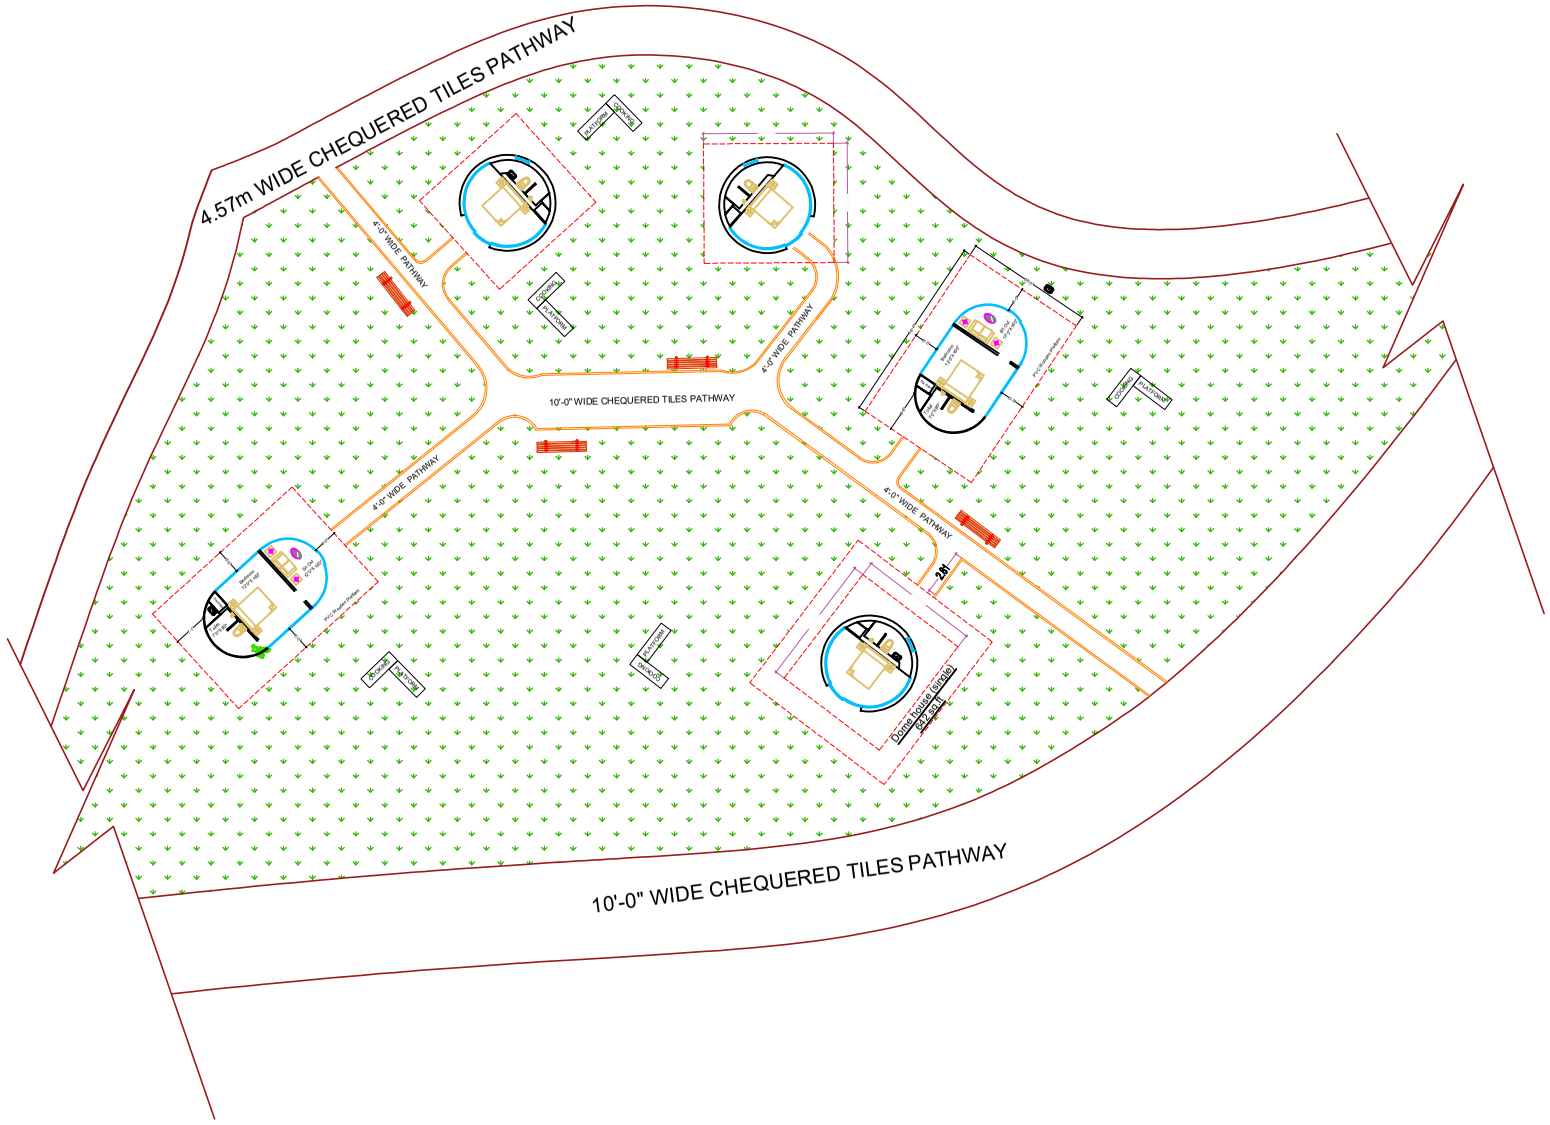


REV.	DESCRIPTION	DATE	BY

NOTES:–

SHALL BE FOLLOWED.

2. ±0.00 LEVEL CORRESPONDS TO PLINTH LEVEL(P.L.) OF BUILDING. WHICH IS 1050mm IN ABSOLUTE GROUND LEVEL(G.L.).
3. ALL RCC WORK SHALL BE OF M25 GRADE CONCRETE.
4. BRICKWORK SHALL BE WITH 100A BRICKS IN CEMENT MORTAR 1:6.

PROJECT	PROPOSED DEVELOPMENT OF MAJHAR KUND SASARAM RANGE, ROHTAS DIVISION
DEPT.	ENVIRONMENT AND FOREST DEPARTMENT ROHTAS, BIHAR
CONSULT.	SHAMAR STRUCTURE SOLUTIONS PVT. LTD. PATNA

CHECKED & APPROVED		Multiple Polycarbonate dome house	
DESIGN BY	Ar. NITISH		
DRAWN BY			
SIZE-A1	SCALE 1:100	DATE - 20.10.2023	SHEET 11 OF 11 / REV R=0