


TERRACE FLOOR PLAN

FRONT BUILDING

SCALE:- 1:50

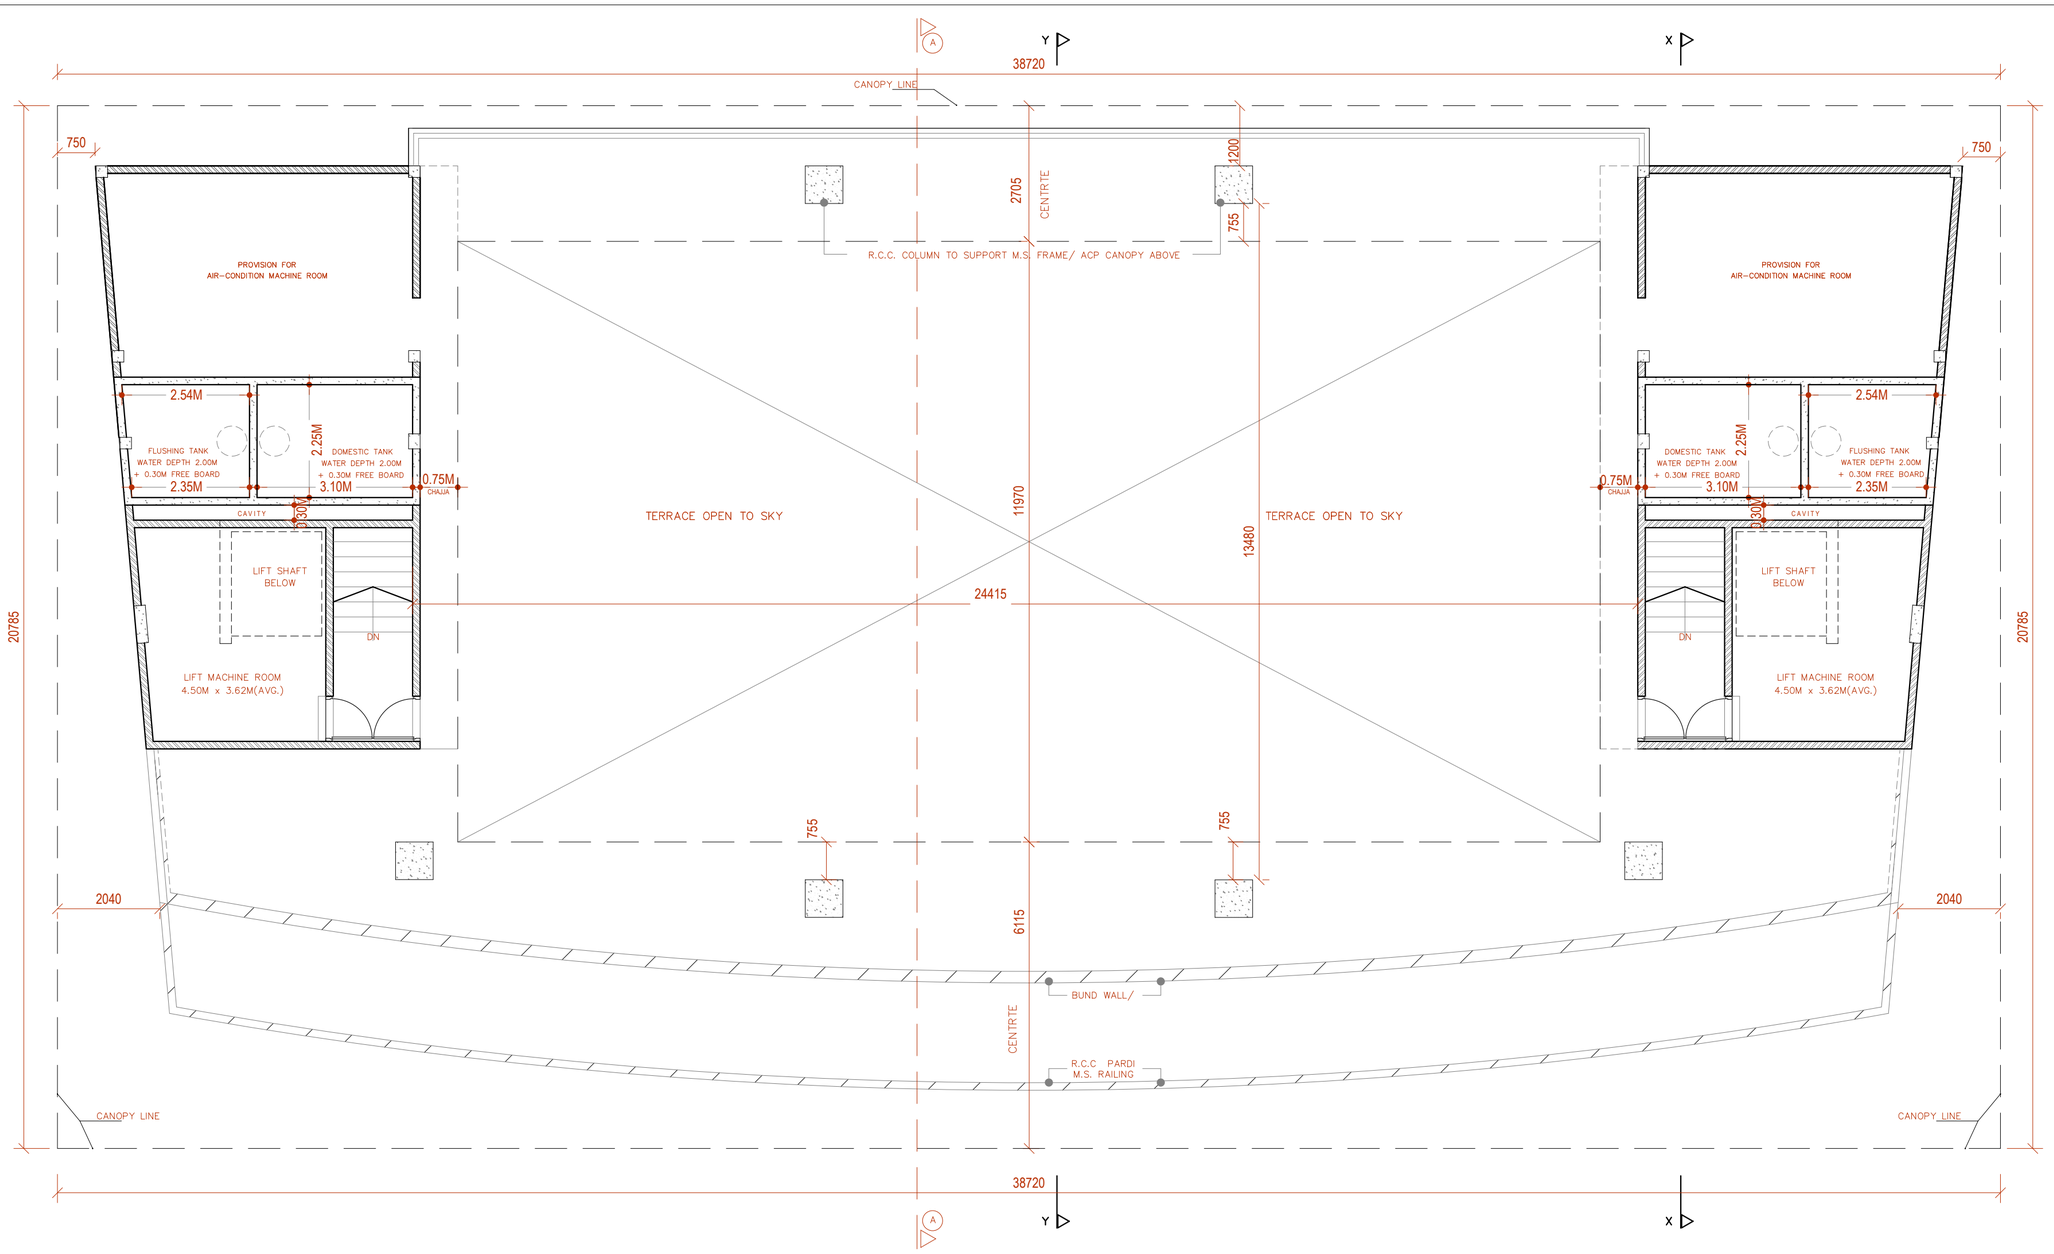

A. GENERAL NOTES

01 ALL DIMENSIONS ARE IN METER UNLESS SPECIFIED OTHERWISE.
02 ALL DIMENSIONS AND LEVELS ARE TO BE CHECKED AND VERIFIED BY THE SITE ENG. BEFORE EXECUTION.
03 ALL THE WORK SHOULD BE CARRIED OUT AS PER SPECIFICATIONS AND INSTRUCTIONS GIVEN BY THE ARCHITECTS.
04 ANY DESCRIPANCY IN THIS DRAWING SHOULD BE BROUGHT TO THE IMMEDIATE NOTICE OF THE ARCHITECTS OR STRUCTURAL ENGINEERS.
05 ALL INTERNAL WALLS ARE 115MM THICK EXCLUDING PLASTERING AND EXTERNAL WALLS 125MM THK EXCLUDING PLASTER.
06 THIS DRAWING IS A COPYRIGHT AND MUST NOT BE USED OR DISCLOSED OR REPRODUCED IN ANY OTHER FORM WITHOUT EXPRESS PERMISSION OF DUMASIA DESAI NANDANI ARCHITECTS

B. SPECIAL NOTES

01 ALL PROJECTIONS TO BE CHECKED WITH ARCHITECTS DRAWING AND TO BE VERIFIED OR ADJUSTED ON SITE IN CONJUNCTION WITH THE STRUCTURAL DRAWINGS.
02 THIS DRAWING IS TO BE READ IN CONJUCTION WITH THE R.C.C. CONSULTANTS DRAWING.

C. REVISIONS

REV. NO.	DESCRIPTION	DATE	SIGN
R1			
R2			
R3			

PROJECT :
PROPOSED INFORMATION TECHNOLOGY BUILDING KNOWN AS 'FLEXCEL-PARK', ON PLOT BEARING C.T.S. NO. 217/1 TO 7 S.V. ROAD, JOGESHWARI(WEST), MUMBAI 400102


FOR M/S EXCEL INDUSTRIES LTD.

TITLE
TERRACE PLAN SHOWING O.H. TANK, LIFT MACHINE RM., A.C. RM.

I N D E X

JOB : EXCEL	DRG NO. WD/EXC/13(REVISED)
SCALE : 1 = 50	
DATE : 14-03-08	CADFILE :- PRANAV/DDN/BANDIVALI/WD/PLAN.DWG
DRN : PRANAV	
CHKD : P N D	LOCATION :

DUMASIA DESAI NANDANI ARCHITECTS
ARCHITECTS ENGINEERS & VALUERS
402, SAI CHAMBERS,OPP.RLY.STN.
NEHRU ROAD,SANTACRUZ (E).
MUMBAI-400 055

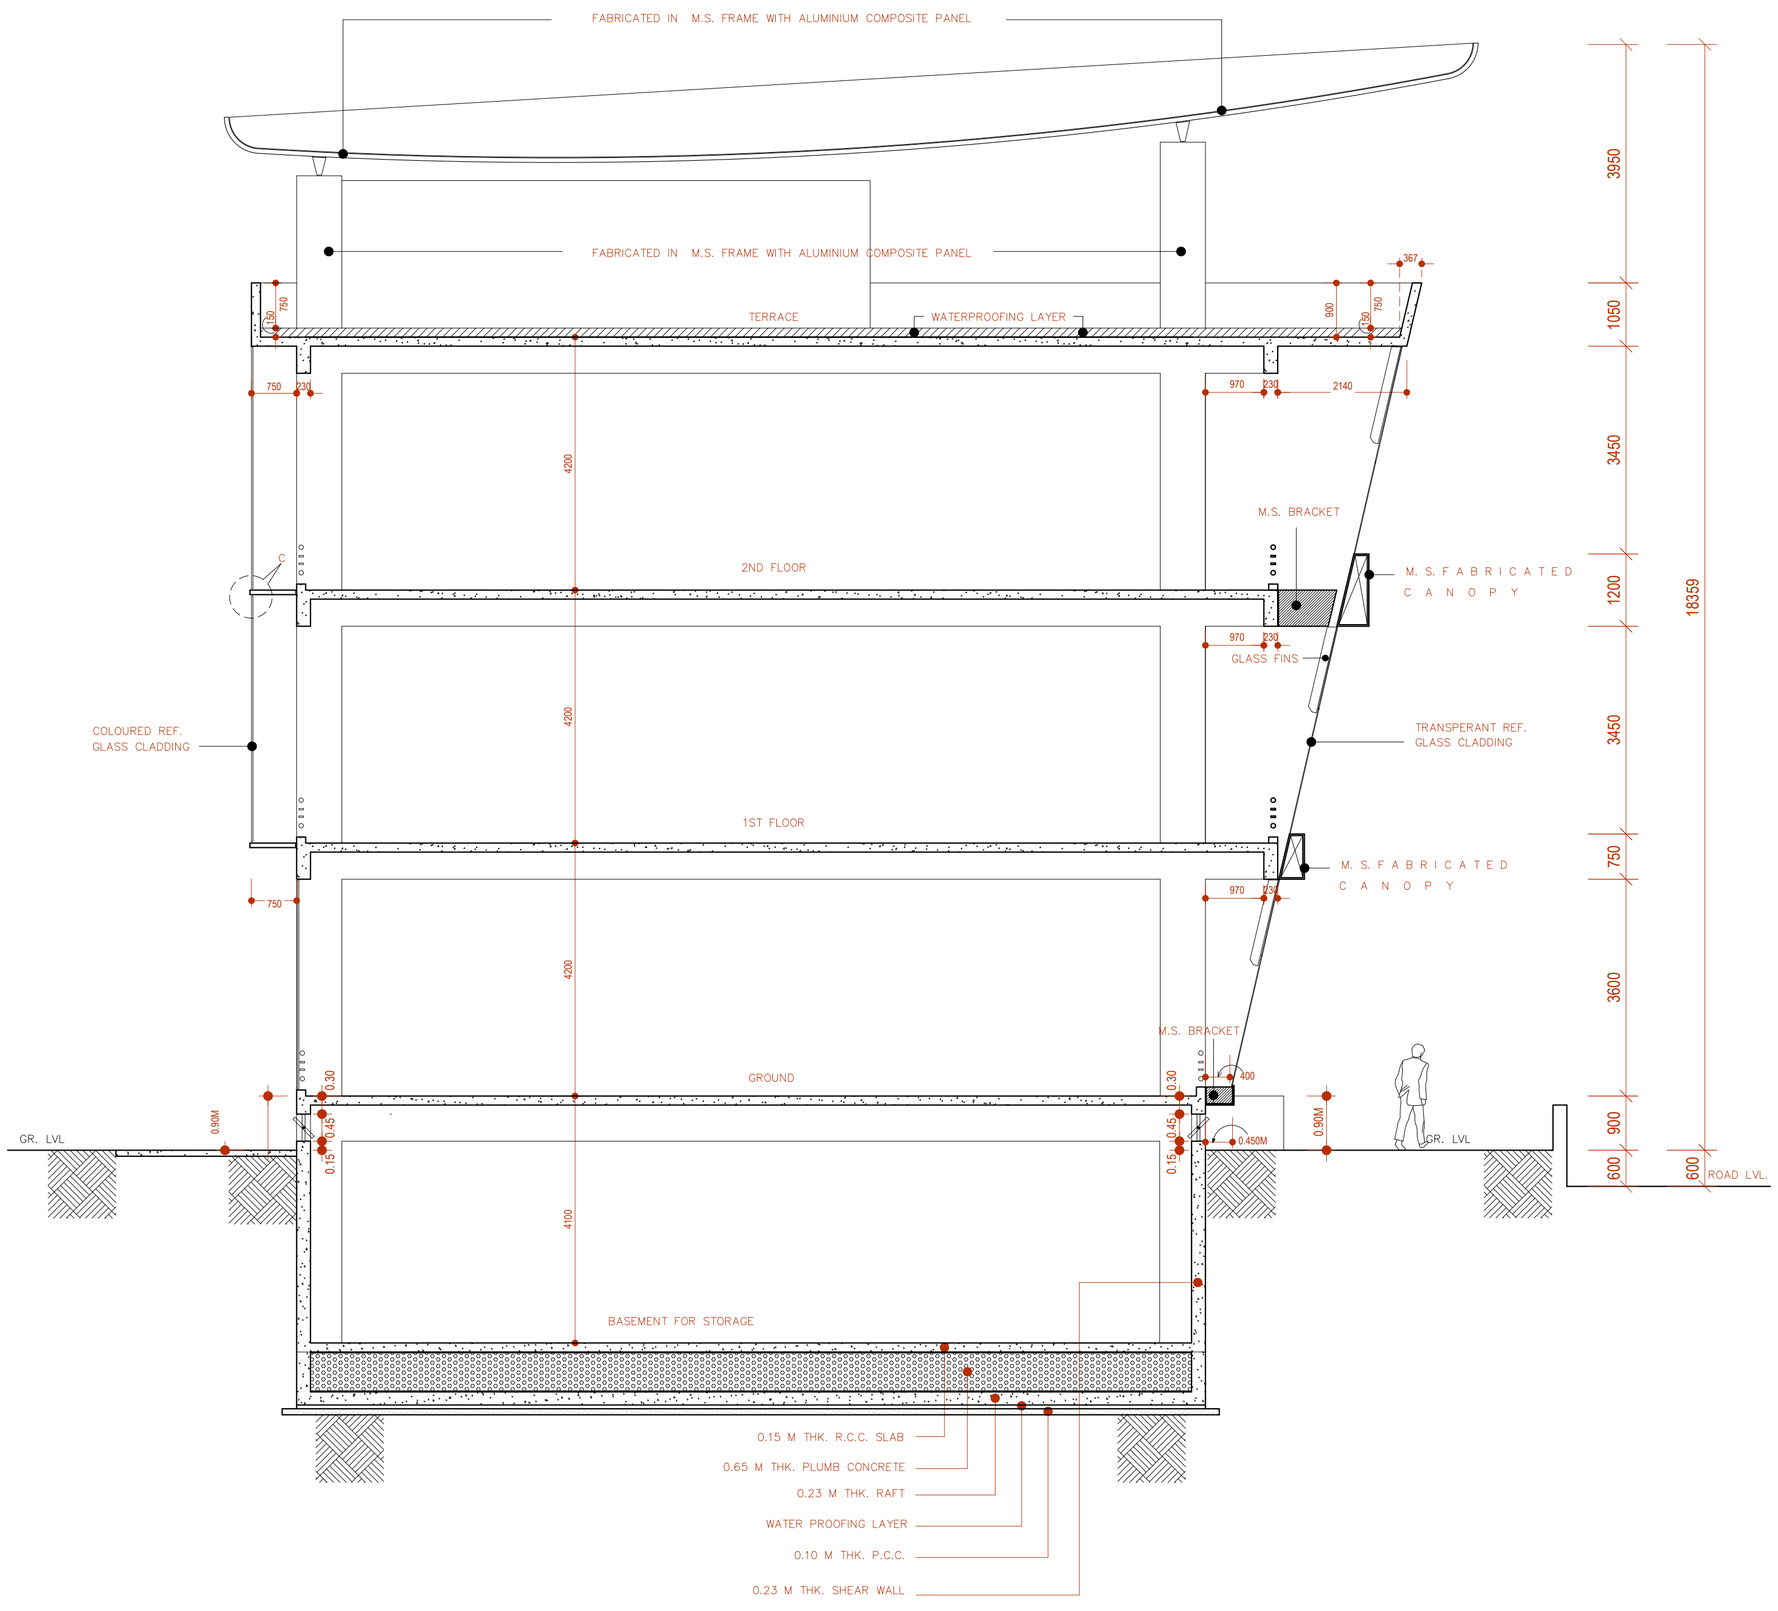

CROSS SECTION A–A

A. GENERAL NOTES

01 ALL DIMENSIONS ARE IN METER UNLESS SPECIFIED OTHERWISE.

02 ALL DIMENSIONS AND LEVELS ARE TO BE CHECKED AND VERIFIED BY THE SITE ENG. BEFORE EXECUTION.

03 ALL THE WORK SHOULD BE CARRIED OUT AS PER SPECIFICATIONS AND INSTRUCTIONS GIVEN BY THE ARCHITECTS.

04 ANY DESCRIPANCY IN THIS DRAWING SHOULD BE BROUGHT TO THE IMMEDIATE NOTICE OF THE ARCHITECTS OR STRUCTURAL ENGINEERS.

05 ALL INTERNAL WALLS ARE 115MM THICK EXCLUDING PLASTERING AND EXTERNAL WALLS 125MM THK EXCLUDING PLASTER.

06 THIS DRAWING IS A COPYRIGHT AND MUST NOT BE USED OR DISCLOSED OR REPRODUCED IN ANY OTHER FORM WITHOUT EXPRESS PERMISSION OF DUMASIA DESAI NANDANI ARCHITECTS

B. SPECIAL NOTES

01 ALL PROJECTIONS TO BE CHECKED WITH ARCHITECTS DRAWING AND TO BE VERIFIED OR ADJUSTED ON SITE IN CONJUNCTION WITH THE STRUCTURAL DRAWINGS.

02 THIS DRAWING IS TO BE READ IN CONJUCTION WITH THE R.C.C. CONSULTANTS DRAWING.

C. REVISIONS

REV. NO.	DESCRIPTION	DATE	SIGN
R1			
R2			
R3			

PROJECT :
PROPOSED INFORMATION TECHNOLOGY BUILDING KNOWN AS 'FLEXCEL–PARK', ON PLOT BEARING C.T.S. NO. 217/1 TO 7 S.V. ROAD, JOGESHWARI(WEST), MUMBAI 400102

FOR M/S EXCEL INDUSTRIES LTD.

TITLE
CROSS SECTION A–A

I N D E X

JOB : EXCEL	DRG NO. WD/EXC/08
SCALE : 1 = 50	
DATE : 03–08–06	CADFILE :– PRANAV/DDN/BANDIVALI/WD/PLAN.DWG
DRN : PRANAV	
CHKD : P N D	LOCATION :

DUMASIA DESAI NANDANI ARCHITECTS
ARCHITECTS ENGINEERS & VALUERS
402, SAI CHAMBERS,OPP.RLY.STN. NEHRU ROAD,SANTACRUZ (E), MUMBAI–400 055