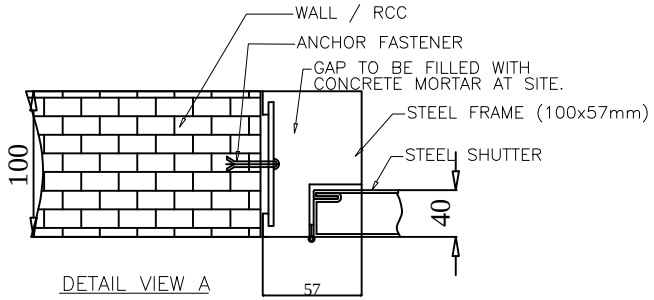

DETAIL VIEW A

NOTES:–

ALL DIMENSIONS ARE IN MM.

NOTES:–

ALL DIMENSIONS ARE IN MM.

A. ABBREVIATION

Wall Opening Width : WOW
Wall Opening Height : WOH
Frame Opening Height : FOH
Frame Opening Width : FOW
Shutter Opening Height : SOH
Shutter Opening Width : SOW

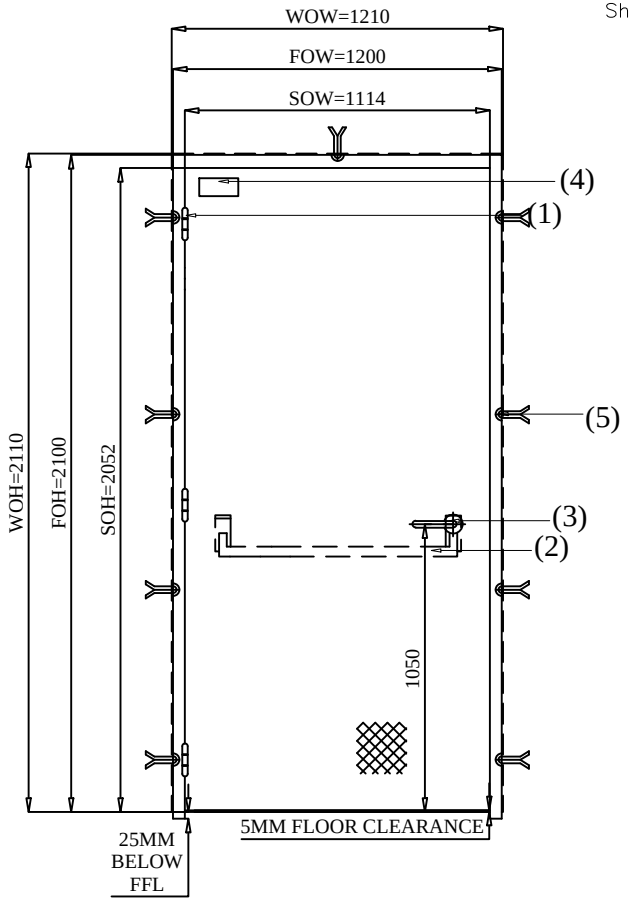

MATERIAL OF CONSTRUCTION

FRAME : G.I. 1.20mm Sheet
SHUTTER : G.I. 0.80mm Sheet

THICKNESS : 40MM

FRAME PROFILE : 100 x 57Mm (Single Ribet)

INFILL MATERIAL : MINERAL WOOL
DENSITY 48kg/cm3

PAINT: AS PER AS APPROVED RAL SHADE
POWDER COATED (DFT 80 Microns min)

SCHEDULE OF HARDWARE

1) S.S. Ball Bearing Hinges (GEZE MAKE) - 3 NOS .
2) Panic Bar for Single Leaf Door - YALE MAKE - 1 Nos.
3) External Trim Bar (Panic Latch) - Yale Make -1 Nos.
4) Heavy Duty Door Closer GEZE MAKE -1 Nos
5) Anchor Fastener - 8 x 80MM.

DATE	REV.	STATUS	PARTICULARS	BY	CHKD.	APPD.

REVISIONS.

STATUS CODE: 1:PRELIMINERY COPY 2:FOR REVIEW 3:FOR MATERIAL PROCUREMENT
4:FOR APPROVAL 5:APPROVED FOR CONSTRUCTION

THIS DESIGNED OR DRAWING IS THE PROPERTY OF RADIANT SAFEDOORS PVT. LTD. IT IS SUBJECT TO THEIR RECALL, AND MUST NOT BE LENT,COPIED OR REPRODUCED WITHOUT THEIR WRITTEN PERMISSION.

APPROVED FOR CONSTRUCTION BY.:–

	SIGN	DATE
DRAWN. BY		04/01/2019
CHKD. BY		04/01/2019
APPD. BY		04/01/2019

CLIENT : M/S. Nihva Technologies Pvt Ltd
SITE :

QTY. 28 Nos

TITLE: SINGLE LEAF GENERAL STEEL DOOR WITH PANIC BAR

PROJECTION

SCALE N.T.S.

RADIANT SAFEDOORS PVT. LTD.
WORKS : 539, PHASE II, VATVA GIDC, AHMEDABAD.

DRG. NO. RSPL/190402/01