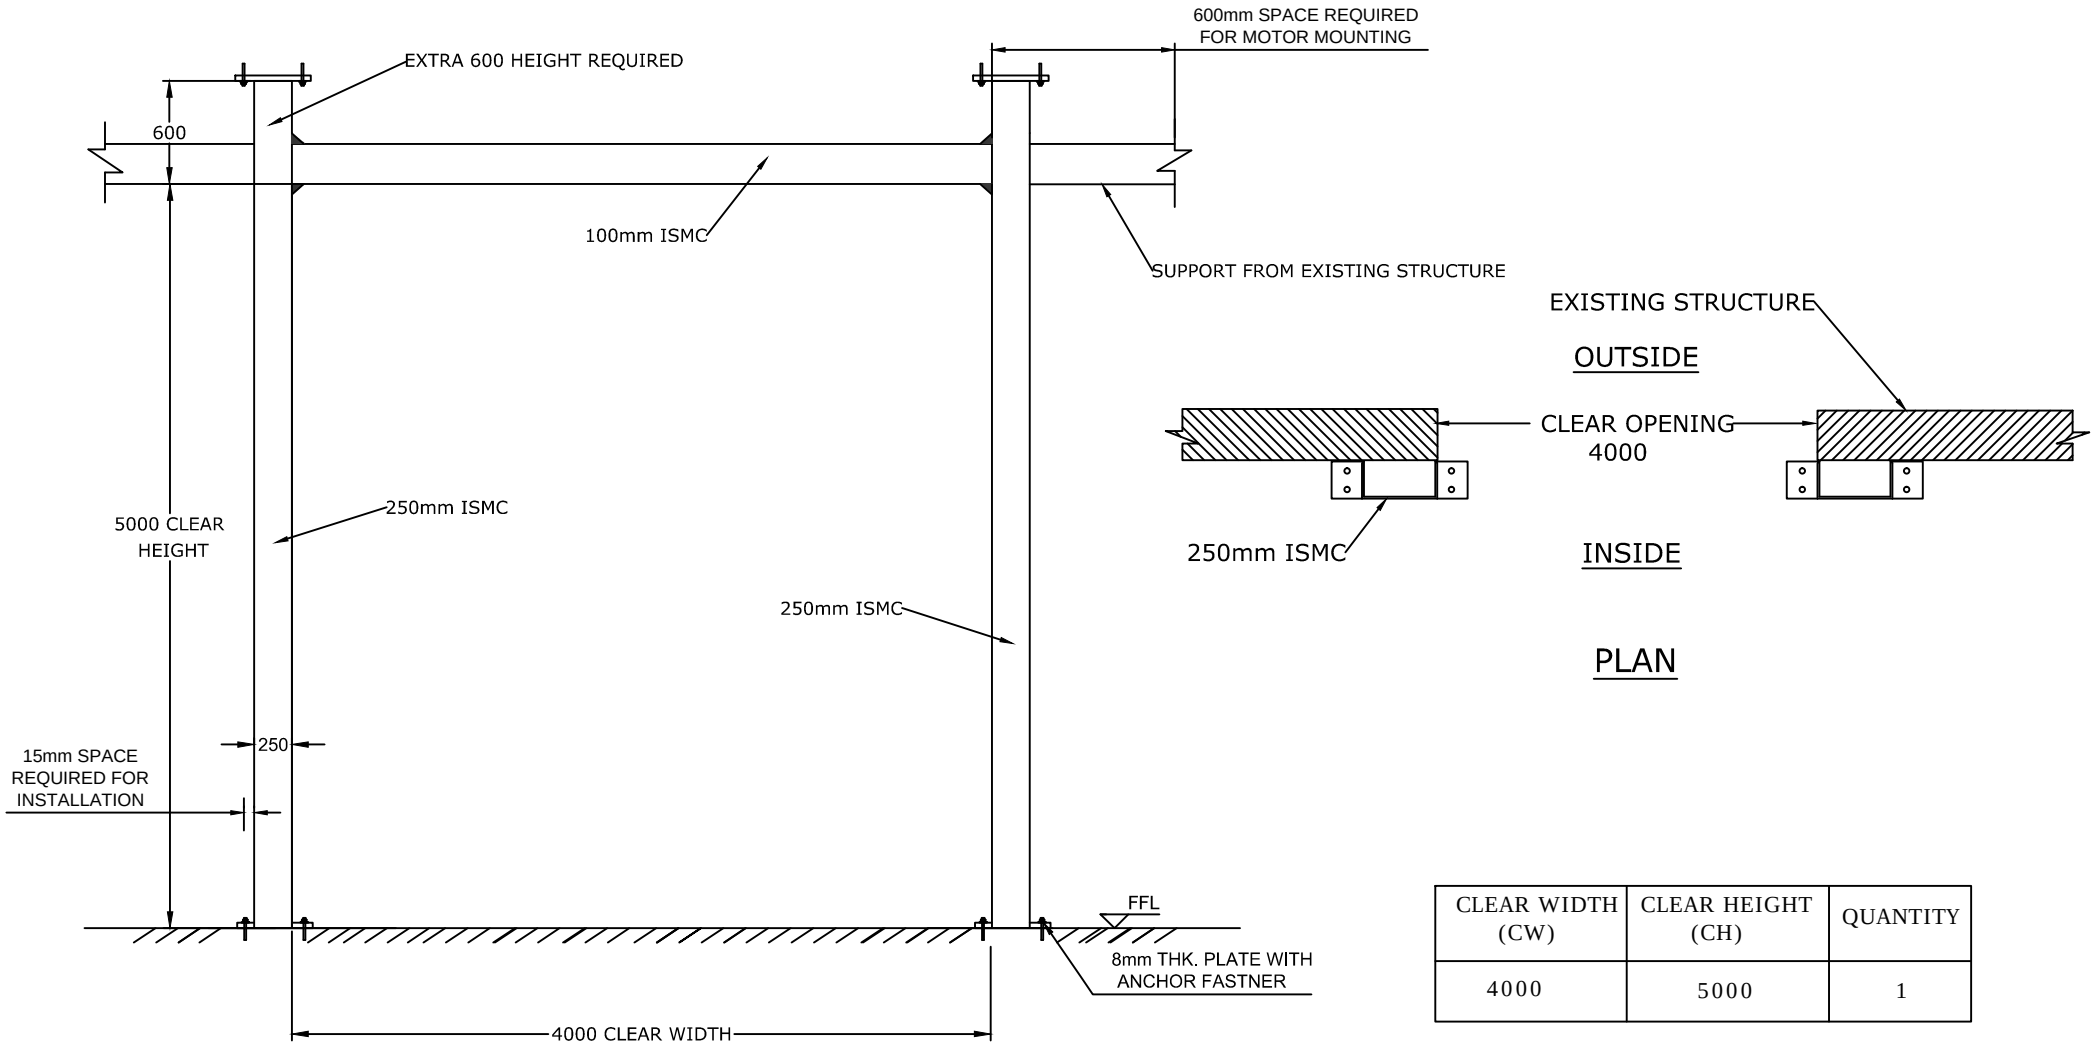


CLEAR WIDTH (CW)	CLEAR HEIGHT (CH)	QUANTITY
4000	5000	1

structure should be bear approx. 800 k.g. weight. (wind pressure included)

This drawing & designing is the property of NIHVA TECHNOLOGIES. Not be sold or copy to any other concern.

TITLE

STRUCTURE FOR HIGH SPEED DOOR (RR 392)

CLIENT APPROVAL

ALL DIMENSION ARE IN mm

NIHVA TECHNOLOGIES PVT. LTD.

NIHVA TECHNOLOGY PVT. LTD. PUNE
Tel : 020 66304033
Email:- info@nihva.com
Website:- www.nihva.com

	SIGN	DATE
DRAWN	OMKAR	19/09/16
CHECK	ANIL	19/09/16
ENG		
APPRD.		
MFG		
Ref. No.		

CLIENT - EagleBurgmann India PVT LMD

PROJECT-

SITE - Hadapsar,Pune

DWG. NO. - NIHVA/16-17/0077

SCALE: NTS | WT: | SHEET: 01

If any queries contact : projects@nihva.com