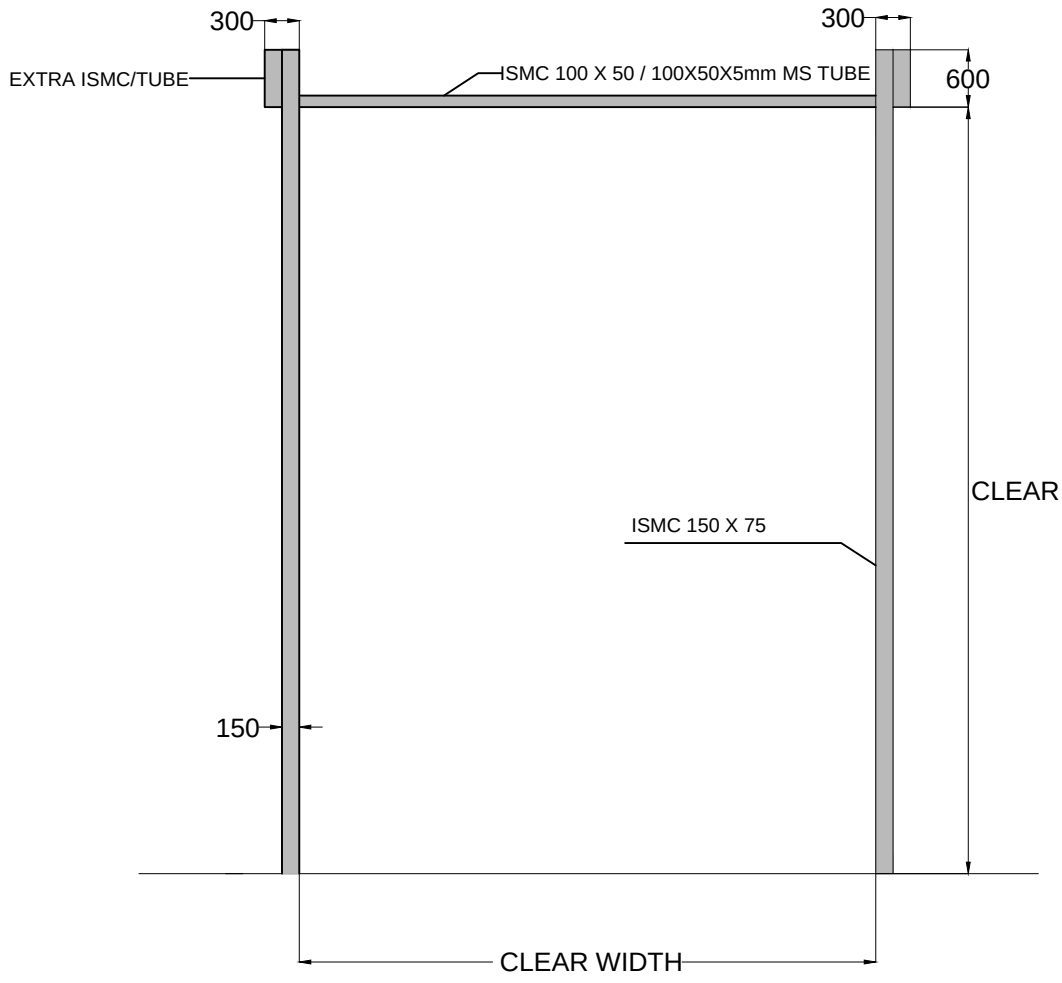


CLEAR WIDTH	CLEAR HEIGHT	QTY.
4000mm	5000mm	01NOS
2500mm	3000mm	03NOS

TOLERANCE - ±10mm

NOTE :

1. MATERIAL FOR ALL STRUCTURE = M.S

This drawing & design is the property of NIHVA TECHNOLOGIES. Not to be sold or copied to any other concern.

TITLE

STRUCTURE FOR GEAR OPERATED ROLLING SHUTTER

NIHVA TECHNOLOGIES PVT. LTD.

NIHVA TECHNOLOGIES PVT. LTD. PUNE
Tel : 020 66304033
Email:- info@nihva.com
Website:- www.nihva.com

	NAME	SIGN	DATE
DRAWN	SURAJ		18-12-2018
CHECK	PRADEEP		18-12-2018
APPRD.	R.D		18-12-2018

CLIENT - SYNERGY

PROJECT-EMBASSY INDUSTRIAL PARKS PVT. LTD.

SITE LOCATION - CHAKAN

If any queries contact : design@nihva.com

DWG. NO. : NIHVA/17-18/0213 | REV- 00

ALL DIMENSION ARE IN mm | SCALE: NTS | WT: | SHEET: 01 OF 01