
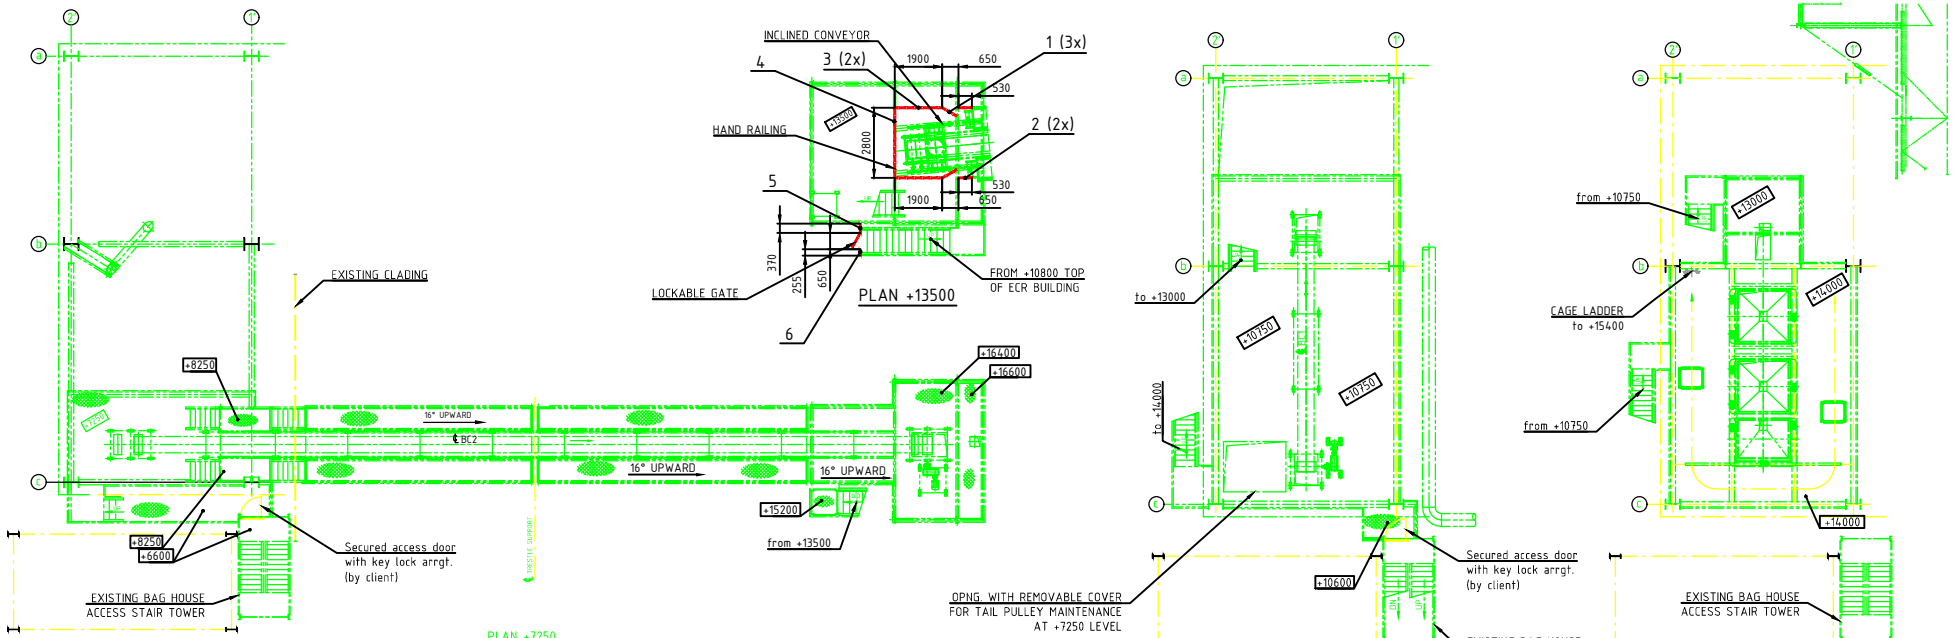


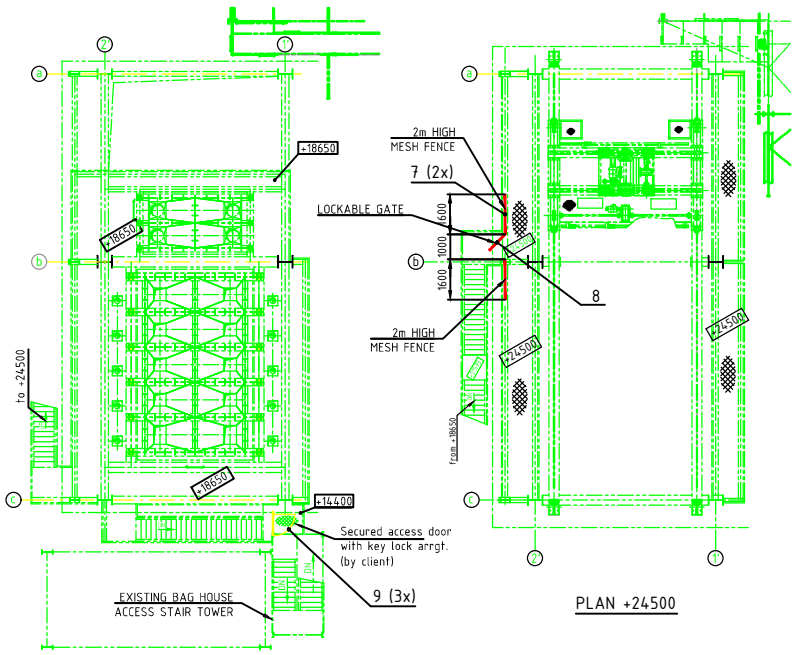

ITEM NO.	DESCRIPTION	QTY.
1	LOCKABLE GATE – W=650 x 2 Mtr. HEIGHT	3
2	MESH FENCE – 530 x 2 Mtr. HEIGHT	2
3	MESH FENCE – 1900 x 2 Mtr. HEIGHT	2
4	MESH FENCE – 2800 x 2 Mtr. HEIGHT	1
5	MESH FENCE – 370 x 2 Mtr. HEIGHT	1
6	MESH FENCE – 255 x 2 Mtr. HEIGHT	1
7	MESH FENCE – 1600 x 2 Mtr. HEIGHT	2
8	LOCKABLE GATE – W=1000 x 2 Mtr. HEIGHT	1
9	SECURED ACCESS DOOR WITH KEY LOCK ARRGT. W=850 x 2 Mtr. HEIGHT	3