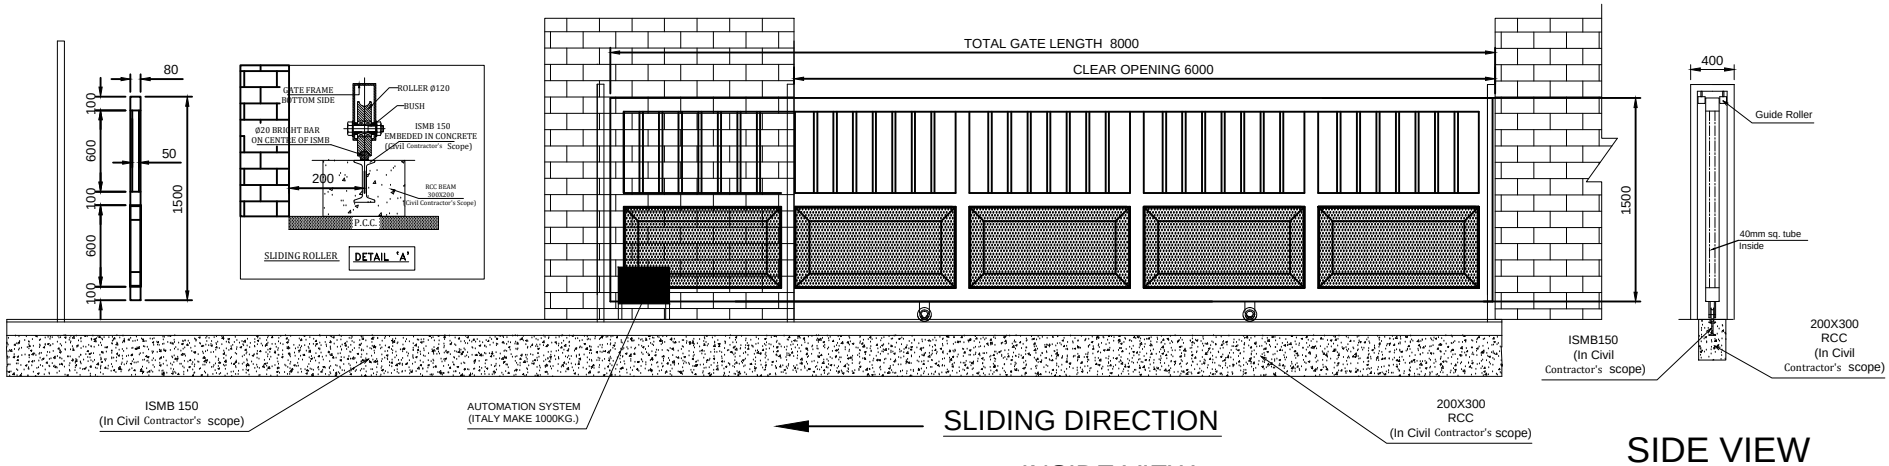
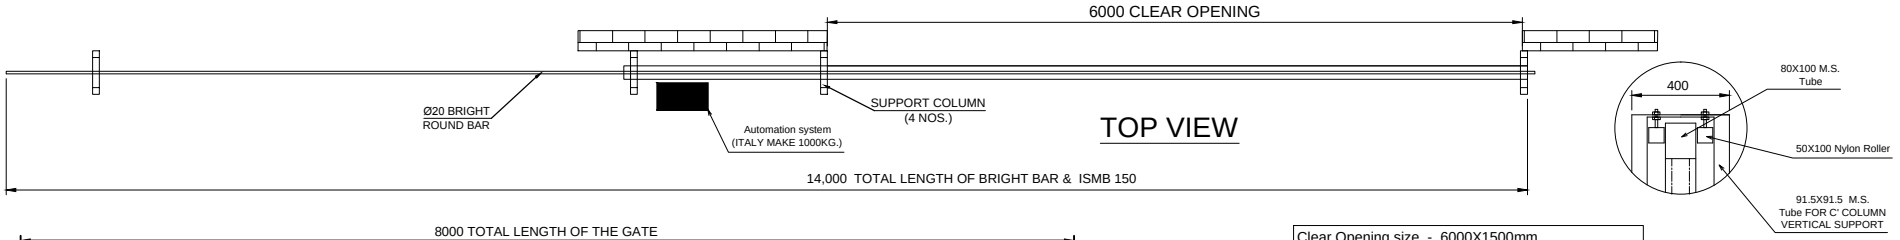
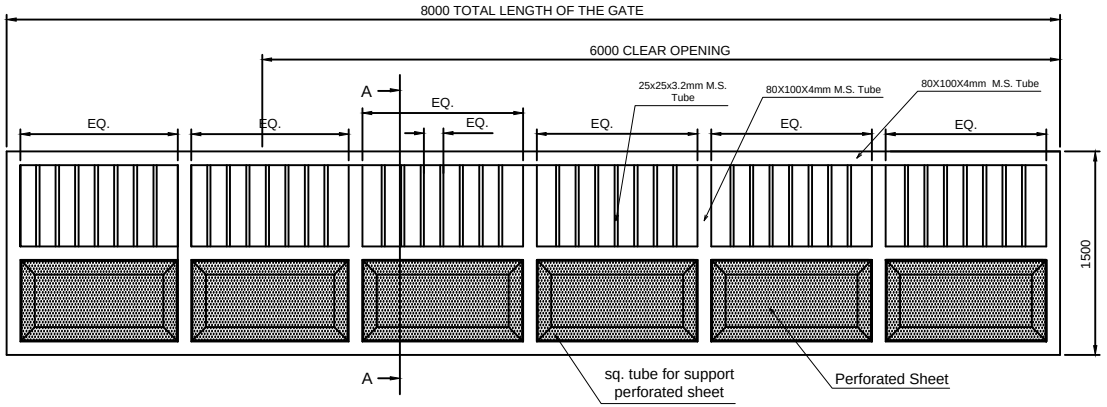



Clear Opening size - 6000X1500mm
Total length of gate - 8000X1500mm
No. Of Column - 4 nos.
Factory paint finish - Red oxide primer coat
NOTE :- *ALL REQ. CIVIL WORK WILL BE IN YOUR CONTRACTOR'S SCOPE.

☑ FINAL CERTIFIED

This drawing & designing is the property of NIHVA TECHNOLOGIES. Not be sold or copy to any other concern.

| TITLE | MOTORIZED SLIDING GATE | | |
|---|---|---|---|
| | SIGN | DATE | |
| DRAWN | ABHIJIT | 28/10/15 | CLIENT - REWARD CONSTRUCTION |
| CHECK | ANIL | 28/10/15 | PROJECT - GIVAUDAN |
| REV. | 03 | | SITE - RANJANGAON MIDC |
| APPROVAL | | | DWG. NO. : NIHVA/15-16/105 |
| If any queries contact : projects@nihva.com | | | SCALE: 01 / WT: / SHEET: 01 OF 01 |
| ALL DIMENSION ARE IN mm | | | |

NIHVA TECHNOLOGIES PVT. LTD.
NIHVA TECHNOLOGY PVT. LTD. PUNE
Tel : 020 66304033
Email:- info@nihva.com
Website:- www.nihva.com