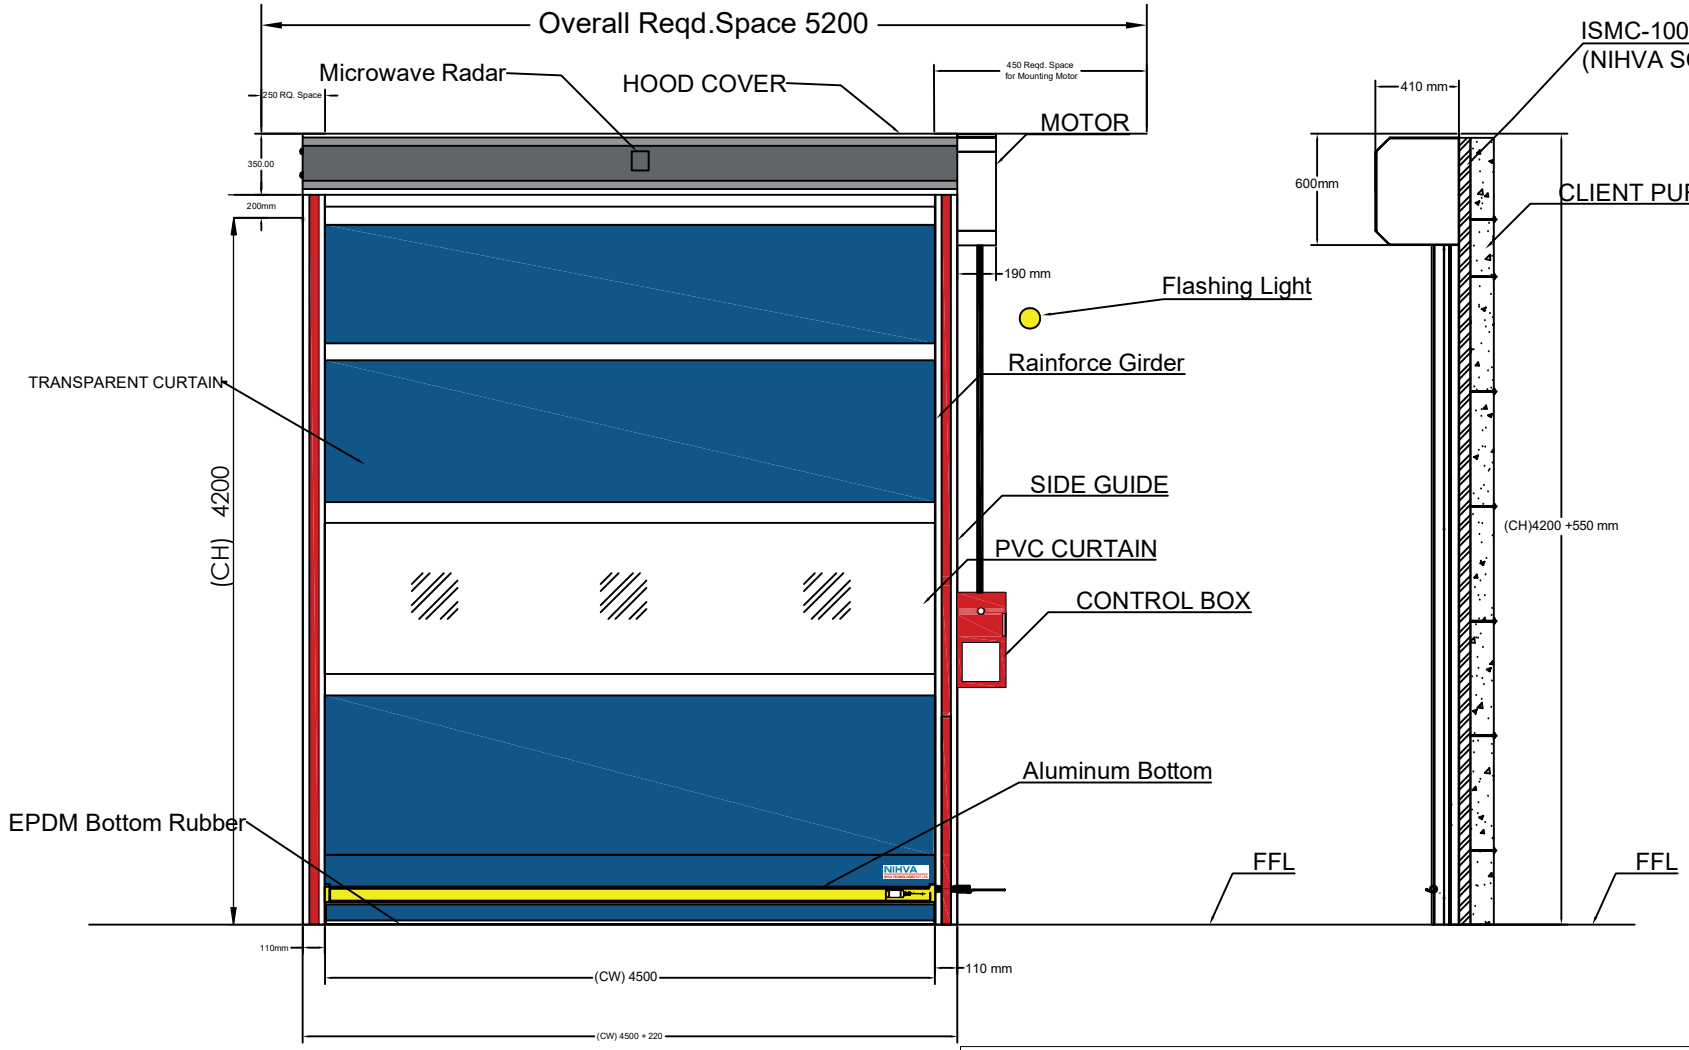


NOTE: (1) REQUIRED M.S. TECHNICAL STRUCTURE & FITTING FOR HSD IS IN NIHVA SCOPE)

(2) ALL CIVIL WORK IN CLIENT SCOPE

Sr	Description	Clear Width (CW)	Clear Height (CH)	QTY
1	HSD With Sensor	**4500**	**4200**	1

This drawing & design is the property of NIHVA TECHNOLOGIES. Not to be sold or copied to any other concern.

TITLE HIGH SPEED DOOR GA DRAWING

	NAME	SIGN	DATE
DRAWN	S.J		18.01.2024
CHECK	A.K		18.01.2024
APPRD.	V.T		18.01.2024

If any queries contact : projectsupport@nihva.com

ALL DIMENSION ARE IN mm

NIHVA TECHNOLOGIES PVT. LTD.

NIHVA TECHNOLOGIES PVT. PUNE
Tel : 020 66304033
Email:- info@nihva.com
Website:- www.nihva.com


CLIENT - RINAC

PROJECT - HIGH SPEED DOOR

FORMAT NO - NIHVA-DD-F-03

DWG. NO. : NIHVA/23-24/00XX | REV- R00

SCALE: NTS | WT: | SHEET:

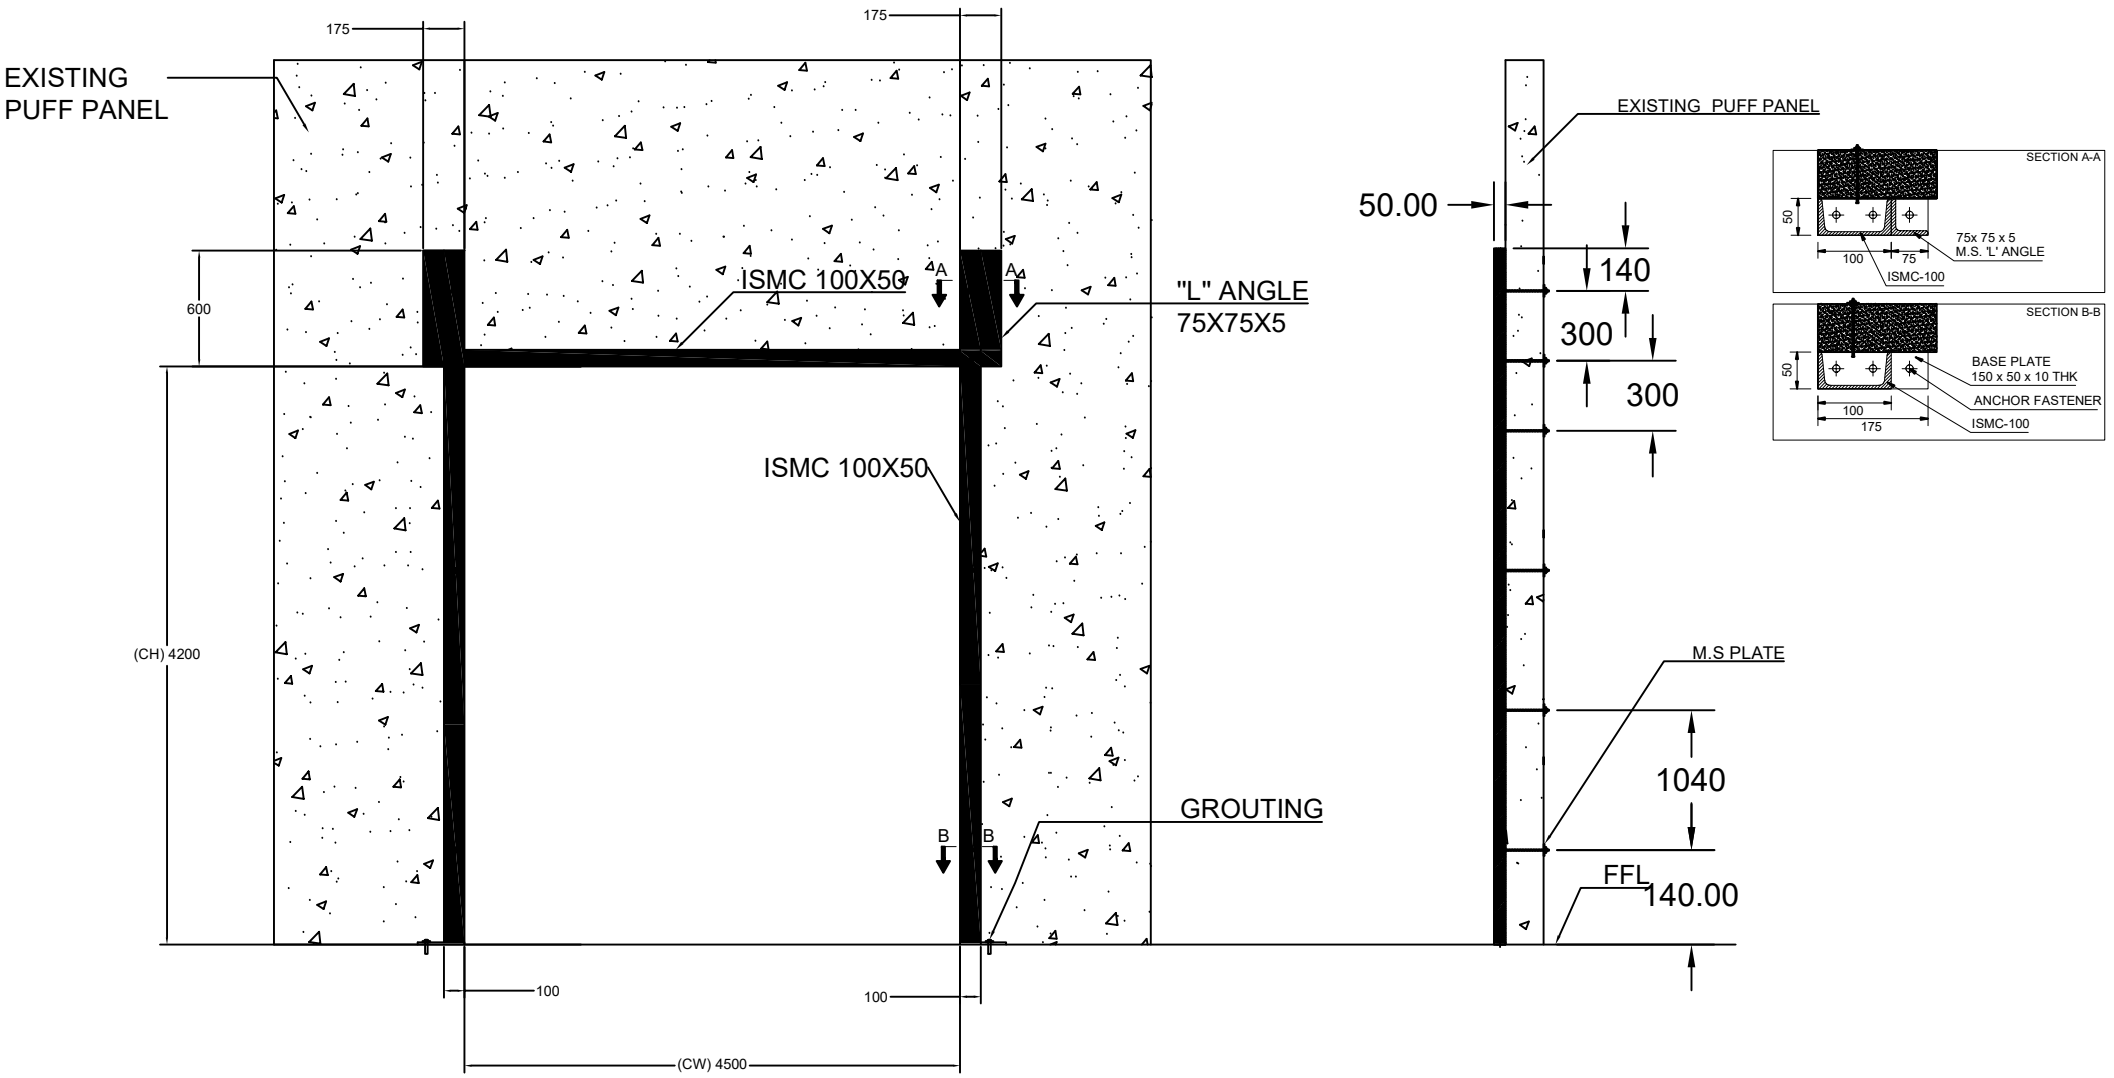

M.S. STRUCTURE DETAILS

Sr	Description	Clear Width (CW)	Clear Height (CH)	QTY
1	HSD With Sensor	**4500**	**4200**	1

This drawing & design is the property of NIHVA TECHNOLOGIES. Not to be sold or copied to any other concern.

TITLE	HIGH SPEED DOOR STRUCTURE DRAWING			NIHVA TECHNOLOGIES PVT. LTD. PUNE Tel : 020 66304033 Email:- info@nihva.com Website:- www.nihva.com	
	NAME	SIGN	DATE		
DRAWN	S.J		18.01.2024	CLIENT - RINAC	
CHECK	A.K		18.01.2024	PROJECT - HIGH SPEED DOOR ST.	
APPRD.	V.T		18.01.2024	FORMAT NO - NIHVA-DD-F-03	
If any queries contact : projectsupport@nihva.com				DWG. NO. : NIHVA/23-24/00XX	REV- R00
ALL DIMENSION ARE IN mm				SCALE: NTS	WT: SHEET: