


DETAIL VIEW OF B

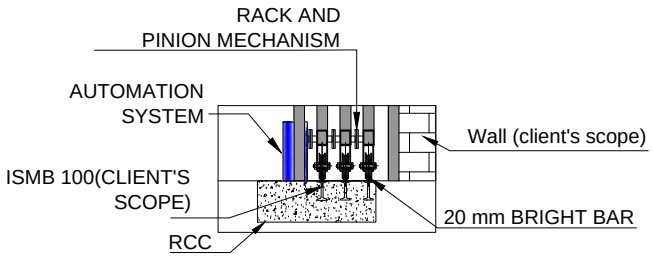

DETAIL VIEW OF A

NOTE:-
1.ALL REQUIRED CIVIL WORK BE IN CLIENTS SCOPE.
2.ONE COAT OF RED OXIDE & TWO COAT OF APPROVED RAL SHADE WILL BE GIVEN TO THE GATE.
3.IF NECESSARY GATE LEAF WILL BE IN TWO PARTS FOR TRANSPORTATION & WILL BE WELD TOGETHER ON SITE.

CLEAR WIDTH	CLEAR HEIGHT	QUANTITY.
35000mm	1800mm	01 NOS

This drawing & designing is the property of NIHVA TECHNOLOGIES. Not to be sold or copied to any other concern.

TITLE: AUTOMATIC 3 LEAF TELESCOPIC GATE

		SIGN	DATE
DRAWN	SURAJ		06-10-18
CHECK	PRADEEP		06-10-18
APPROVAL	R.D		06-10-18

If any queries contact :design@nihva.com

ALL DIMENSION ARE IN mm

NIHVA TECHNOLOGIES PVT. LTD. PUNE
Tel : 020 66304033
Email:- info@nihva.com
Website :- www.nihva.com

CLIENT -INDAMAR
PROJECT -
SITE -NAGPUR
DWG. NO. : NIHVA/18-19/0139 REV.- 0
SCALE: NTS WT: SHEET: 01 OF 01