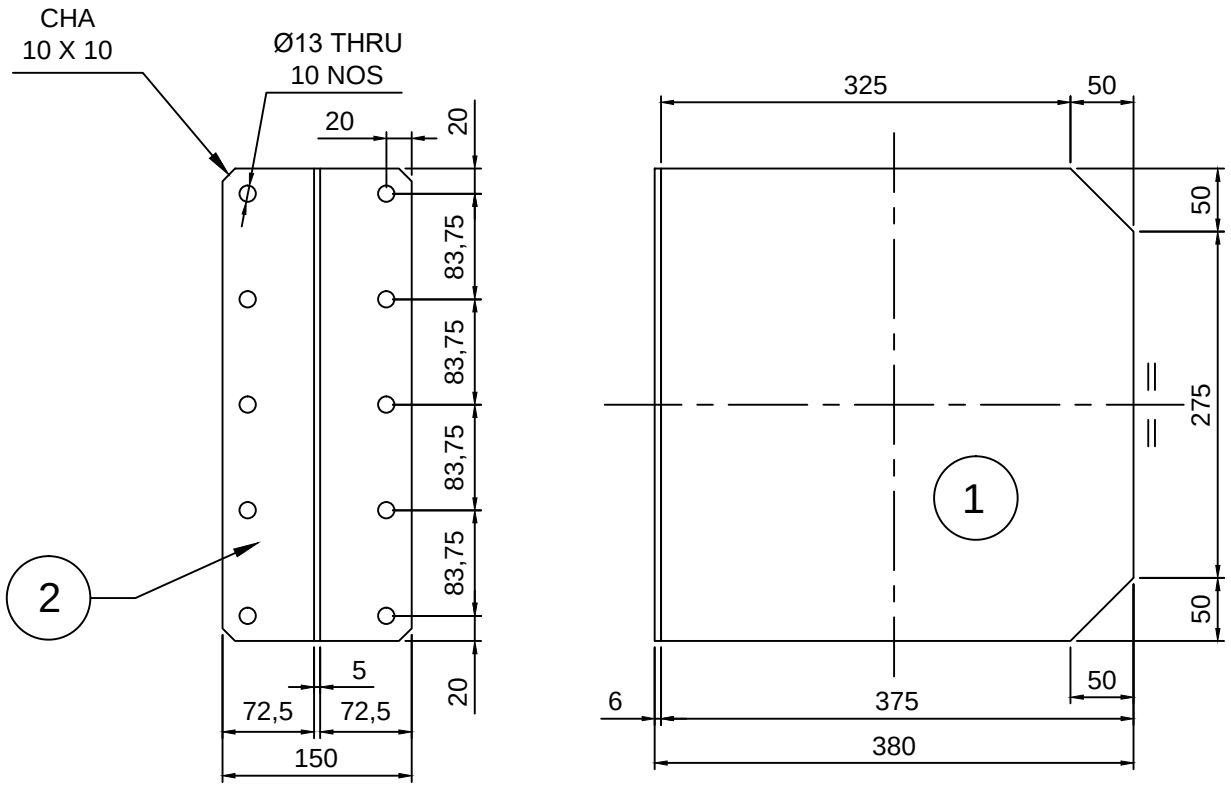


1. SHEET 375 X 5THK X 375L = 2 NOS
2. FLAT 150 X 6 X 375L = 2 NOS

MATERIAL- MS
THICKNESS- 5mm
QUANTITY- 2 NOS

This drawing & design is the property of NIHVA TECHNOLOGIES. Not to be sold or copied to any other concern.

TITLE	MS BRACKET		NIHVA TECHNOLOGIES PVT. LTD. PUNE Tel : 020 66304033 Email:- info@nihva.com Website:- www.nihva.com
	SIGN	DATE	
DRAWN	PRADEEP	25.04.2018	CLIENT -
CHECK	OMKAR	25.04.2018	PROJECT -
REV.			SITE -
APPROVAL	OMKAR	25.04.2018	DWG. NO. : NIHVA_18_19_VDR_009
If any queries contact : design@nihva.com			SCALE: NTS / WT: / SHEET: 01 OF 01
ALL DIMENSION ARE IN mm			