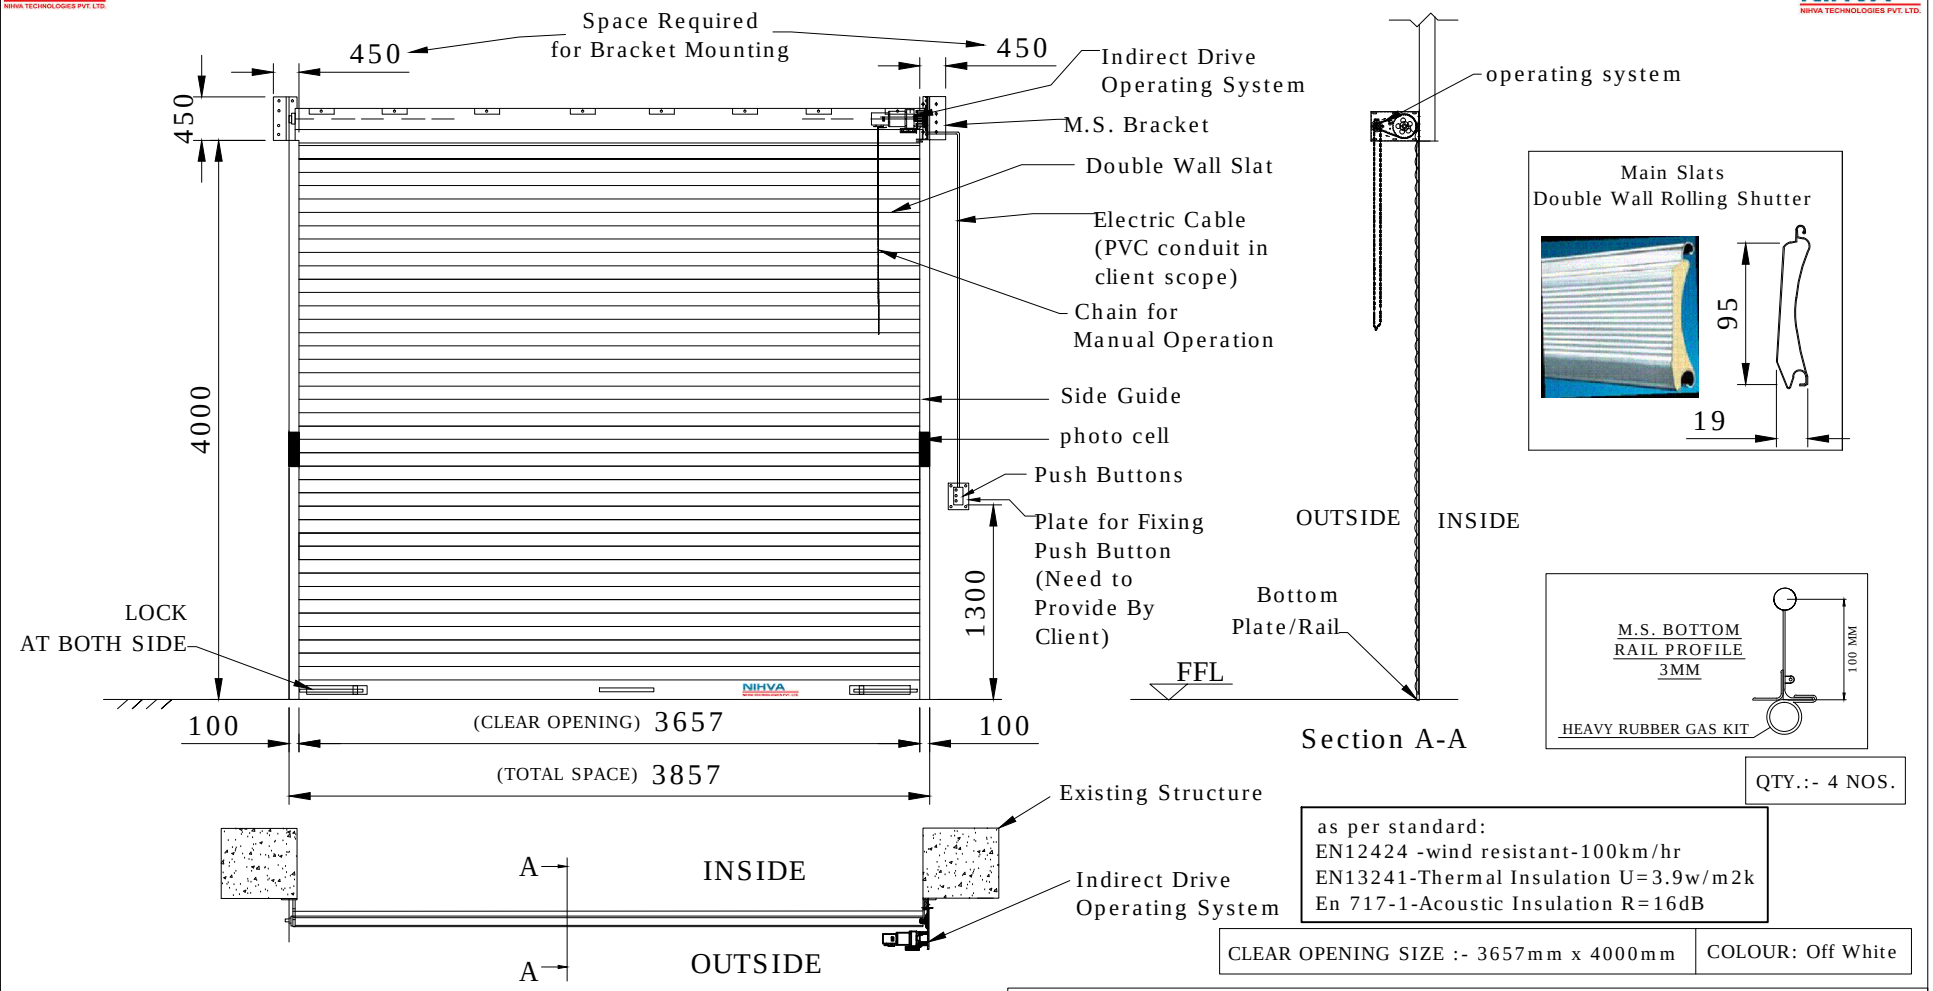



QTY.:- 4 NOS.

as per standard:
EN12424 -wind resistant-100km/hr
EN13241-Thermal Insulation U=3.9w/m2k
En 717-1-Acoustic Insulation R=16dB

| CLEAR OPENING SIZE :- 3657mm x 4000mm | COLOUR: Off White |
|---|---|

NOTE: push button fixing will be decided as per site ready condition.

| Sr. No. | Details | Specification |
|---|---|---|
| 1) | Slats Profile | 95mm x 19mm with PU filled inside |
| 2) | Guide Channel | 100mm x 40mm |
| 3) | Shaft | 125mm OD with heavy duty flanges and hardware |
| 4) | Bottom Rail | 125mm x3mm thick with extra angle support. Locking arrangement provides |
| 5) | Brackets | 450mmx450mmx3mm thickness |

This drawing & designing is the property of NIHVA TECHNOLOGIES. Not be sold or copy to any other concern.

TITLE:

DOUBLE WALL
ROLLING SHUTTER

CLIENT APPROVAL

ALL DIMENSION ARE IN mm

| | SIGN | DATE |
|---|---|---|
| DRAWN | ABHIJIT | 19/11/15 |
| CHECK | ANIL | 19/11/15 |
| REV. | 01 | |
| APPRD. | | |
| MFG | | |
| Ref. No. | | |

NIHVA TECHNOLOGY
PVT. LTD. PUNE
Tel : 020 66304033
Email:- info@nihva.com
Website:- www.nihva.com

CLIENT - APOLLO POWER SYSTEMS PVT. LTD.

PROJECT - INGERSOLL RAND

SITE -

DWG. NO. -NIHVA/15-16/156

SCALE: 01 | WT: | SHEET: 01 OF 01

If any queries contact : projects@nihva.com