




SIDE VIEW

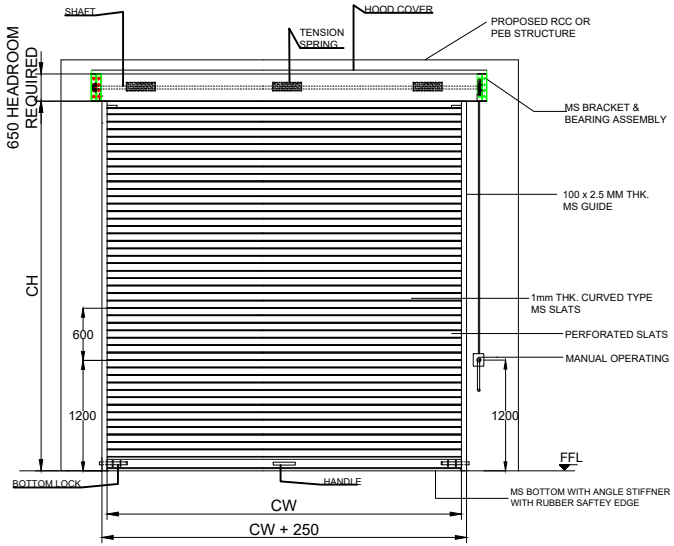


INSIDE ELEVATION

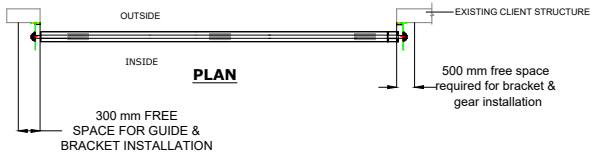


PLAN

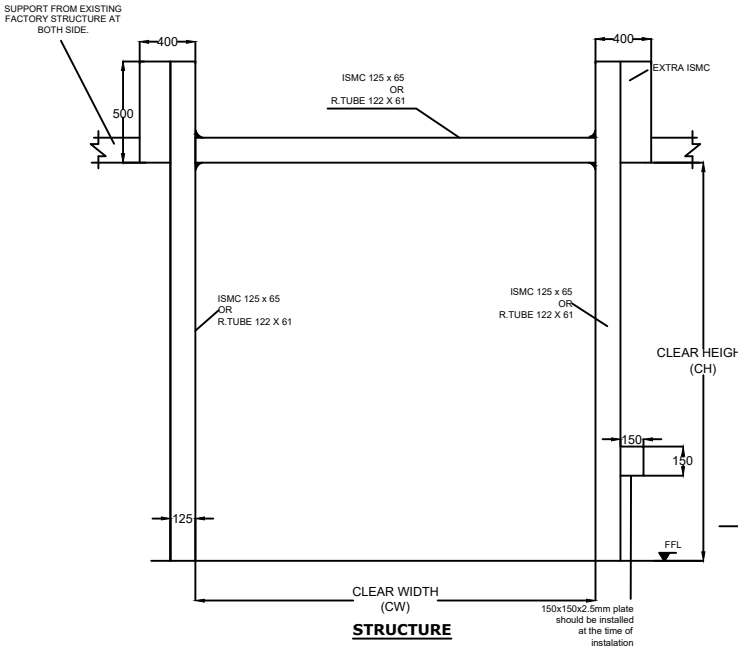

STRUCTURE

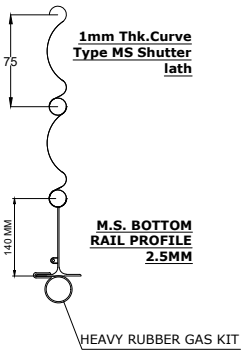

M.S. BOTTOM RAIL PROFILE 2.5MM

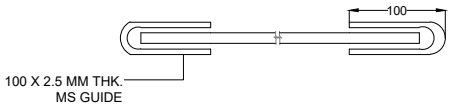

TOLERANCE - ±10mm

SR NO	CLEAR WIDTH	CLEAR HEIGHT	QUANTITY
1	5000	4500	01 NO

NOTE-
1. ALL CIVIL WORK WILL BE CLIENT'S SCOPE.
2.IF STRUCTURE REQUIRED FOR SHUTTER IS IN CLIENT'S SCOPE.

This drawing & design is the property of NIHVA TECHNOLOGIES. Not to be sold or copied to any other concern.

TITLE: GEAR OPERATED ROLLING SHUTTER

	NAME	SIGN	DATE
DRAWN	B.S.		23.06.2025
CHECK	V.T.		23.06.2025
APPRD.	V.T.		23.06.2025

If any queries contact : design@nihva.com

ALL DIMENSION ARE IN mm

NIHVA TECHNOLOGIES PVT. LTD.
NIHVA TECHNOLOGIES PVT. LTD. PUNE
Tel : 020 66304033
Website:- www.nihva.com
Email:- info@nihva.com

CLIENT - TATA COMMINS

PROJECT -

SITE LOCATION -

DWG. NO. : NIHVA/21-22/VDR/020 | REV- R00

SCALE: NTS | WT: | SHEET: 01 OF 01