



# Gate Opening Position

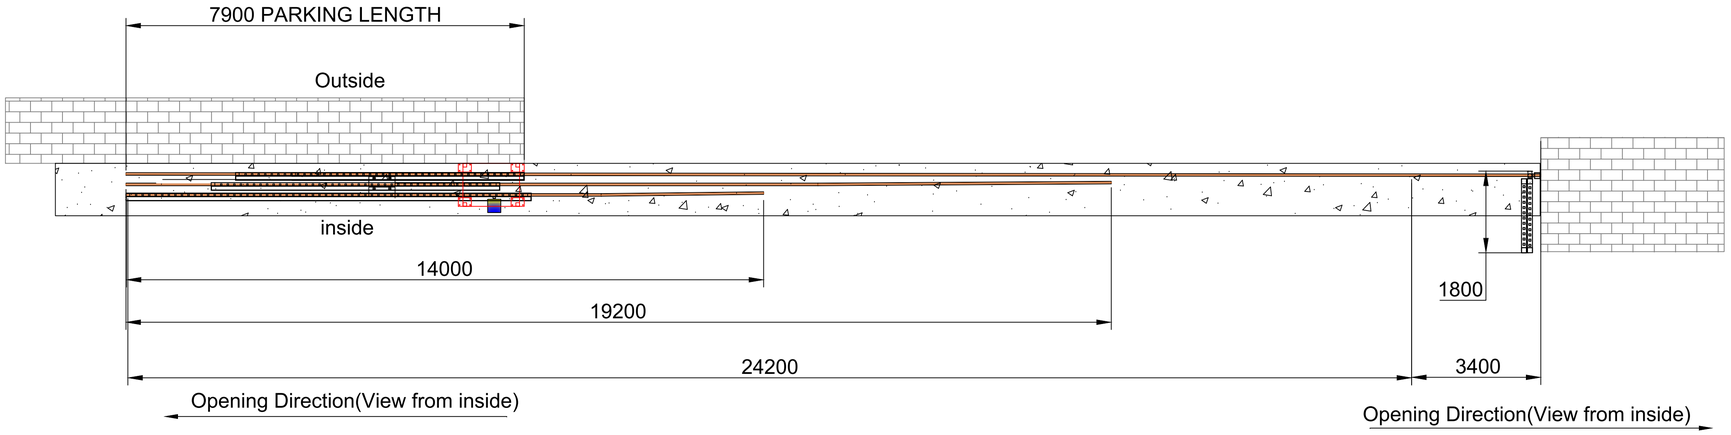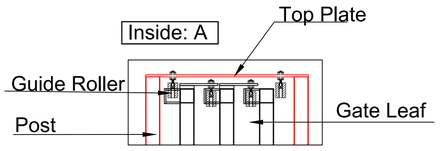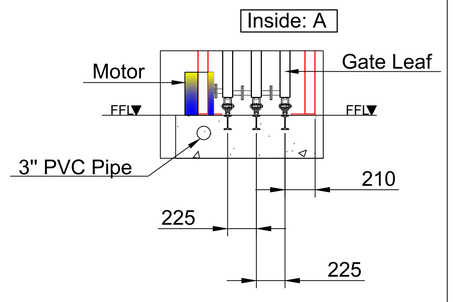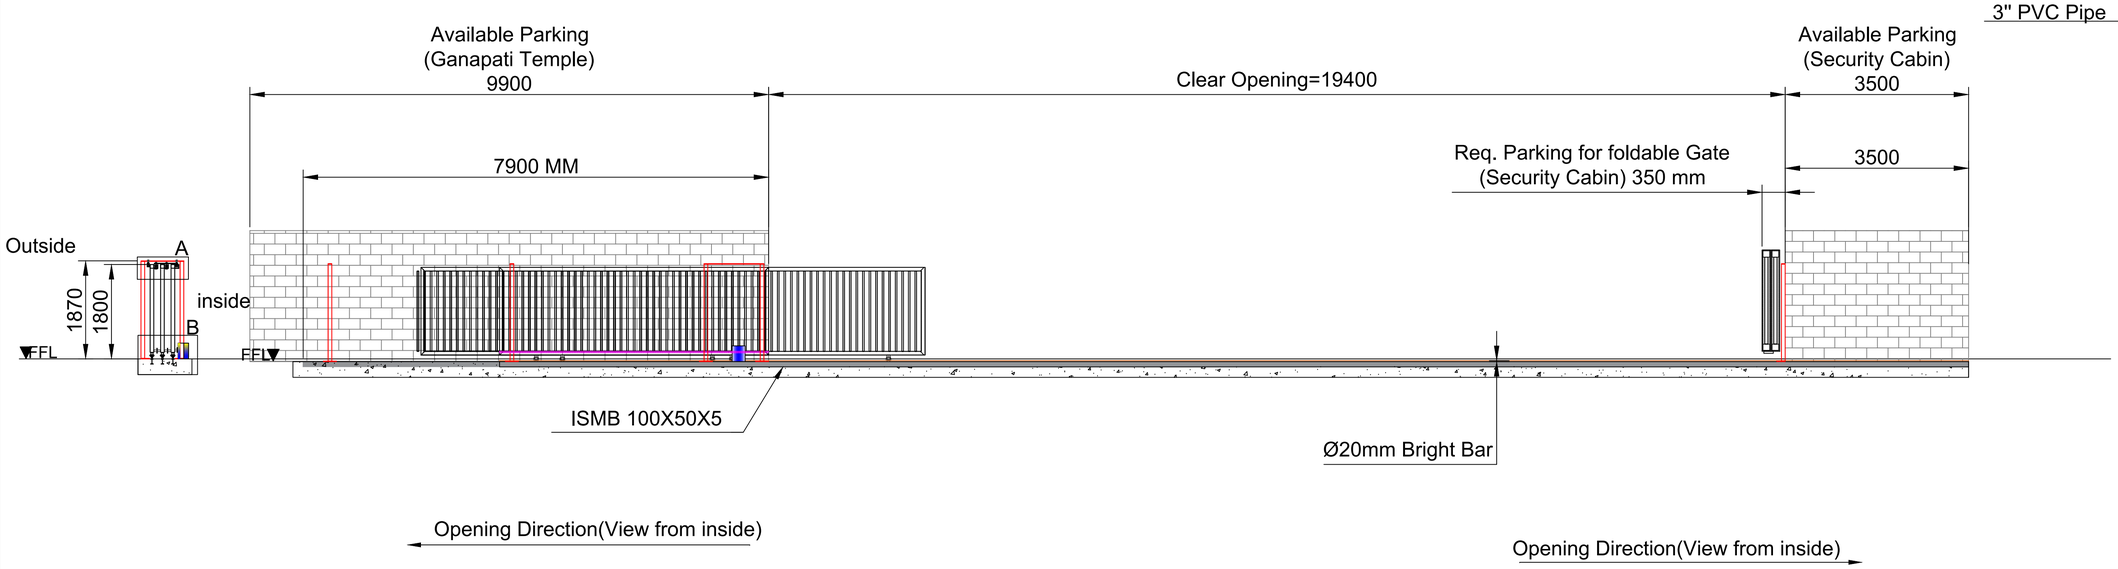


## Note:-

1. All Dimension are in MM
2. Required All civil work will be in Client scope
3. Installlation and Fabrication tolerance will be ±20mm
4. Required Parking will be 8000 mm
5. Gate Color will be Metalic color,shade stone gray(RAL7030)

| Rev No. | Revision | Date | Revised By |
|---|---|---|---|
| 01 | REVISED WITH FOUNDATION OF FOLDABLE GATE | 25/08/2022 | MAHESH S. |

This drawing & design is the property of NIHVA TECHNOLOGIES. Not to be sold or copied to any other concern.

TITLE:-
Bi-Parting Tel.Sliding Gate

| | NAME | DATE | SIGN |
|---|---|---|---|
| DRAWN | MAHESH.S | 30/07/2022 | |
| CHECK | MAHESH.S | 30/07/2022 | |
| APPRD. | AMIT.K | 30/07/2022 | |

If any queries contact : design@nihva.com

ALL DIMENSION ARE IN mm

NIHVA TECHNOLOGIES PVT. LTD.
NIHVA TECHNOLOGIES PVT. LTD. PUNE
Tel : 020 66304033
Email:- info@nihva.com
Website:- www.nihva.com

CLIENT - NAVNEET EDUCATION LTD
LOCATION - PALGHAR
PRODUCT - TEL.SLIDING GATE | QTY-01
DWG NO:- NIHVA/22-23/CLT/0071_7 | REV-01
SCALE: NTS | SCALE:-- 1:1 | SHEET: 01 OF 01