

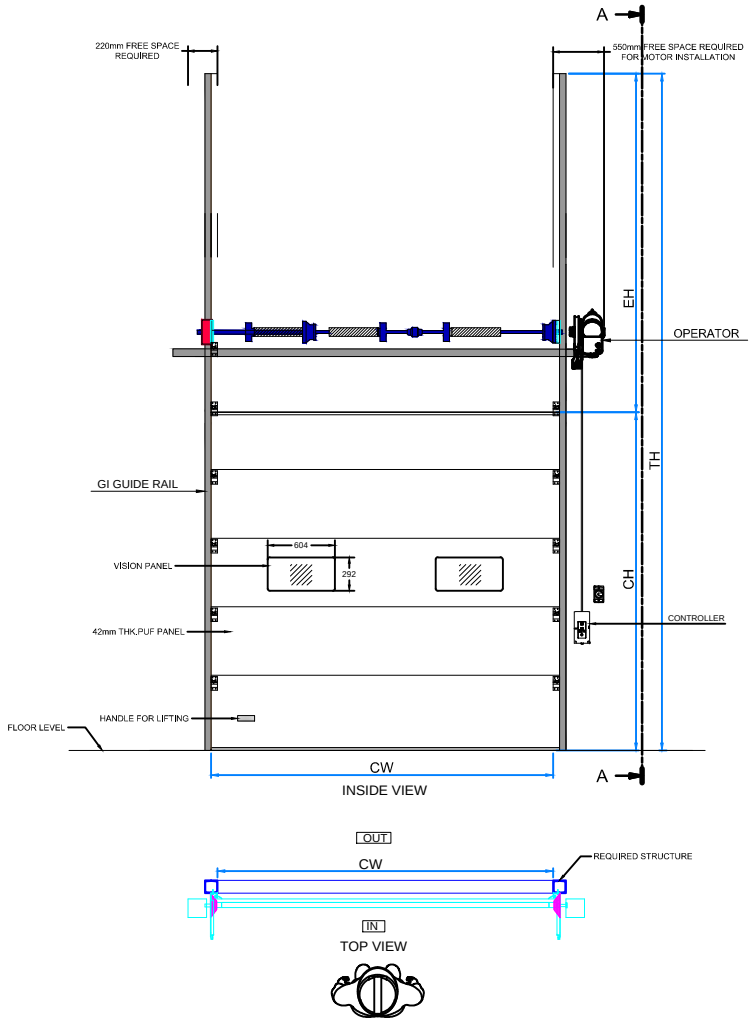


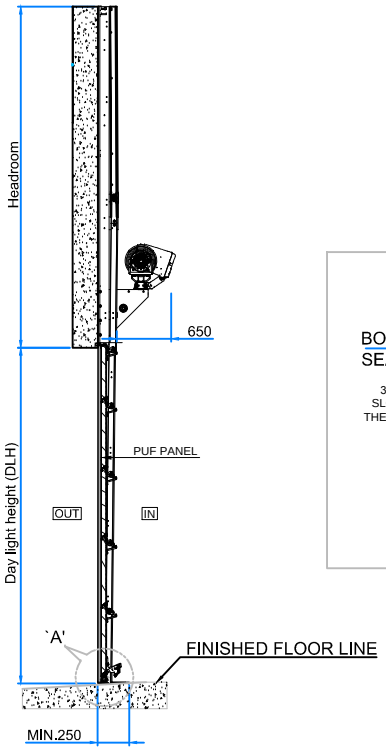

SECTION A-A

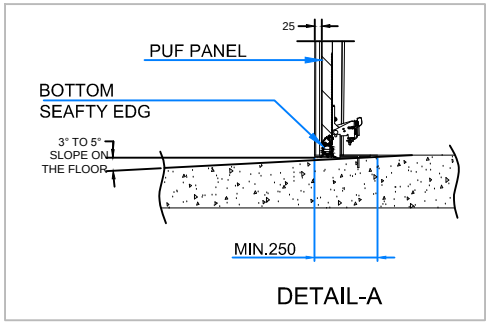

DETAIL-A

TOP VIEW

NOTE:-

1. ALL REQUIRED CIVIL WORK & M.S STRUCTURE WORK WILL BE IN CLIENTS SCOPE.

SR NO	CLEAR WIDTH	CLEAR HEIGHT	QTY	TH	EH
01	2700 mm	3500 mm	17	7365	4665

RAL 7026	GRANITE GREY	
RAL 7016	ANTHRACITE GRAY	
RAL 9007	GREY ALUMINIUM	
RAL CODE	RAL COLOR	APPROVE

TOLERANCE: ±10mm

This drawing & design is the property of NIHVA TECHNOLOGIES. Not to be sold or copied to any other concern.

TITLE: SECTIONAL DOOR (VL)

NIHVA TECHNOLOGIES PVT. LTD. PUNE
Tel : 020 66304033
Website:- www.nihva.com
Email:- info@nihva.com

	NAME	SIGN	DATE
DRAWN	AKASH		21.01.19
CHECK	VIKRANT		21.01.19
APPROVAL	R.D		21.01.19

If any queries contact : design@nihva.com

ALL DIMENSION ARE IN mm

CLIENT - ESR PUNE

PROJECT - BMW

SITE - CHAKAN, PUNE

DWG. NO. : NIHVA/18-19/0243 REV: 00

SCALE: NTS WT: SHEET: 01 OF 01