

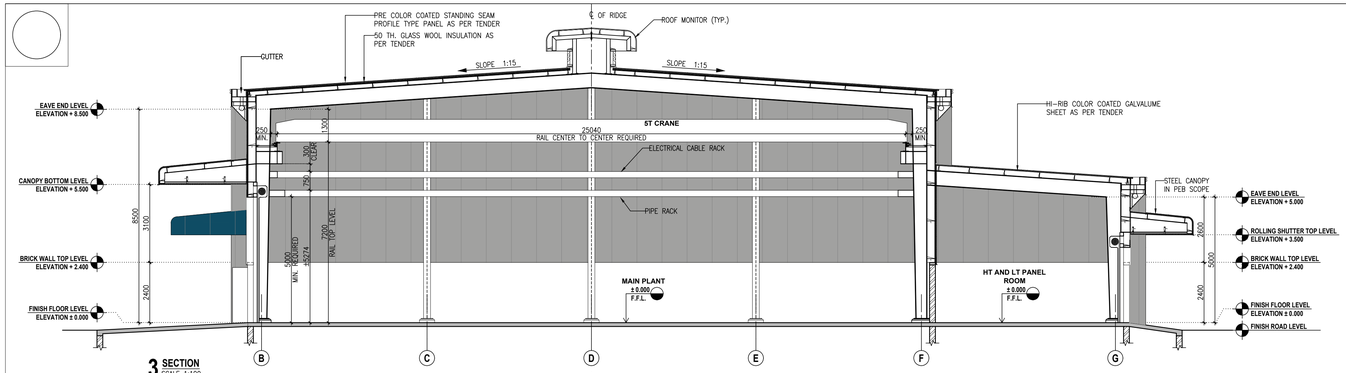




**3 SECTION**
SCALE 1:100

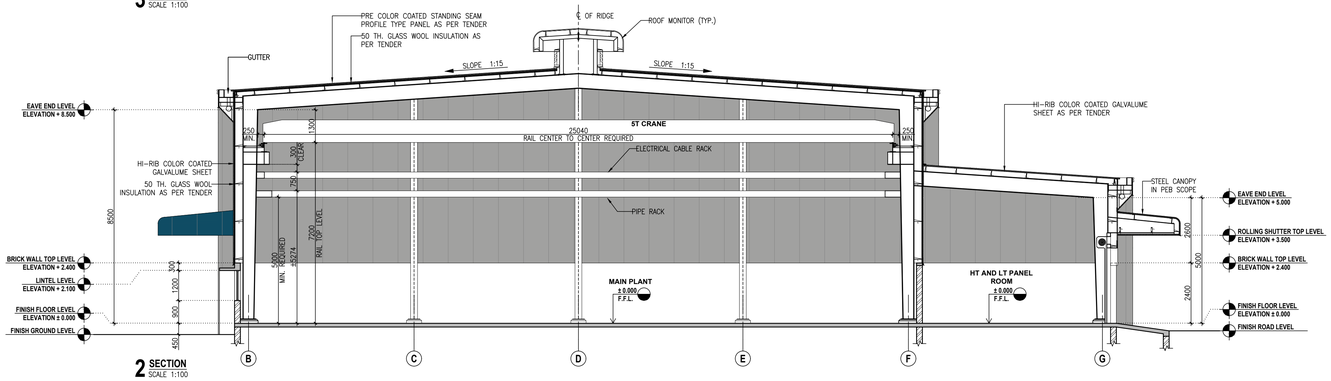


**2 SECTION**
SCALE 1:100

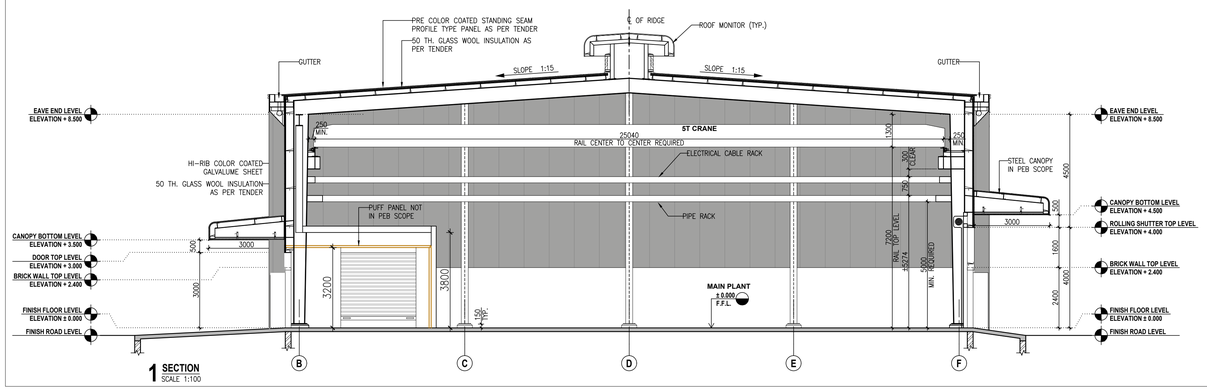


**1 SECTION**
SCALE 1:100

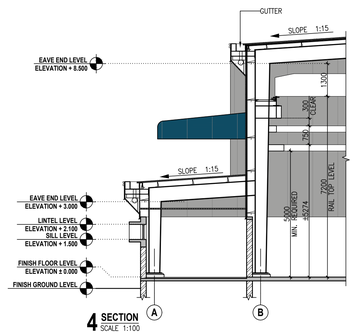


**4 SECTION**
SCALE 1:100

THIS DRAWING & DESIGN IS THE SOLE PROPERTY OF VMS & SHALL NOT BE COPIED, TRACED OR REPRODUCED BY ANY MEANS WITHOUT PRIOR WRITTEN CONSENT OF THE FIRM.

## GENERAL NOTES :


1. ALL THE DIMENSIONS ARE UNFINISHED DIMENSIONS.
2. ALL DIMENSIONS ARE IN MM AND LEVELS ARE IN MT, UNLESS OTHERWISE MENTIONED.
3. ALL THE DIMENSIONS SHALL BE READ & NOT TO BE MEASURED.
4. IN CASE OF ANY DISCREPANCY, BRING IT TO THE NOTICE OF THE ARCHITECT IMMEDIATELY.
5. DETAIL DRAWING PRECEDES THE GENERAL DRAWING

**FOR TENDER**

| NO. | DATE | DESCRIPTION | DRAWN BY | CHECKED BY |
|---|---|---|---|---|
| R0 | - | - | - | - |

**REVISION HISTORY**

KEY PLAN
SCALE : N.T.S.

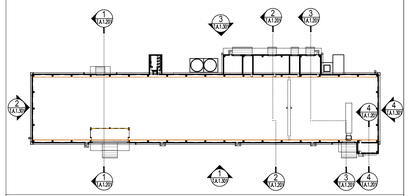


| REFERENCE DRAWINGS : | |
|---|---|
| 01. ARCHITECTURAL : | - |
| 02. STRUCTURAL : | - |
| 03. HVAC : | - |
| 04. ELECTRICAL : | - |
| 05. UTILITIES : | - |

## SECTIONS

# MAIN PLANT BUILDING

## SUCHI FOAMS PVT. LTD. AT - KHAVAD, TA - KADI.

| PROJECT NO. | | | |
|---|---|---|---|
| 1219 | SCALE : 1:100 | DRAWN : | PARESH |
| | | CHECKED: | PARESH |
| | DATE : 26-07-2019 | APPROVED: | NITESH |
| | | COORDINATION CHECKED: | NITESH |

VMS ENGINEERING & DESIGN SERVICES (P) LTD.
CHITRAKOOT FLATS, B/H TIMES OF INDIA, OFF ASHRAM ROAD,
AHMEDABAD-380 009. PHONE: +91 (079) 2658-8829, 4023-6236
WWW.VMSCONSULTANTS.COM

| SHEET SIZE | DRAWING NO. | TENDER | REVISION: |
|---|---|---|---|
| 600x 1000 | T.A.1.201 | T | R0 |