


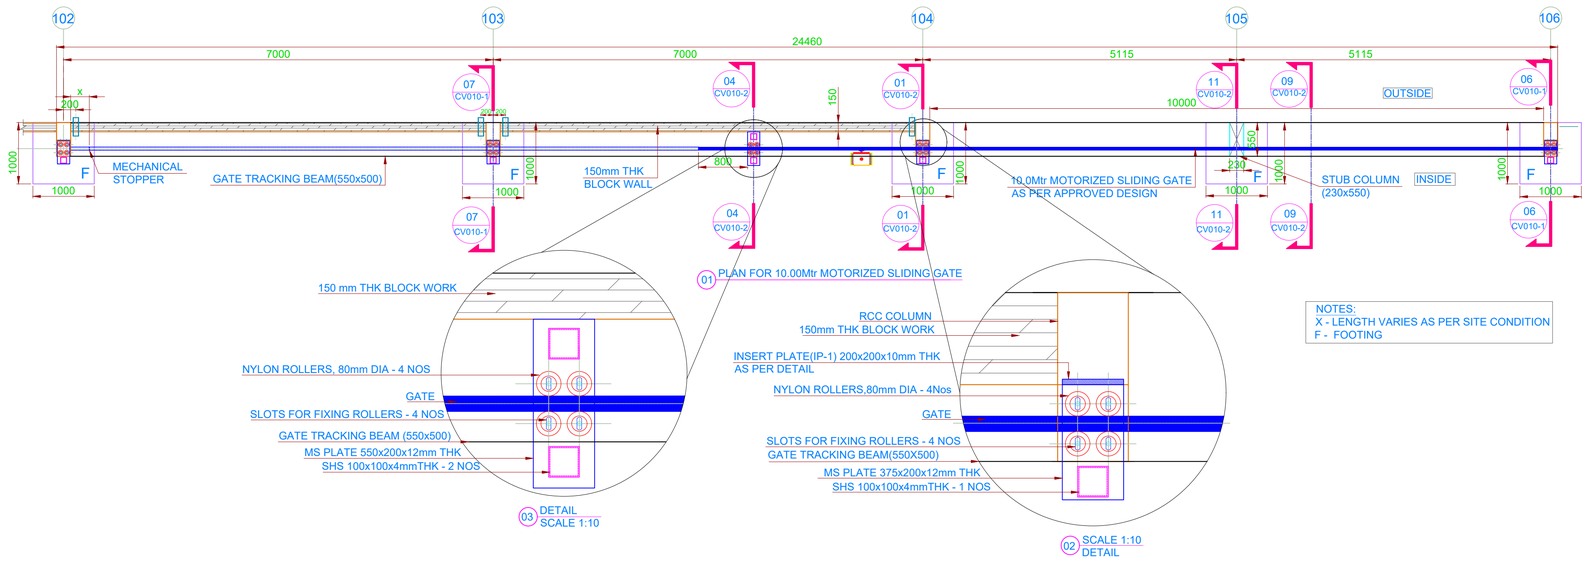


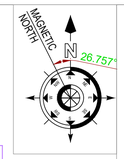


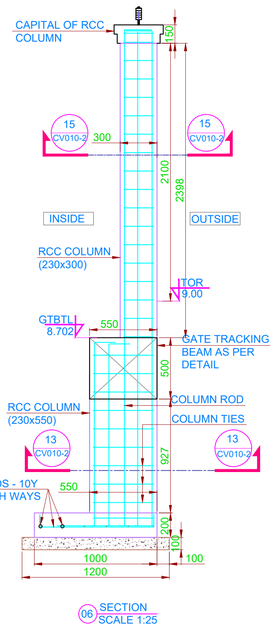


TYPICAL REINFORCEMENT DETAIL FOR COLUMNS @ GRID 106

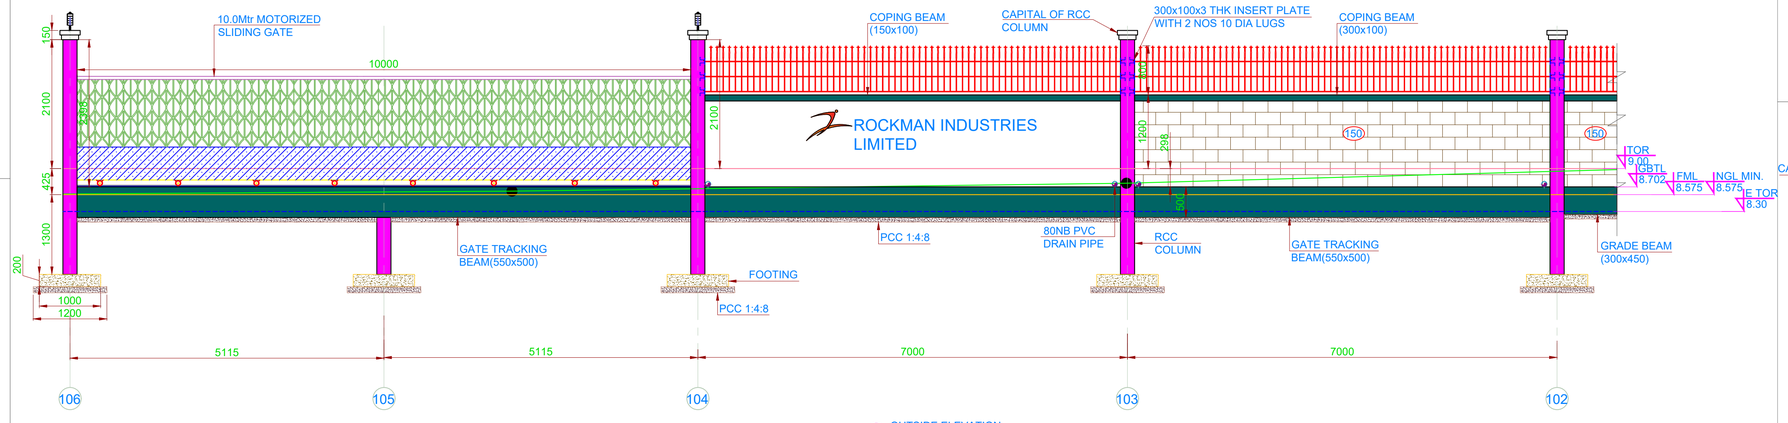

04 OUTSIDE ELEVATION

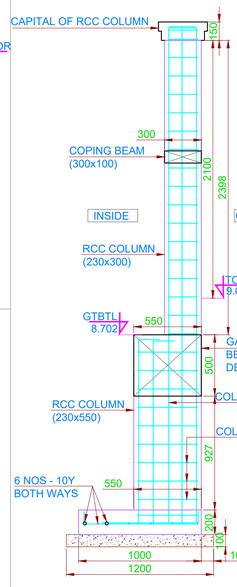

TYPICAL REINFORCEMENT DETAIL FOR COLUMNS @ GRID 102 TO 104

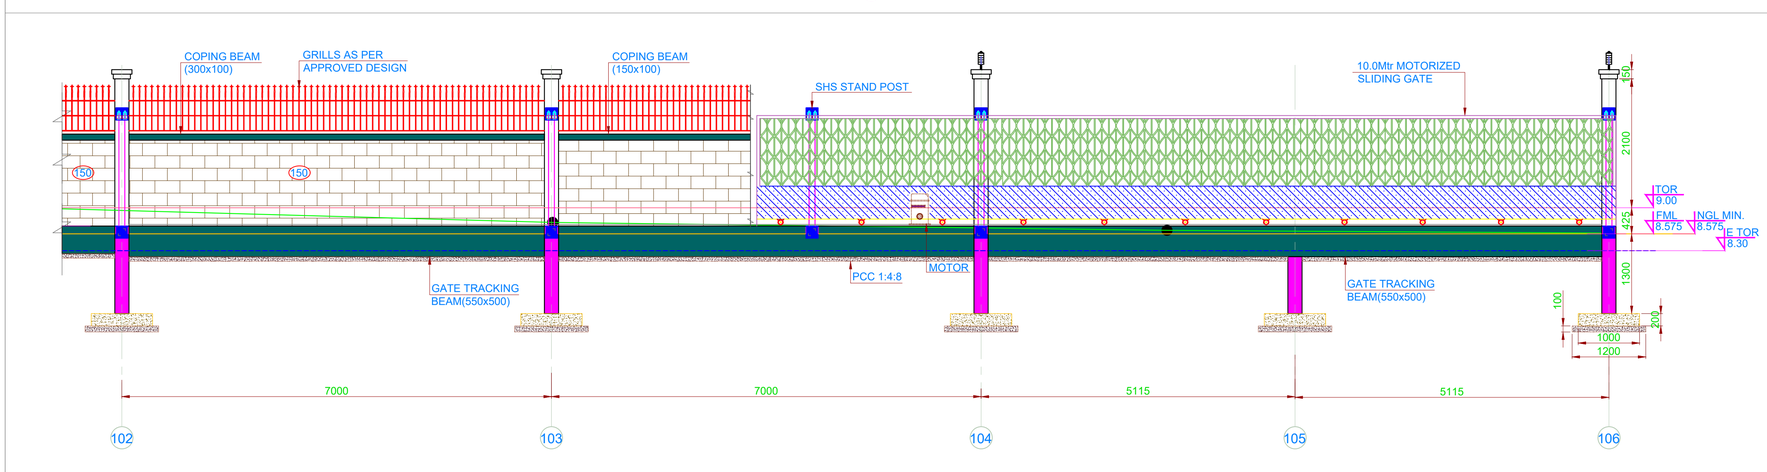

05 INSIDE ELEVATION

IMPORTANT NOTE :
VENDOR SHOP DRAWING AND TECHNICAL DATA SHEET TO BE SUBMITED FOR APPROVAL.

GENERAL NOTES

1. ALL DIMENSIONS ARE IN 'mm'.
2. ALL LEVELS ARE IN 'Mtrs'.
3. GRADE OF CONCRETE - M25
4. Y= HIGH YIELD STRENGTH REINFORCEMENT STEEL FE500D TMT BARS

KEY PLAN

Date	Purpose of Issue	Version
23.01.2024	GOOD FOR CONSTRUCTION	R0

Milestones

GOOD FOR CONSTRUCTION

VER	DSN	Date	DRW	Date	CHK	Date	APR	Date
R0	VR	23.01.24	FV	23.01.24	MA	23.01.24	DC	23.01.24

CLIENT

ROCKMAN INDUSTRIES LTD,
9th FLOOR, UNIT 3&4, EMAAR CAPITAL TOWER - 2
SECTOR - 26, SIKANDERPUR GHOSI, M G ROAD,
GURUGRAM – 122002. HARYANA, INDIA

PROJECT NAME

M/S. ROCKMAN INDUSTRIES CHENNAI PVT.LTD,
NO:6/2, CHELLAPERUMPULIMEDU, CHOLAVARAM POST,CHEYYAR TALUK,THIRUVANNAMALAI DISTRICT-631701.

PROJECT CODE: 357

ARCHITECTS & CONSULTANTS
BESTEN Engineers & Consultants India Pvt. Ltd.
F-2, LAKSHMI APARTMENTS,
NO. 95, PERIYAR PATHAI,CHOOLAIMEDU (WEST),
CHENNAI - 600 094.
PH : 044 - 23611595. email : contact@besten.in, www.besten.in

Project Component : SITE

Scale at A1 : 1 : 50

DRAWING NO. SI 1 0 7 C V 0 1 0

Sheet No 01 / 02

Drawing Title : 10.0 Mtr SLIDING GATE LAYOUT AND DETAIL

Revision No GF R 0

Graphic Scale : 0 1 2 3 4 5 6 7 8 9 10

This drawing and its contents is the property of Besten Engineers & Consultants India Private Limited and is covered under intellectual property rights. This drawing must not be copied, electronically transmitted, or passed on to any third person/firm/ party in part or in full, nor be made use by such persons/ firm/ parties without our authorisation in writing. This drawing is to be returned after the purpose of issue is fulfilled.