RAILING & DOOR ASSLY

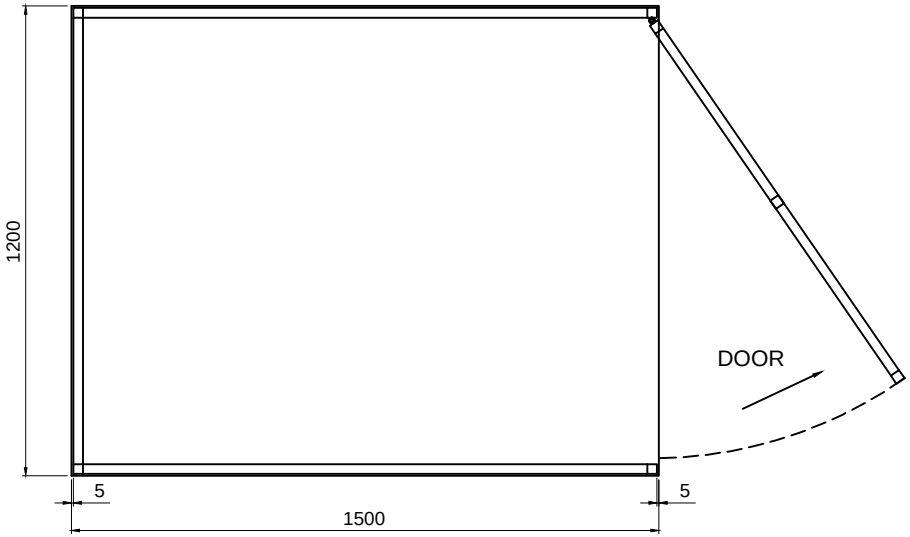

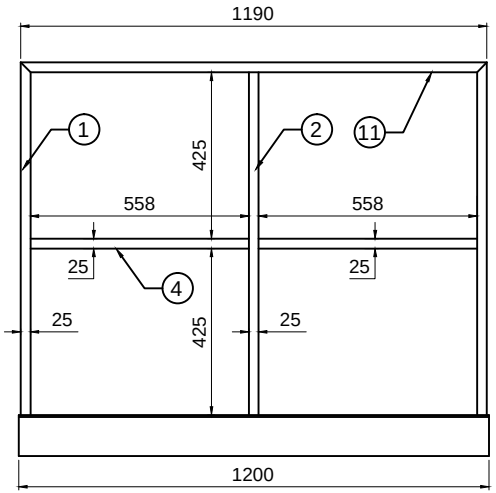

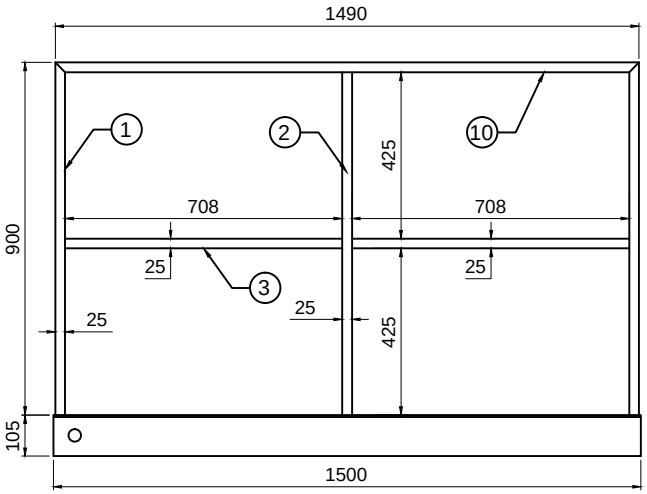

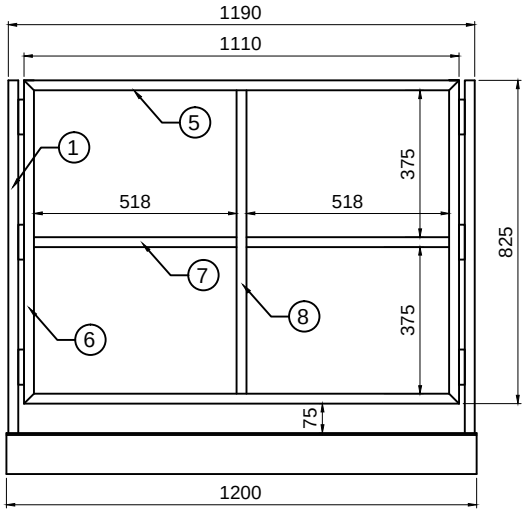

SR.NO	DESCRIPTION	QTY.	SR.NO	DESCRIPTION	QTY.
1.	SQ.TUBE 25 X 25 X 2.5 THK X 900L	4 NOS	10.	SQ.TUBE 25 X 25 X 2.5 THK X 1490L	2 NOS
2.	SQ.TUBE 25 X 25 X 2.5 THK X 875L	3 NOS	11.	SQ.TUBE 25 X 25 X 2.5 THK X 1190L	1 NO
3.	SQ.TUBE 25 X 25 X 2.5 THK X 708L	4NOS			
4.	SQ.TUBE 25 X 25 X 2.5 THK X 558L	2NOS			
5.	SQ.TUBE 25 X 25 X 2.5 THK X 1110L	1 NO			
6.	SQ.TUBE 25 X 25 X 2.5 THK X 825L	2NOS			
7.	SQ.TUBE 25 X 25 X 2.5 THK X 518L	2NOS			
8.	SQ.TUBE 25 X 25 X 2.5 THK X 775L	1 NO			
9.	HEAVY DUTY HINGES	6NOS			

This drawing & design is the property of NIHVA TECHNOLOGIES. Not to be sold or copied to any other concern.

TITLE : -
SAFETY RAILING ASSLY

NIHVA TECHNOLOGIES PVT. LTD.
NIHVA TECHNOLOGIES PVT. LTD. PUNE
Tel : 020 66304033
Email:- info@nihva.com
Website:- www.nihva.com

	SIGN	DATE
DRAWN	P.A	04.10.18
CHECK	R.D	04.10.18
REV.		
APPROVAL		

If any queries contact : projects@nihva.com

ALL DIMENSION ARE IN mm

CLIENT -
PROJECT -
SITE -
DWG. NO. : NIHVA/18-19/MFG/NSL/1018/004
SCALE: NTS | WT: | SHEET: 01 OF 01