
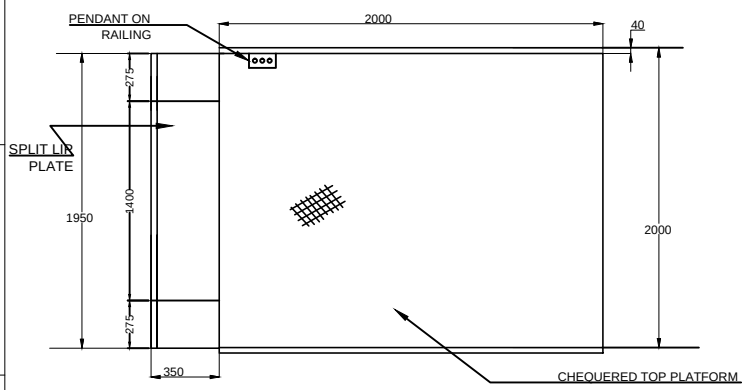



FOR CIVIL WORK OF PIT , KINDLY REFER PIT DRAWING ATTACHED .
NIHVA/20-21/0095/R02 SHEET - 2 OF 2

| REV NO | DRAWN | DATE | REMARK |
|---|---|---|---|
| R02 | S.M.S. | 1.1.2021 | PIT DRAWING REVISED |
| R01 | S.M.S. | 9.12.2020 | (1) LIFT HEIGHT CHANGED TO 600MM<br>(2) SPLIT LIP |

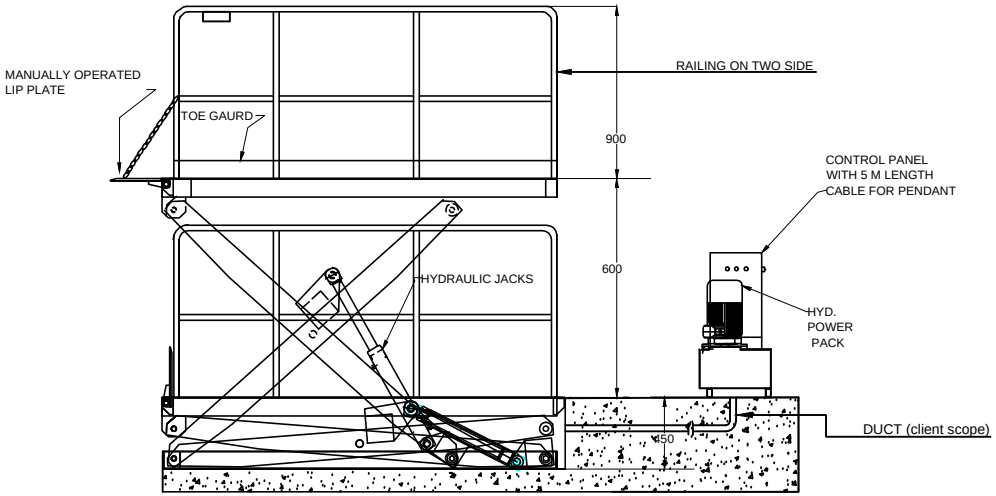


**SPECIFICATION OF PIT MOUNTED HYDRAULIC SCISSOR LIFT- R00**

| SR NO | PARAMETER | DESCRIPTION |
|---|---|---|
| 1 | CAPACITY | 2 TON |
| 2 | PLATFORM SIZE(CHEQUERED) | 2000mm(L) X 2000mm(W) |
| 3 | SHUT HEIGHT | 450 mm |
| 4 | LIFT HEIGHT | 600 mm |
| 5 | TOTAL HEIGHT | 1050 mm |
| 6 | RAILING HEIGHT (2 SIDE) | 900 mm |
| 7 | MANUAL LIP(1 SIDE)(PLAIN & SPLIT) | 1950(L) X 350(W) |
| 8 | PIT SIZE | 2250(L)X2050(W) |
| 9 | CONTROL PANEL | STANDARD |
| 10 | POWERPACK | 3 HP, 3 PHASE AC |
| 11 | PENDANT | PUSH BUTTON MOUNTED ON RAILING |
| 12 | FEATURE | LIFT CUT-OFF SWITCH |

RAL CODE PAINT (NIHVA STANDARD) , KINDLY INFORM IF OTHER. | RAL 1004 GOLDEN YELLOW

NOTE :
1. PIT FOR SCISSOR LIFT HAS TO BE DIAGONALLY WITHIN 3-5 MM
2. BASE OF THE PIT HAS TO BE IN WATER LEVEL AND RIGHT ANGLE TO THE VERTICAL SIDE WALLS
3. PROPER ARRANGEMENT FOR ROUTING HOSES AND CABLES HAVE TO BE MADE DEPENDING ON SITE CONDITIONS AND POSITION OF POWER PACK & IN CLIENT SCOPE.
4. COVERING REQUIRED FOR HOSES, PANEL , AND CABLES RELATED CIVIL WORK IS IN CLIENTS SCOPE ALSO PROPER DRAINAGE SYSTEM SHOULD BE PROVIDED FOR THE PIT.
5. PIT , DUCT FOR HOSE, CABLE & ALL REQUIRED CIVIL WORK IS IN CLIENT SCOPE.
6. LEVEL OF THE PIT SHOULD BE PLAIN & AT LEAST TAKE LOAD OF 6000KG.

This drawing & design is the property of NIHVA TECHNOLOGIES. Not to be sold or copied to any other concern.

TITLE PIT MOUNTED HYDRAULIC SCISOR LIFT

| | NAME | SIGN | DATE |
|---|---|---|---|
| DRAWN | SIDDHESHWAR | | 26.11.2020 |
| CHECK | | | |
| APPRD. | | | |

If any queries contact : projectsupport@nihva.com

ALL DIMENSION ARE IN mm

NIHVA TECHNOLOGIES PVT. LTD.
NIHVA TECHNOLOGIES PVT. LTD. PUNE
Tel : 020 66304033
Email:- info@nihva.com
Website:- www.nihva.com

CLIENT - ADVIK HI-TECH PVT LTD
PROJECT - ADVIK HI-TECH PVT LTD
SITE LOCATION - CHAKAN ,PUNE
DWG. NO. : NIHVA/20-21/0095/R02 | REV- R02
SCALE: NTS | WT: | SHEET: 1 OF 2