

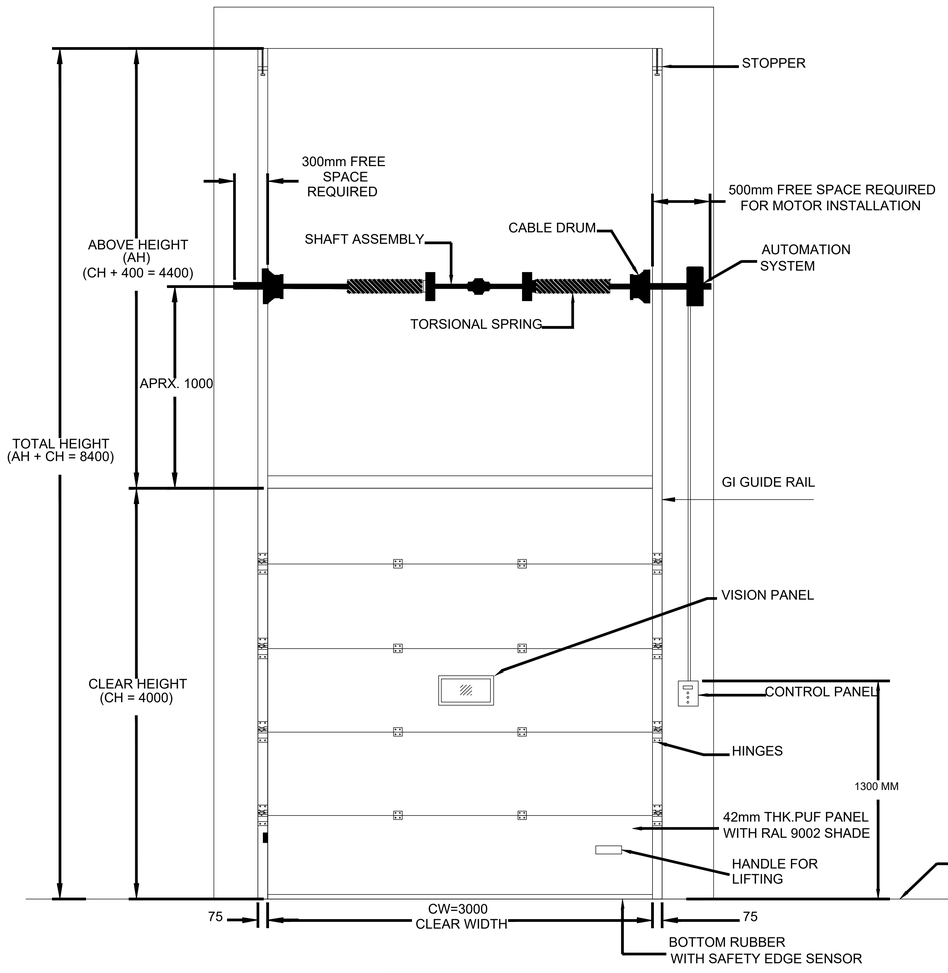



INSIDE ELEVATION

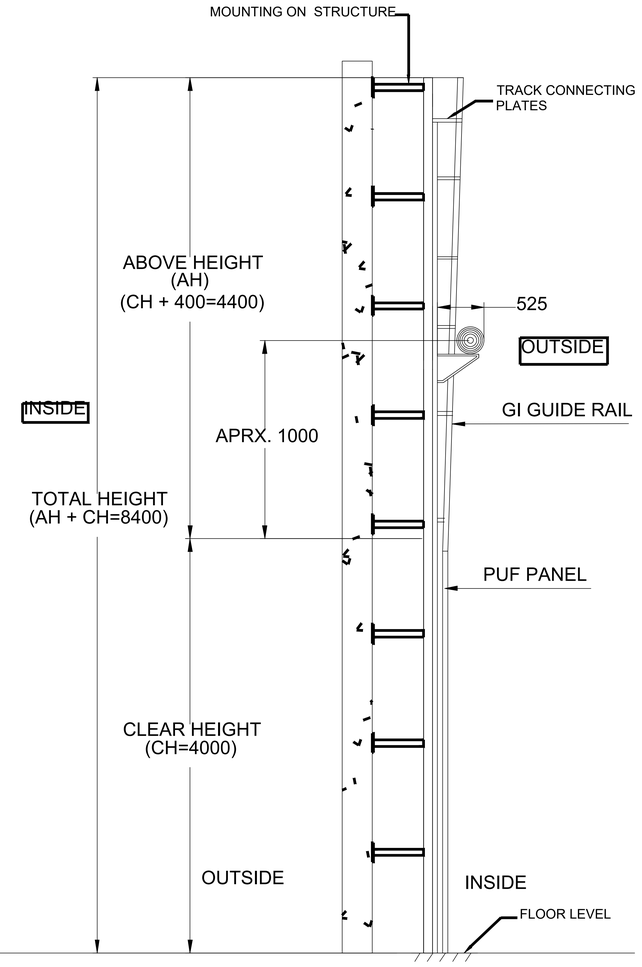

SIDE VIEW

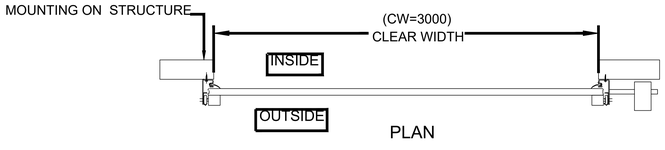

PLAN

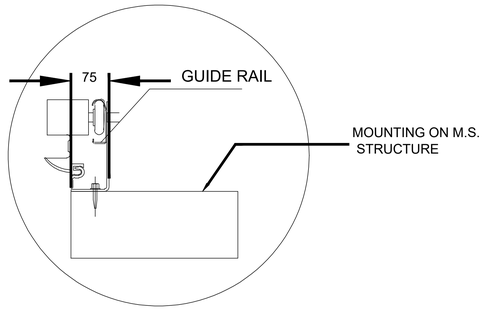

TRACK DETAILS

NOTE:-
1.All dimension are in MM
2.Required all civil work will be Client scope
3.Required structure will be client scope

DIMENSION :

CLEAR WIDTH (CW)	CLEAR HEIGHT (CH)	QUANTITY
3000 mm	4000 mm	03 NOS

TECHNICAL DATA :

COMPONENTS	MATERIALS	SPECIFICATIONS
DOOR PANELS	GI & PUF	42mm CFC- FREE POLYURETHANE WITH 0.5mm THK, GI PRECOATED PANELS.
DOOR HINGE	——	HEAVY DUTY HINGES FOR INTERLOCKING OF PANELS
SHAFT ASSEMBLY	STD.	TORSIONAL SPRING WITH SHAFT & BEARING PLATES
FINISH		PANELS WILL BE COLORED IN STANDARD RAL SHADE APPROVED BY CLIENT.

ACCESSORIES-
1. SAFETY EDGE SENSOR.
2. MANUAL ROPE.
3. SPRING BREAK DEVICE(SPRING FAILURE PROTECTION)
4.ONE WINDOWS.
5.ANY POINT STOP(DEADMAN CONTROL)

IMPORTANT NOTES:
1.SINGLE PHASE POWER SUPPLY REQUIRED AT DOOR LOCATION.
2.ALL CIVIL WORK SHALL BE CLIENT'S SCOPE.
3.REQUIRED STRUCTURE FOR DOOR IS IN CLIENT'S SCOPE.

NIHVA TECHNOLOGIES PVT. LTD. PUNE
Email:- info@nihva.com
Website:- www.nihva.com

TITLE:
OVERHEAD SECTIONAL DOOR - VL

CLIENT'S APPROVAL :

CLIENT - MOTHERSON

PROJECT -

SITE LOCATION -

DWG. NO. : NIHVA23-24CLT066


SCALE: NTS	WT:	SHEET:1 OF 1	REV- 0

	NAME	DATE	SIGN
DRAWN	SUMIT.J	29-11-2023	
CHECK	A.K.	29-11-2023	
APPROVAL	V.T.	29-11-2023	

If any queries contact : design1@nihva.com

NOTE: ALL DIMENSIONS ARE IN mm

THIS DRAWING & DESIGNING IS THE PROPERTY OF NIHVA TECHNOLOGIES. NOT TO BE SOLD OR COPIED TO ANY OTHER CONCERN.

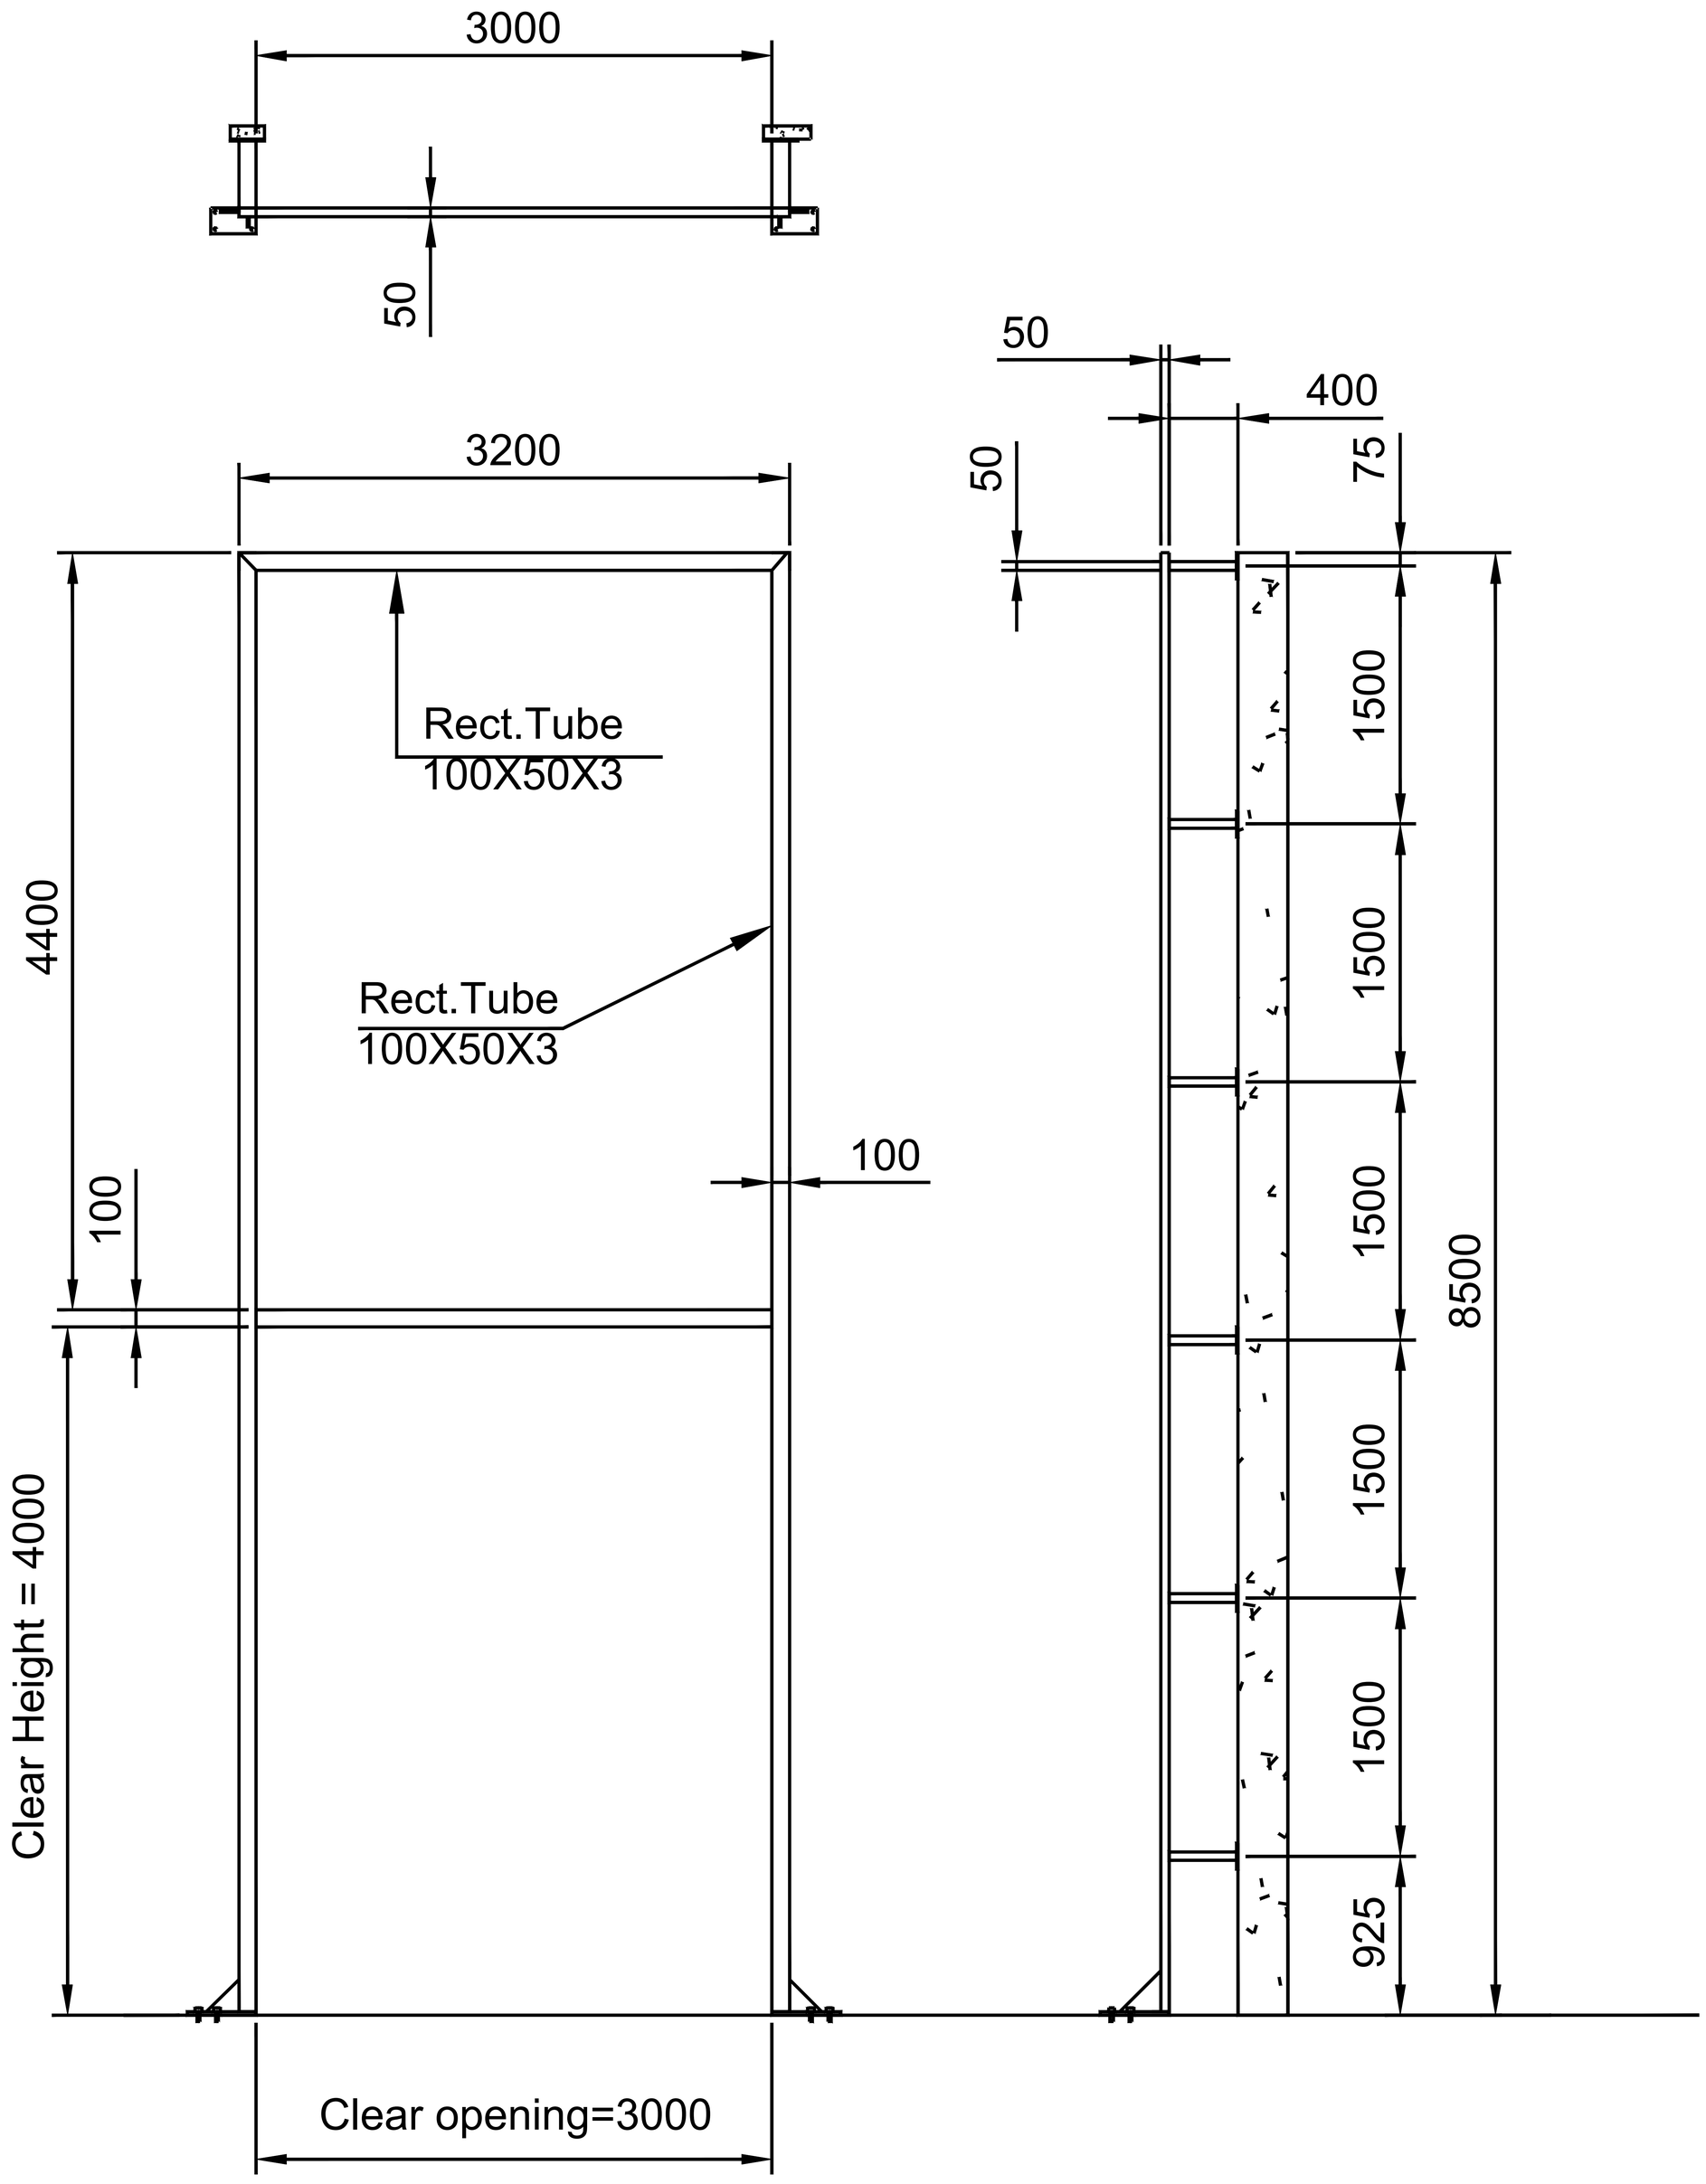

NOTE:-

1.All dimension are in MM

2.Required all civil work will be Client scope

3.Required 100X50X3 rect tubular structure will be client scope

Rev No.	Revision	Date	Revised By

TITLE:- MS Rect.tubular structure - VL

	NAME	DATE	SIGN
DRAWN	NIRMALA	27-09-2023	
CHECK	A.K	27-09-2023	
APPRD.	V.T	27-09-2023	

If any queries contact : design@nihva.com

ALL DIMENSION ARE IN mm

NIHVA TECHNOLOGIES PVT. LTD. PUNE
Tel : 020 66304033
Email:- info@nihva.com
Website:- www.nihva.com

CLIENT - MOTHERSON

LOCATION - PUNE

PRODUCT - | QTY :- 03 NOS

DWG NO:-NIHVA23-24CLT067 | REV- 0

SCALE:NTS | SCALE:-- 1:1 | SHEET: 01 OF 01