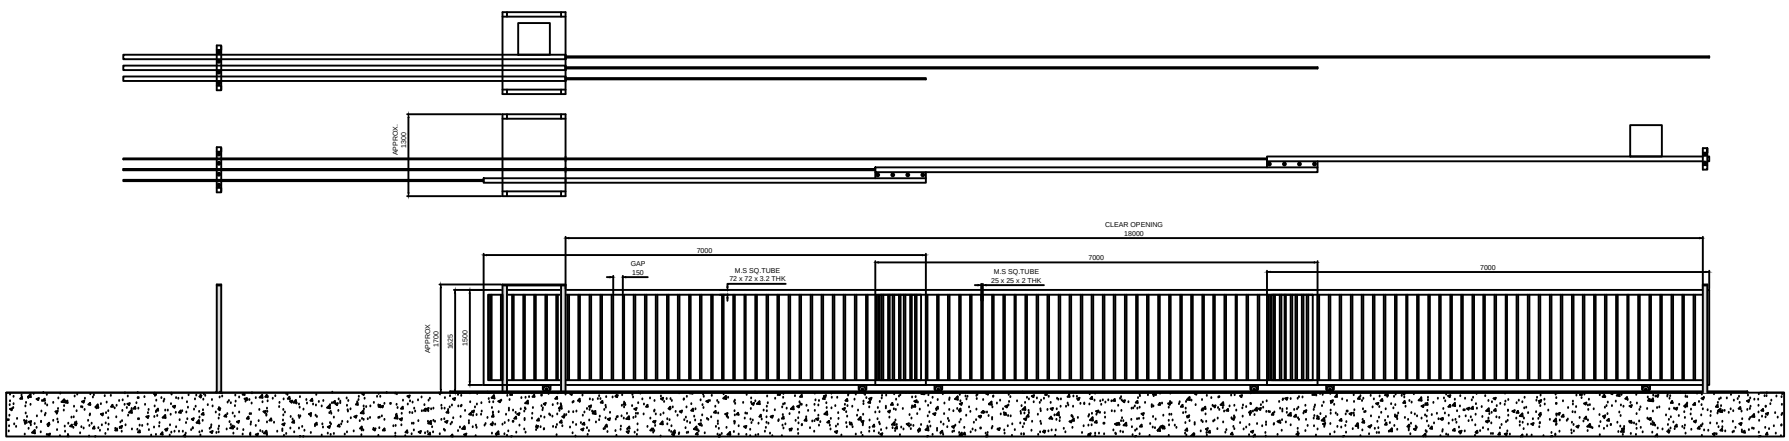
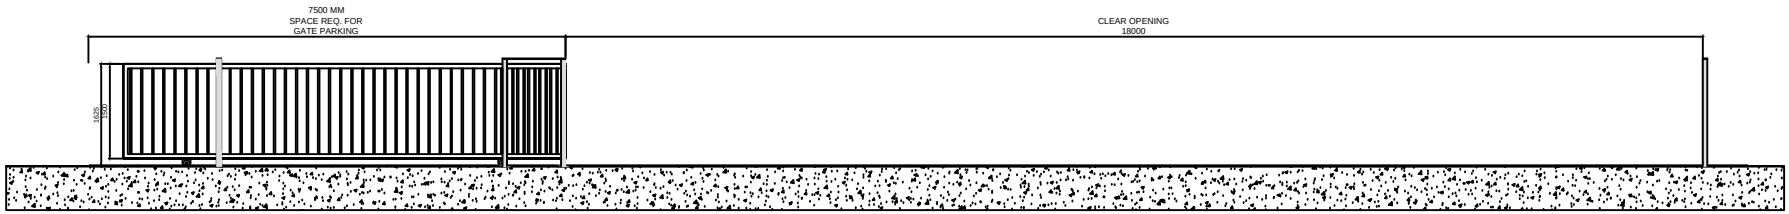



This drawing & design is the property of NIHVA TECHNOLOGIES. Not to be sold or copied to any other concern.

TITLE
AUTOMATIC 3 LEAF
TELESCOPIC SLIDING GATE

NIHVA
NIHVA TECHNOLOGIES PVT. LTD.

NIHVA TECHNOLOGIES
PVT. LTD. PUNE
Tel : 020 66304033
Email:- info@nihva.com
Website:- www.nihva.com

| | NAME | SIGN | DATE |
|---|---|---|---|
| DRAWN | P.A | | 17.02.2020 |
| CHECK | G.J | | 17.02.2020 |
| APPRD. | | | |

CLIENT - AU
PROJECT - ARAYMOND
SITE LOCATION - CHAKAN

If any queries contact : design@nihva.com
DWG. NO. : NIHVA/19-20/0215
REV- R00

ALL DIMENSION ARE IN mm
SCALE: NTS
WT:
SHEET: