

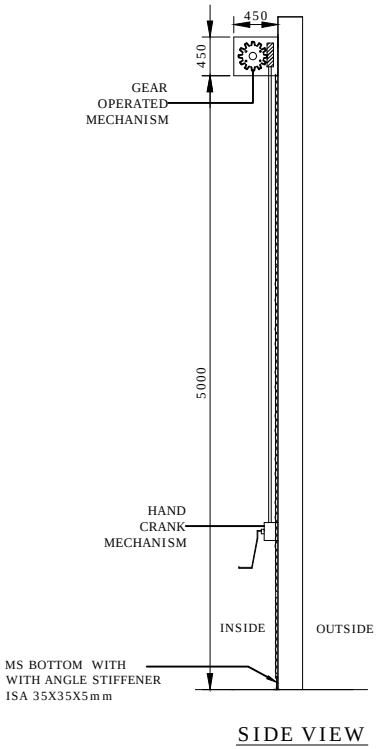



SIDE VIEW

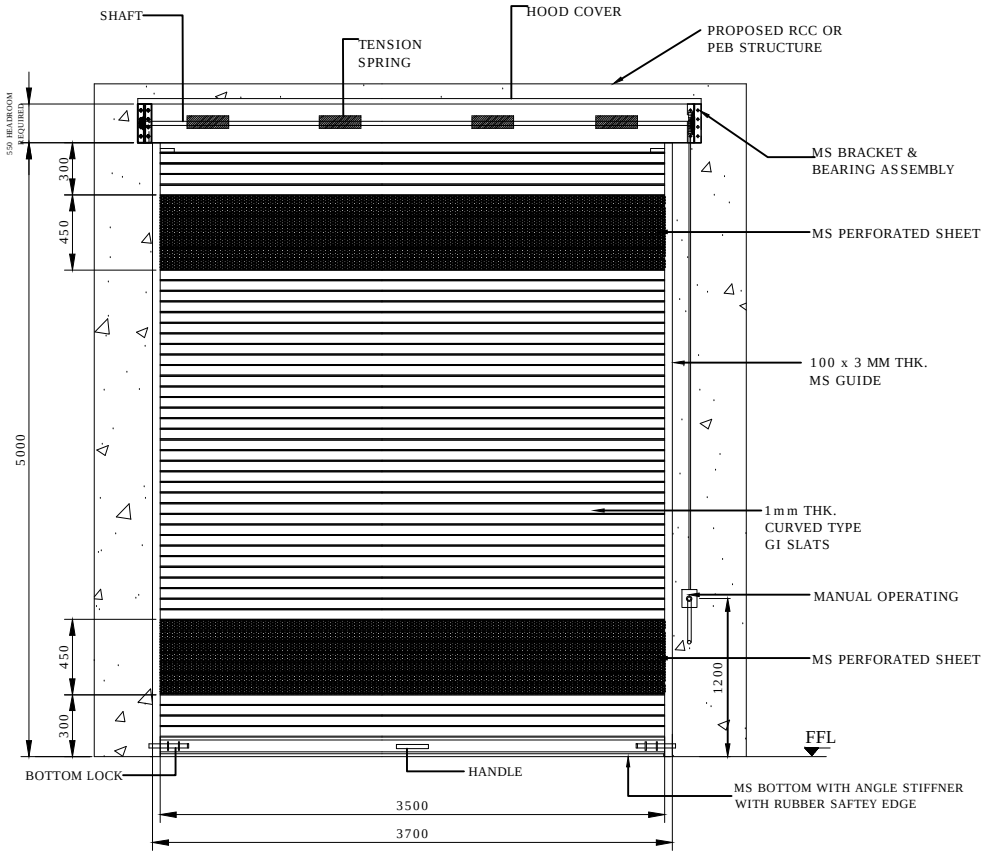


INSIDE ELEVATION

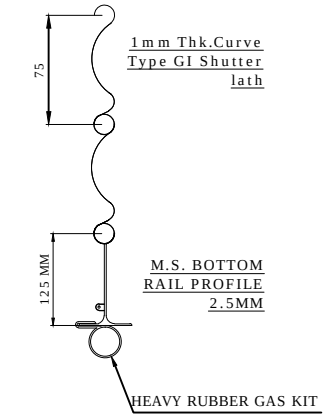

M.S. BOTTOM RAIL PROFILE 2.5MM

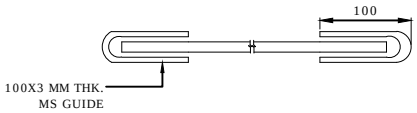

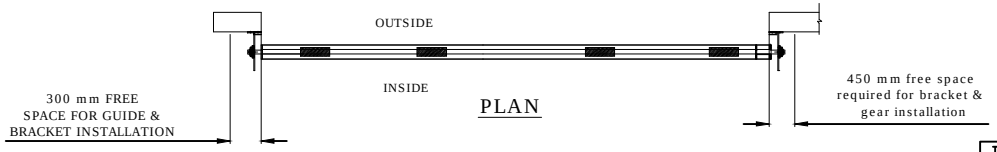

PLAN

TOLERANCE : +/- 10 MM

RAL CODE : RAL 7001 (GREY)

CLEAR WIDTH	CLEAR HEIGHT	QUANTITY
3500	5000	02

This drawing & designing is the property of NIHVA TECHNOLOGIES. Not to be sold or copied to any other concern.

TITLE	GEAR OPERATED ROLLING SHUTTER 3.5mX5m With Right side gearbox	NIHVA TECHNOLOGIES PVT. LTD. PUNE Tel : 020 66304033 Email:- info@nihva.com Website:- www.nihva.com

	NAME	DATE
DRAWN	P.A	31/01/19
CHECK	V.T	31/01/19
APPROVE		

CLIENT - ARAWADE

PROJECT -

SITE - PUNE

DWG. NO. : NIHVA/18-19/0263 | REV : 00

If any queries contact : projects@nihva.com | SCALE: NTS | WT: | SHEET: 01 OF 01

ALL DIMENSION ARE IN mm