


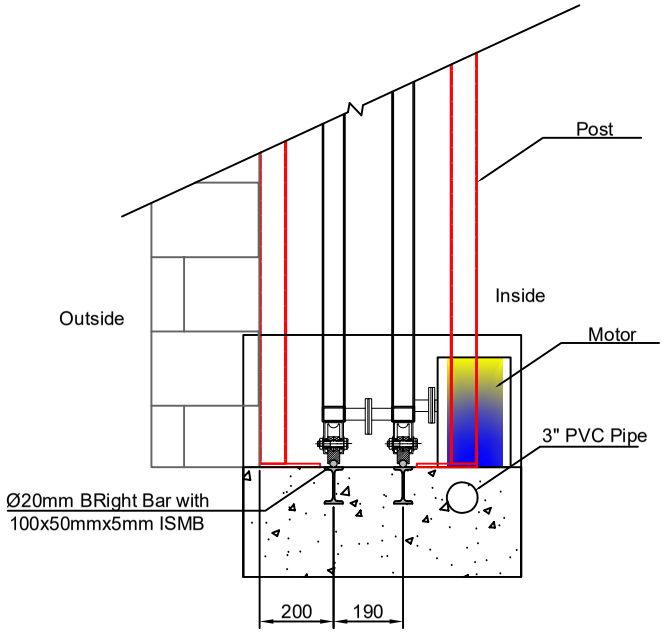

This drawing & design is the property of NIHVA TECHNOLOGIES. Not to be sold or copied to any other concern.

TITLE:- Bi-Parting Tel.Sliding Gate Foundation

NIHVA TECHNOLOGIES PVT. LTD.
NIHVA TECHNOLOGIES PVT. LTD. PUNE
Tel : 020 66304033
Email:- info@nihva.com
Website:- www.nihva.com

	NAME	DATE	SIGN
DRAWN	SUJATA	18/06/2022	
CHECK			
APPRD.	M.S	18/06/2022	

If any queries contact : design@nihva.com

ALL DIMENSION ARE IN mm

CLIENT - NAVNEET EDUCATION LTD

LOCATION - PALGHAR

PRODUCT - TEL.SLIDING GATE

DWG NO:-NIHVA/22-23/CLT/0062 | REV- 0

SCALE: NTS | SCALE:-- 1:1 | SHEET: 01 OF 01

Rev No.	Revision	Date	Revised By