
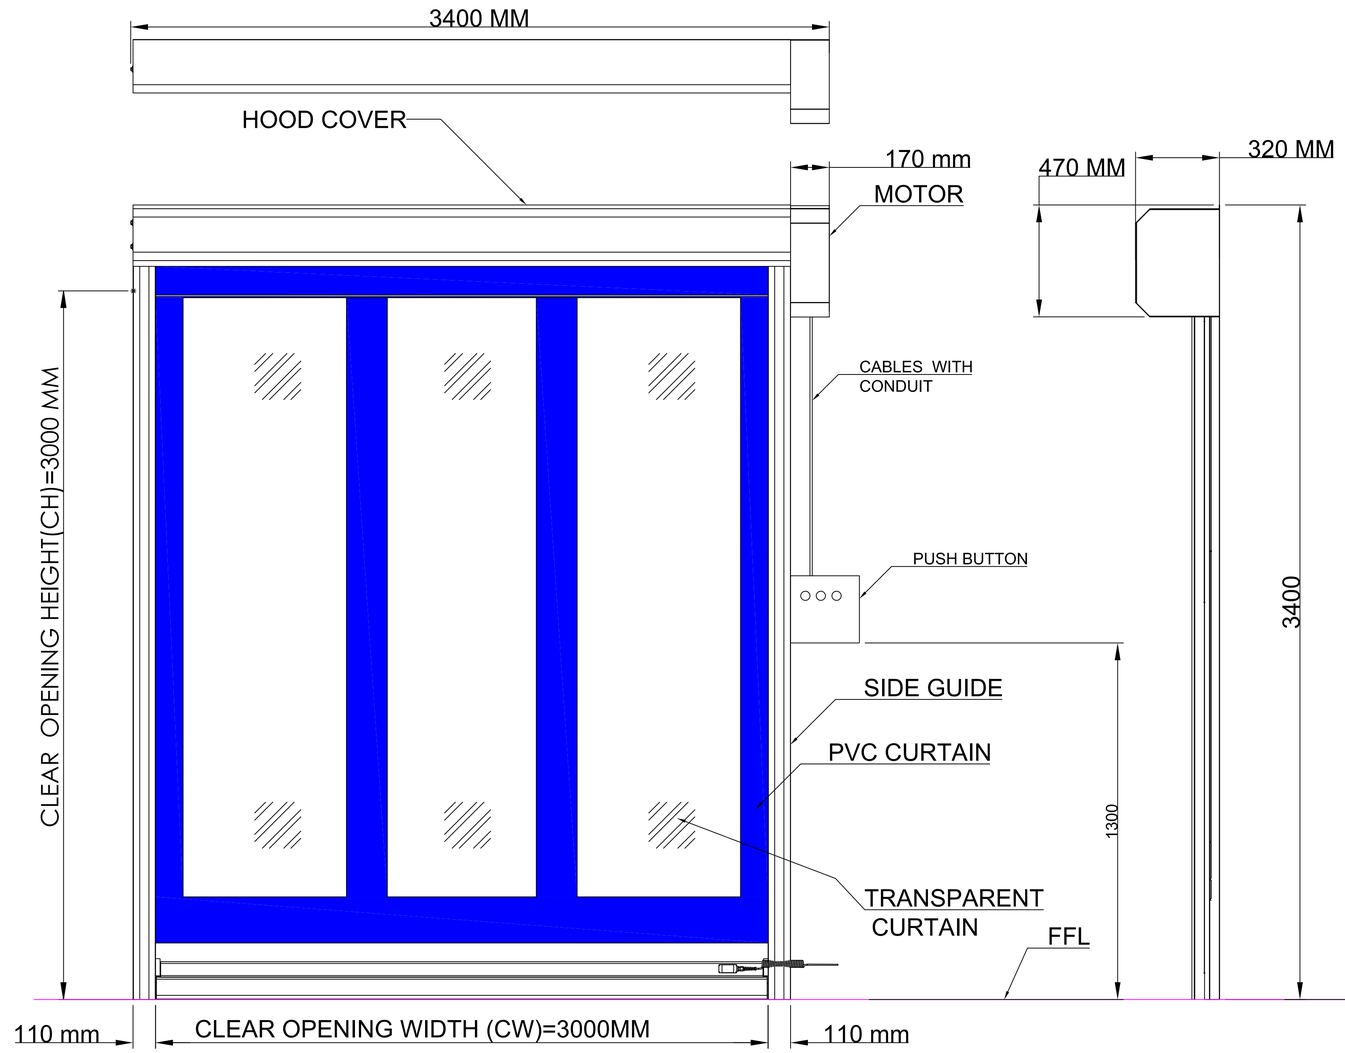


HIGH SPEED DOOR

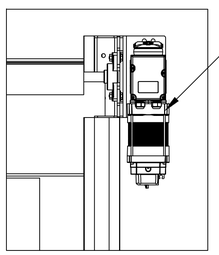


Speed	Inverter Motion system to adjust different speeds, with progressive control of acceleration & deceleration during braking		
	Opening Speed up to		3,0 m/s
	Closing Speed		0,8 m/s
Security Features	EN 13241-1		Standard
Resistance to Wind Load	EN 12424		up to Class 2
Curtain Stabilisation / Wind Load	Aluminium anodized windbars		Standard
Curtain	Fabric	0.9 - 1.5 mm	Standard
	Transparent PVC section	2.0 mm	Standard
Guide Material / Surface	Aluminium Anodized		Standard
	Painting in any RAL color		Optional
	Stainless Steel SS 316 matte finish		Optional
Shaft / Operator Cover	Straight		Optional
Operator and Control (German brand)	Connecting Voltage		220V - 1ph, N
	Open-Stop-Close Button		Standard
	Protection Category (Operator / Control)		IP 54 / IP 65
	Emergency-OFF Button		Standard
	Closing Zone Monitoring	Light Curtain	Optional
		optical safety edge	Standard
	External Route Monitoring	Photocell	Standard
	Door area Monitoring	Radar Presence Detector	Optional
		Induction Loop	Optional
	Electronic Limit Switch		Standard
Emergency Opening	Crank Handle		Standard
	Counterweight system		Optional
	Chain		Optional


NOTE:
1. REQUIRED STRUCTURE , FITTING & ALL CIVIL WORK IS IN CLIENT SCOPE.
2. STRUCTURE SHOULD BE RIGID & NEED TO BE FIXED/WELDED WITH EXISTING STRUCTURE AT SITE(IN CLIENT SCOPE).

REV NO	DRAWN	DATE	REMARK
R03	S.M.S.	31.12.2020	STRUCTURE DRAWING REVISED
R02	S.M.S.	29.12.2020	STRUCTURE MATERIAL CHANGED TO S.S. MOTOR POSITION RIGHT SIDE
R01	S.M.S.	24.12.2020	M.S. STRUCTURE MOUNTING QUANTITY ADDED

RAL CODE FOR PVC CURTAIN-BLUE

3000	3000	3 NOS	RH
CLEAR OPENING WIDTH (CW)	CLEAR OPENING HEIGHT (CH)	QUANTITY	MOTOR POSITION

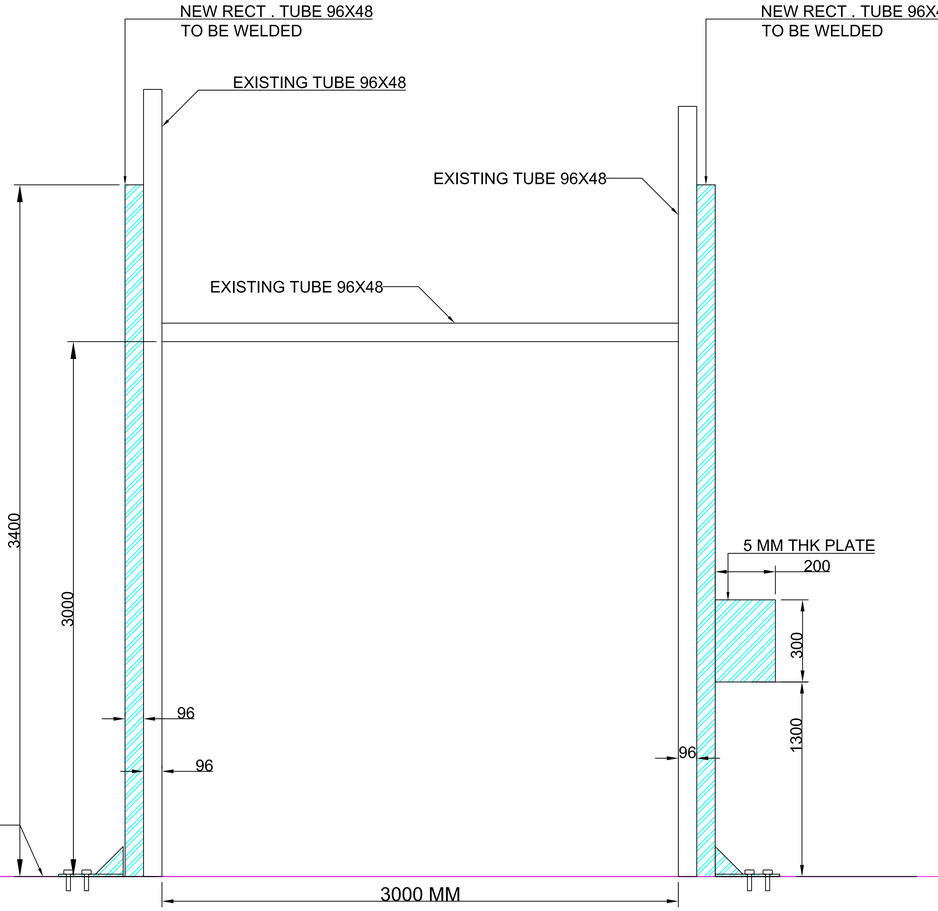

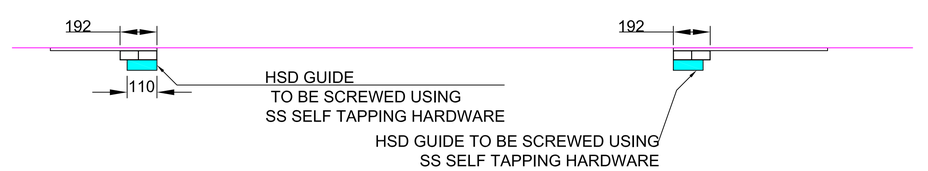

STRUCTURE DRAWING(CLIENT SCOPE)

This drawing & design is the property of NIHVA TECHNOLOGIES. Not to be sold or copied to any other concern.

TITLE NIHVA MAKE HIGH SPEED DOOR 3000X3000

	NAME	SIGN	DATE
DRAWN	S.M.S.		22.12.2020
CHECK	A.K.		22.12.2020
APPRD.			

NIHVA TECHNOLOGIES PVT. LTD.
NIHVA TECHNOLOGIES PVT. LTD. PUNE
Tel : 020 66304033
Email:- info@nihva.com
Website:- www.nihva.com

CLIENT - TRANS ENGINEERS INDIA PVT LTD

PROJECT - MARS INTERNATIONAL INDIA PVT LTD

SITE LOCATION - PUNE

If any queries contact : design@nihva.com

DWG. NO. : NIHVA/20-21/0115/R03 REV- R03

ALL DIMENSION ARE IN mm

SCALE: NTS WT: SHEET: 2 OF 2