
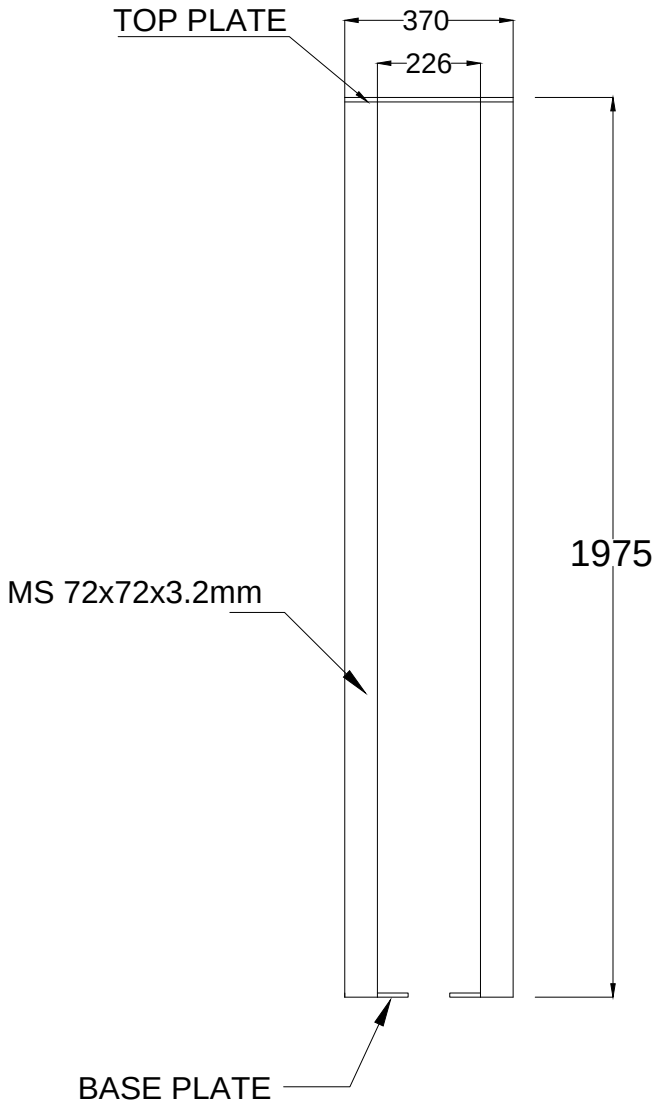



POST

MATERIAL:-MS
QTY:- 08NOS

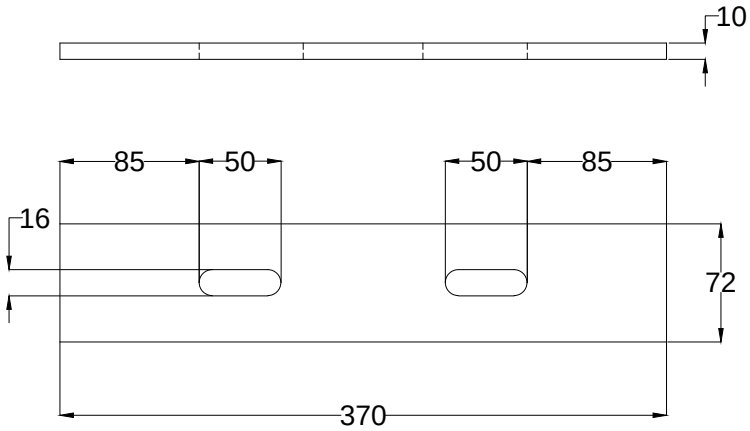

TOP PLATE

MATERIAL:-MS
THICKNESS:-10mm
QTY:- 08NOS

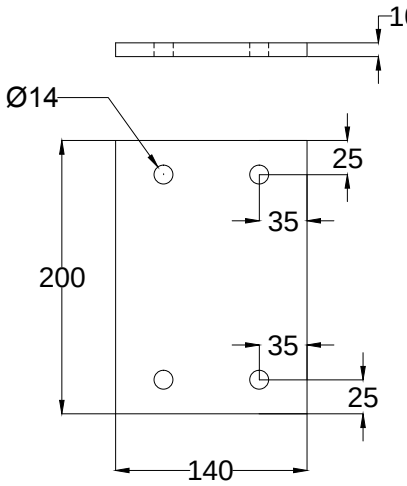

BASE PLATE

MATERIAL:-MS
THICKNESS:-10mm
QTY:- 16 NOS

SR NO	TUBE SPECIFICATION		MATERIAL
1	72X72X3.2mm MS TUBE	POST	MILD STEEL
2	370X72X10mm MS PLATE	TOP PLATE	MILD STEEL
3	200X140X10mm MS PLATE	BOTTOM PLATE	MILD STEEL

This drawing & designing is the property of NIHVA TECHNOLOGIES. Not to be sold or copied to any other concern.

TITLE: SLIDING GATE POST DRAWING

NIHVA TECHNOLOGIES PVT. LTD.
NIHVA TECHNOLOGIES PVT. LTD. PUNE
Tel : 020 66304033
Email:- info@nihva.com
Website:- www.nihva.com

	Name	SIGN	DATE
DRAWN	SURAJ		15/10/18
CHECK	PRADEEP		15/10/18
APPROVAL	R.D		15/10/18

CLIENT -
PROJECT -
SITE LOCATION -
If any queries contact : design@nihva.com
DWG. NO. : NIHVA/18-19/VDR/173
REV.:- 0
ALL DIMENSION ARE IN mm
SCALE: NTS
WT:
SHEET: 01 OF 01