



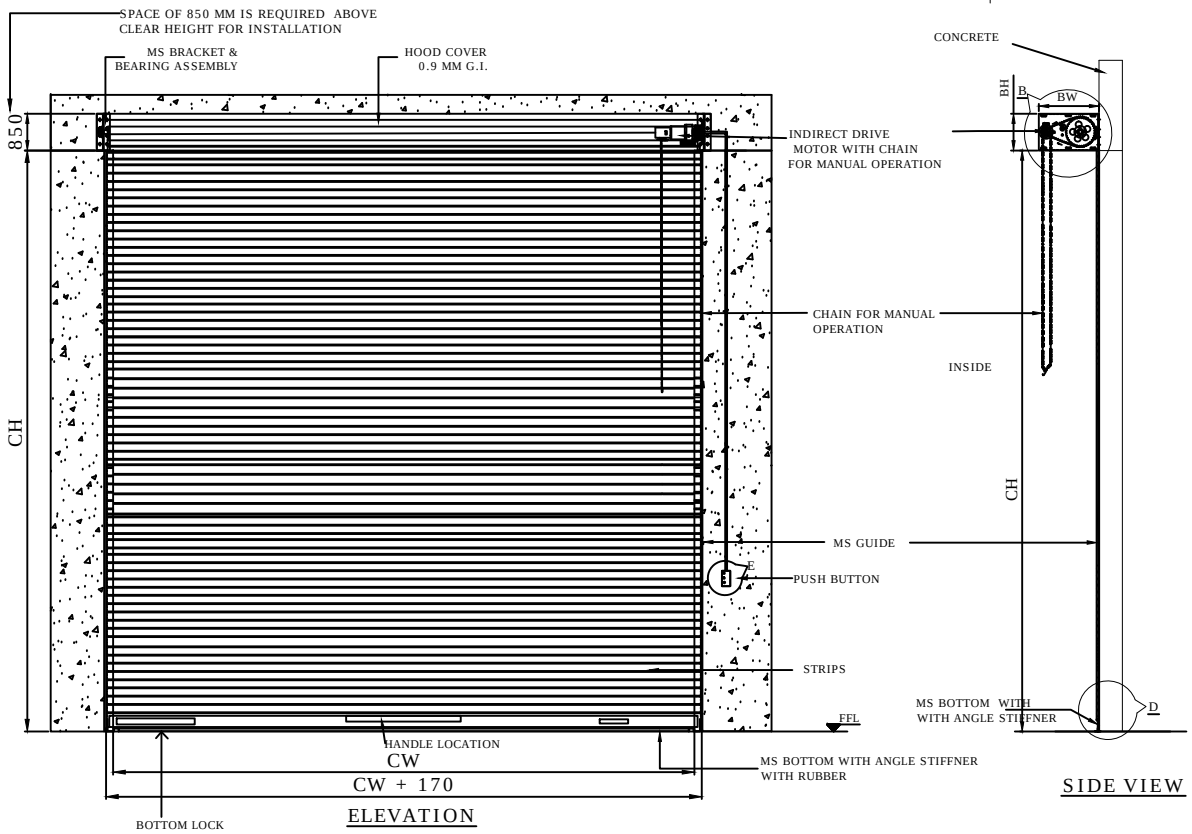

BOX GUIDE DETAILS


NOTE:
1. REQUIRED MS STRUCTURE , FITTING & ALL CIVIL WORK IS IN CLIENT SCOPE.
2. SPACE OF 850 MM IS REQUIRED ABOVE CLEAR HEIGHT FOR ROLLING SHUTTER INSTALLATION .

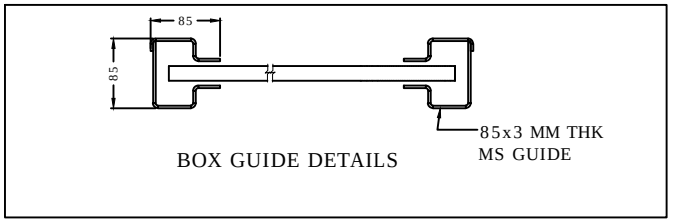


PLAN

REV NO	DRAWN	DATE	REMARK
R01	S.M.S.	31.3.2021	QTY ADDED & RAL SHADE CONFIRMED


SR NO	CLEAR WIDTH (CW)	CLEAR HEIGHT (CH)	QUANTITY	RAL COLOR POWDER COATED
3	4000	5000	3 NOS	RAL 9002
2	4000	4000	4 NOS	RAL 9002
1	3700	4000	1 NO	RAL 9002

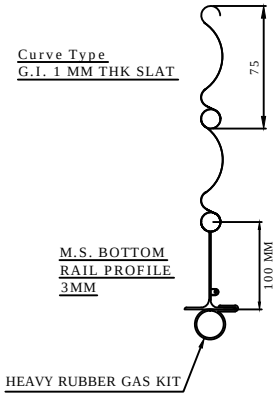

DETAILS : D

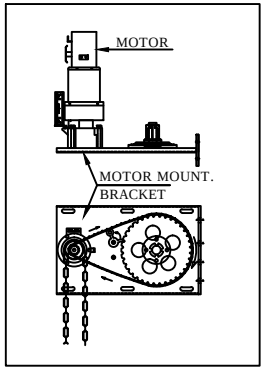

DETAILS : A & B

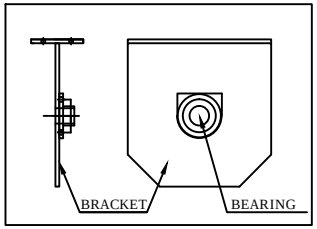

DETAILS : C

RAL CODE	SHADE	COLOUR
RAL 9002	GREY WHITE	

This drawing & design is the property of NIHVA TECHNOLOGIES. Not to be sold or copied to any other concern.

TITLE: GI MOTORIZED INDIRECT DRIVE ROLLING SHUTTER

NIHVA TECHNOLOGIES PVT. LTD.
NIHVA TECHNOLOGIES PVT. LTD. PUNE
Tel : 020 66304033
Email:- info@nihva.com
Website:- www.nihva.com

	NAME	SIGN	DATE
DRAWN	S.M.S.		16.3.2021
CHECK	S.M.S.		16.3.2021
APPRD.			

CLIENT - ARP CONSTRUCTION
PROJECT - JOHN DEERE
SITE LOCATION - SANASWADI , PUNE

If any queries contact : projectsupport@nihva.com
DWG. NO. : NIHVA/20-21/0177/R01
REV- R01

ALL DIMENSION ARE IN mm
SCALE: NTS
WT:
SHEET: