


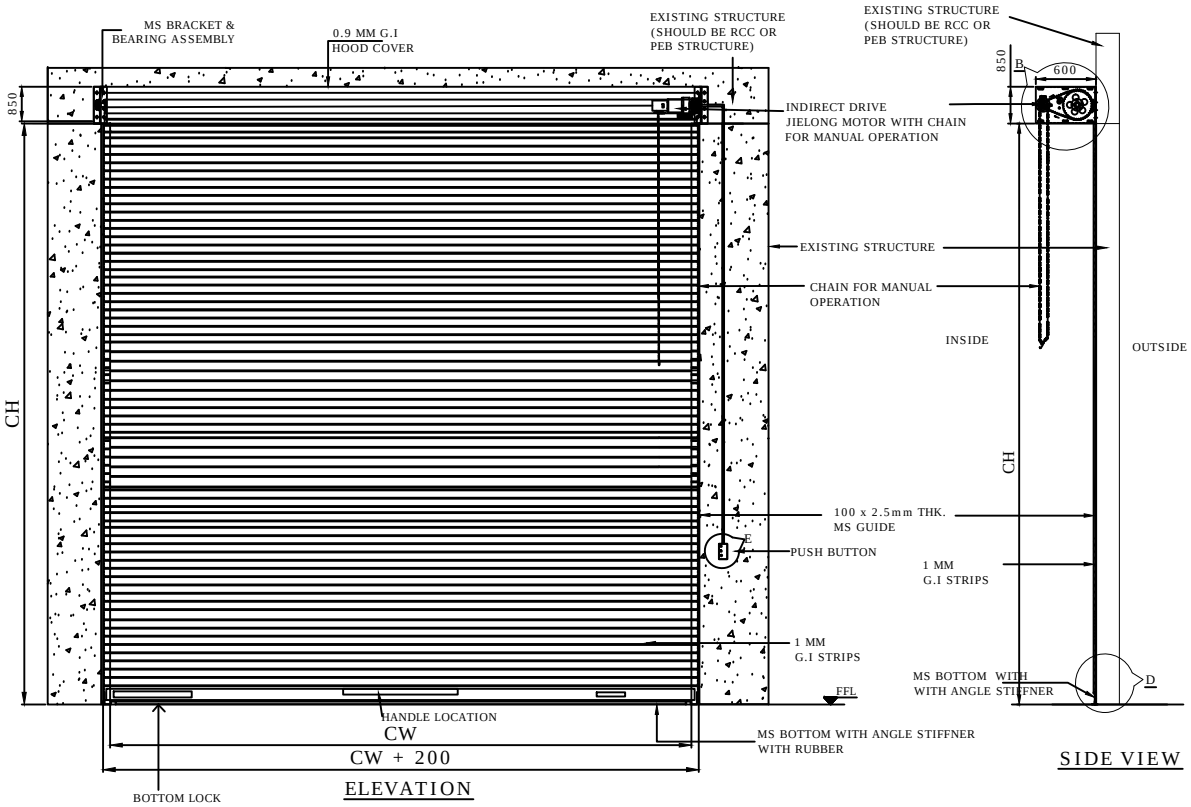


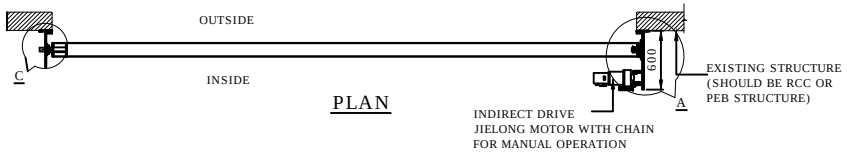


PLAN

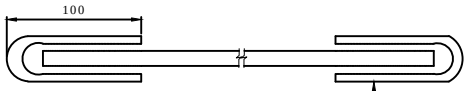


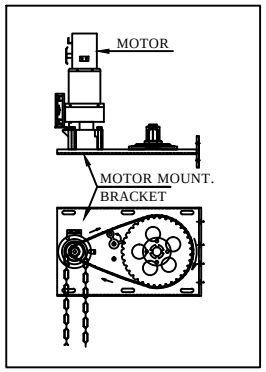

DETAILS : A & B

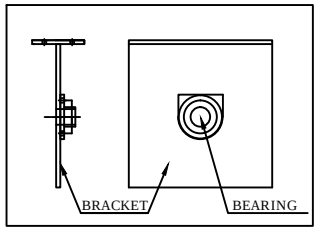

DETAILS : C

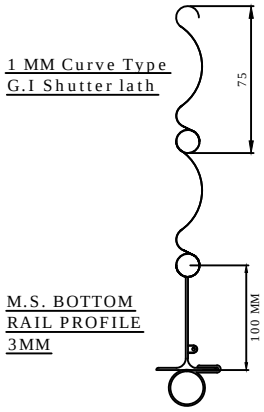

DETAILS : D

(NOTE: IF REQUIRED TECHNICAL STRUCTURE FOR SHUTTER IS IN CLIENT SCOPE)

			RAL 3001	
			RAL 7035	
			RAL 5002	
4500	3000	2 NOS	RAL 9010	
CLEAR WIDTH (CW)	CLEAR HEIGHT (CH)	QUANTITY	STD RAL CODE	APPROVED

This drawing & design is the property of NIHVA TECHNOLOGIES. Not to be sold or copied to any other concern.

TITLE: MOTORIZED ROLLING SHUTTER

NIHVA TECHNOLOGIES PVT. LTD.

NIHVA TECHNOLOGIES PVT. LTD. PUNE
Tel : 020 66304033
Email:- info@nihva.com
Website:- www.nihva.com

	NAME	SIGN	DATE
DRAWN	P.A		12.08.2020
CHECK	G.J		12.08.2020
APPRD.			

CLIENT - NITESH GUNDEJA

PROJECT -

SITE LOCATION - PUNE

If any queries contact : design@nihva.com

DWG. NO. : NIHVA/20-21/0042 REV- R00

ALL DIMENSION ARE IN mm

SCALE: NTS WT: SHEET: