
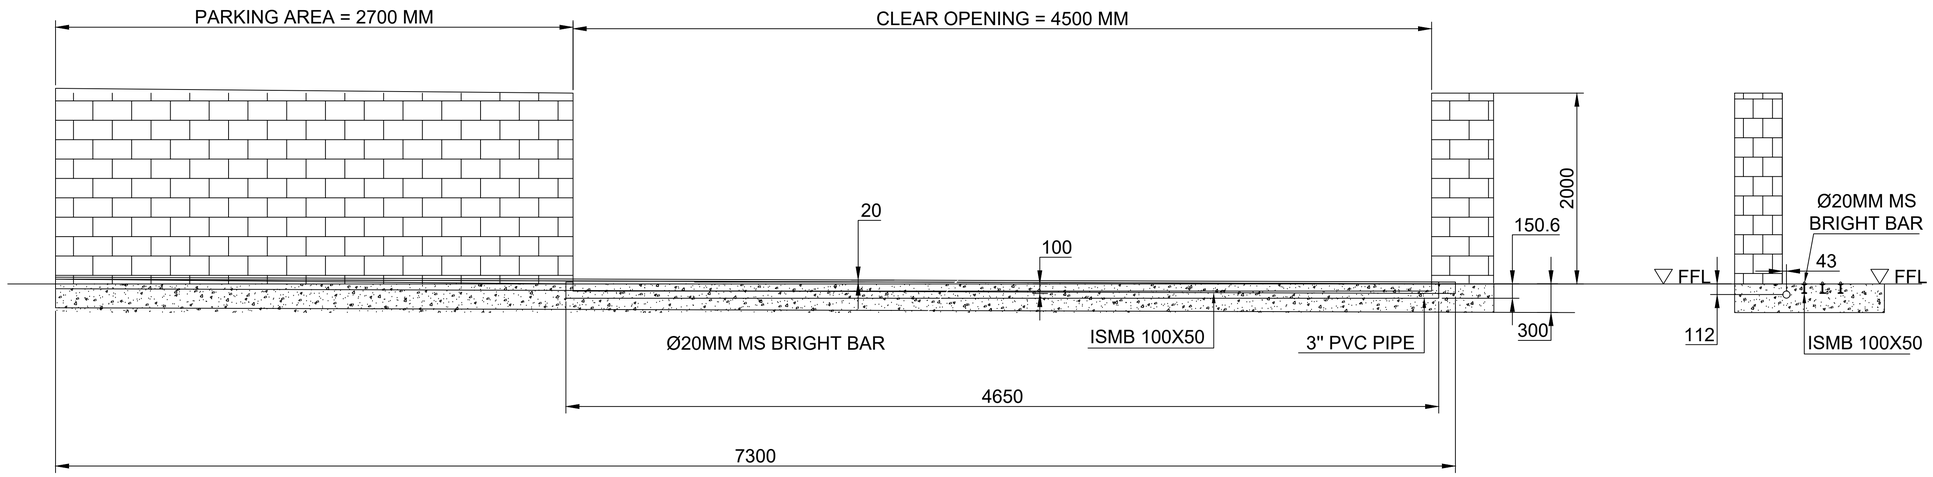


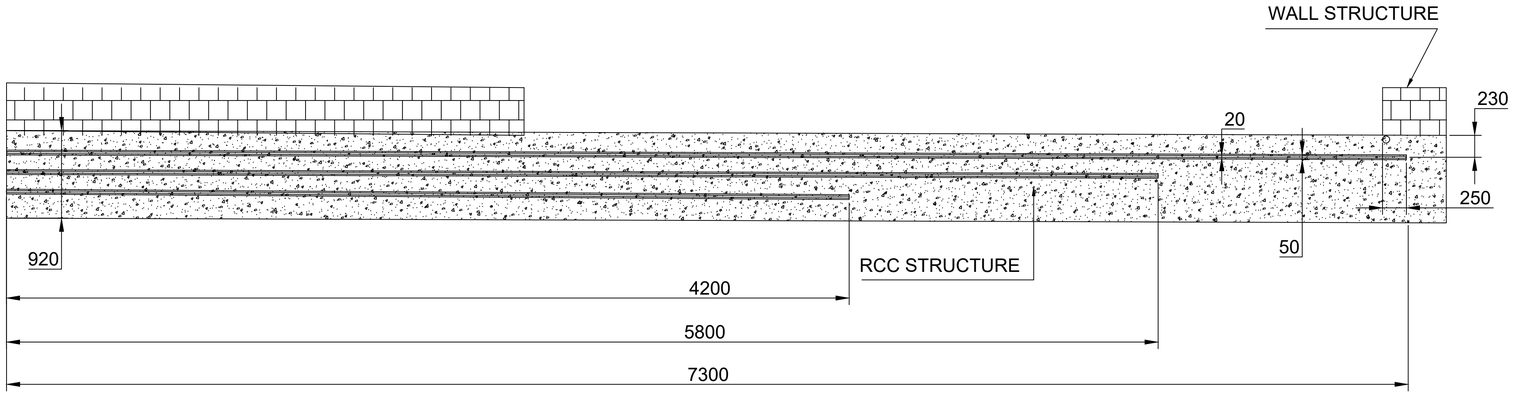

Technical Specs of Motorized Sliding Gate

1. Parking length required - 2700 + mm
2. Bottom Rail - Bright bar Ø20mm

ISMB 100 X 50 positioned in the foundation (client scope).

Note-

1. All dimension are in mm.
2. All civil work is under client scope.
3. 3" PVC pipe in the foundation to be provided by client.
4. Power supply single phase 230v, 50hz. is in client scope.

Rev No.	Revision	Date	Revised By

This drawing & design is the property of NIHVA TECHNOLOGIES. Not to be sold or copied to any other concern.

TITLE:- Foundation Drawing for Sliding Gate

	NAME	DATE	SIGN
DRAWN	M. SUTAR	04/08/2022	
CHECK	M. SUTAR	04/08/2022	
APPRD.	A.KURHADE	04/08/2022	

If any queries contact : design@nihva.com

ALL DIMENSION ARE IN mm

NIHVA TECHNOLOGIES PVT. LTD.

NIHVA TECHNOLOGIES PVT. LTD. PUNE
Tel : 020 66304033
Email:- info@nihva.com
Website:- www.nihva.com

CLIENT -MEGAWIDE CONSTRUCTION

LOCATION - GMR GOA INTERNATIONAL AIRPORT LIMITED

PRODUCT - SLIDING GATE QTY:-

DWG NO:- NIHVA/22-23/CLT/0101 REV- 0

SCALE: NTS SCALE:-- 1:1 SHEET: 01 OF 01